
DIAGRAMA UNIFILAR CC

Strings separadas, proteção, seccionamento e entradas MPPT

DUAS STRINGS INDEPENDENTES - SEM PARALELISMO

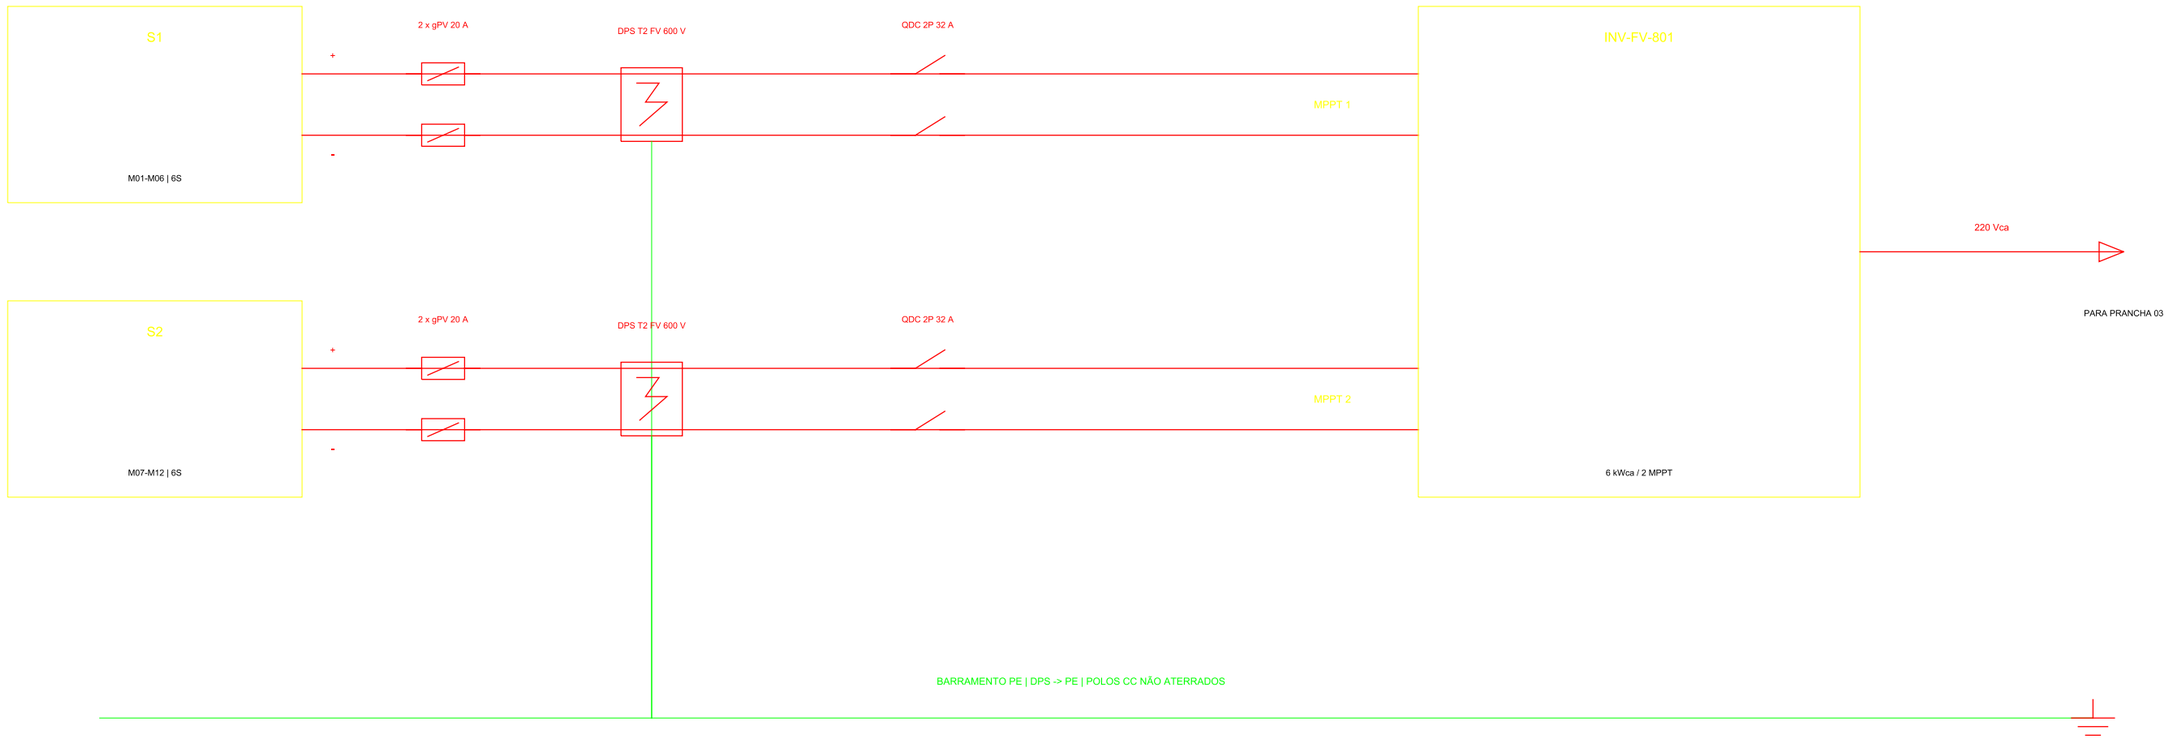

CONDIÇÃO	TENSÃO	LIMITE	RESULTADO
Voc frio	324,550 V	< 600 V	ATENDE PREM.
Vmp quente	216,942 V	90-550 V	ATENDE PREM.

LEGENDA

F: fusível gPV | DPS: proteção contra surtos | QDC: seccionador | PE: proteção

NOTAS DA PRANCHA

Polos positivo e negativo não são intencionalmente aterrados neste conceito.
Tensões e correntes derivam de dados fictícios e exigem validação do fabricante.

AVISO OBRIGATORIO

Projeto acadêmico e conceitual. Não deve ser utilizado para fabricação, instalação ou execução de serviços sem revisão, dimensionamento e responsabilidade de profissional legalmente habilitado.

REV.	DATA	DESCRICAO	RESP.
00	2026-09-09	EMISSAO INICIAL DO PROJETO 08	R.E.M.M.

PORTFOLIO DE
ENGENHARIA ELETRICA
BASE ACADEMICA REPRODUZIVEL

A3
PAISAGEM

TITULO

DIAGRAMA UNIFILAR CC

AUTOR	DATA	REV.	PRANCHA
Rogério Eduardo Moreira Menegueli	2026-09-09	00	02/06

ARQUIVO	UNIDADES	ESCALA	FOLHA	STATUS
02_diagrama_unifilar_cc.dxf	mm	S/ESC.	A3	CONCEIT.