
STRING BOX

Proteções CC independentes para S1/MPPT1 e S2/MPPT2

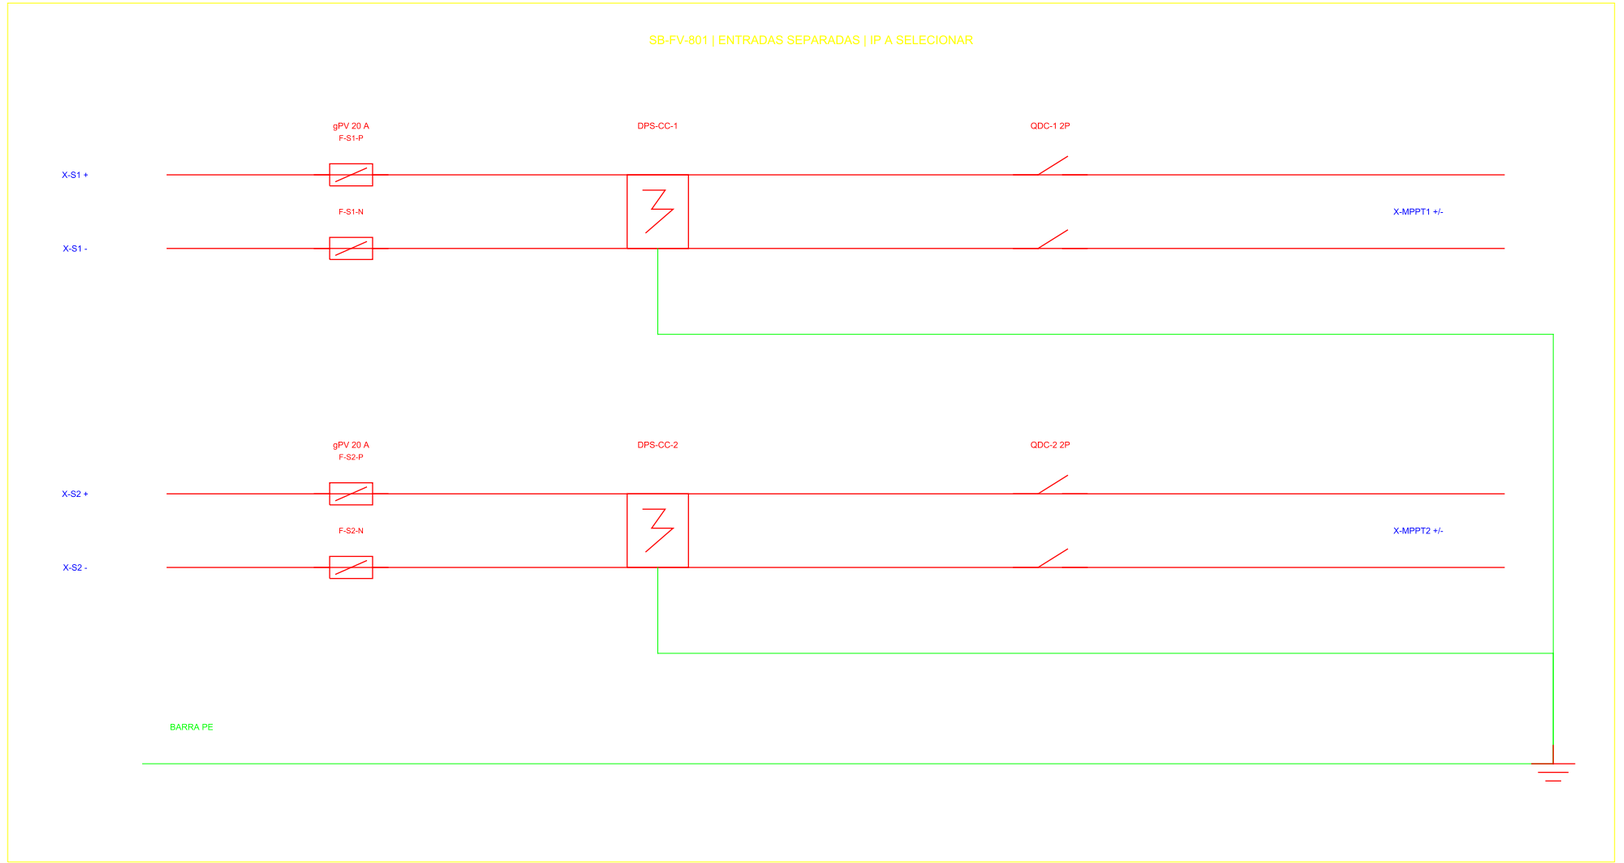

ITEM	ESPECIFICAÇÃO
F-S1-P/N	gPV 20 A / 600 Vcc
F-S2-P/N	gPV 20 A / 600 Vcc
DPS-CC-1	Tipo 2 FV / Ucpv 600 V
DPS-CC-2	Tipo 2 FV / Ucpv 600 V
QDC-1	2P / 32 A / 600 Vcc
QDC-2	2P / 32 A / 600 Vcc

PONTOS DE VERIFICAÇÃO

Polaridade; Ucpv e Up; Icc; capacidade de interrupção; coordenação; grau IP; temperatura; terminais; torque; sinalização.

LEGENDA

gPV: fusível FV | DPS CC: tipo 2 FV | QDC: manobra sob carga | X: terminal

NOTAS DA PRANCHA

A string box não coloca S1 e S2 em paralelo; cada saída alimenta um MPPT.
Confirmar polaridade, Ucpv, Up, corrente, Icc, IP, temperatura e coordenação.

AVISO OBRIGATORIO

Projeto acadêmico e conceitual. Não deve ser utilizado para fabricação, instalação ou execução de serviços sem revisão, dimensionamento e responsabilidade de profissional legalmente habilitado.

REV.	DATA	DESCRICAO	RESP.
00	2026-09-09	EMISSAO INICIAL DO PROJETO 08	R.E.M.M.

PORTFOLIO DE
ENGENHARIA ELETRICA
BASE ACADEMICA REPRODUZIVEL

A3
PAISAGEM

TITULO

STRING BOX

AUTOR	DATA	REV.	PRANCHA
Rogério Eduardo Moreira Menegueli	2026-09-09	00	04/06

ARQUIVO	UNIDADES	ESCALA	FOLHA	STATUS
04_string_box.dxf	mm	S/ESC.	A3	CONCEIT.