
DIAGRAMA UNIFILAR GERAL

Subestacao abrigada 500 kVA - 13,8 kV / 380-220 V e QGBT

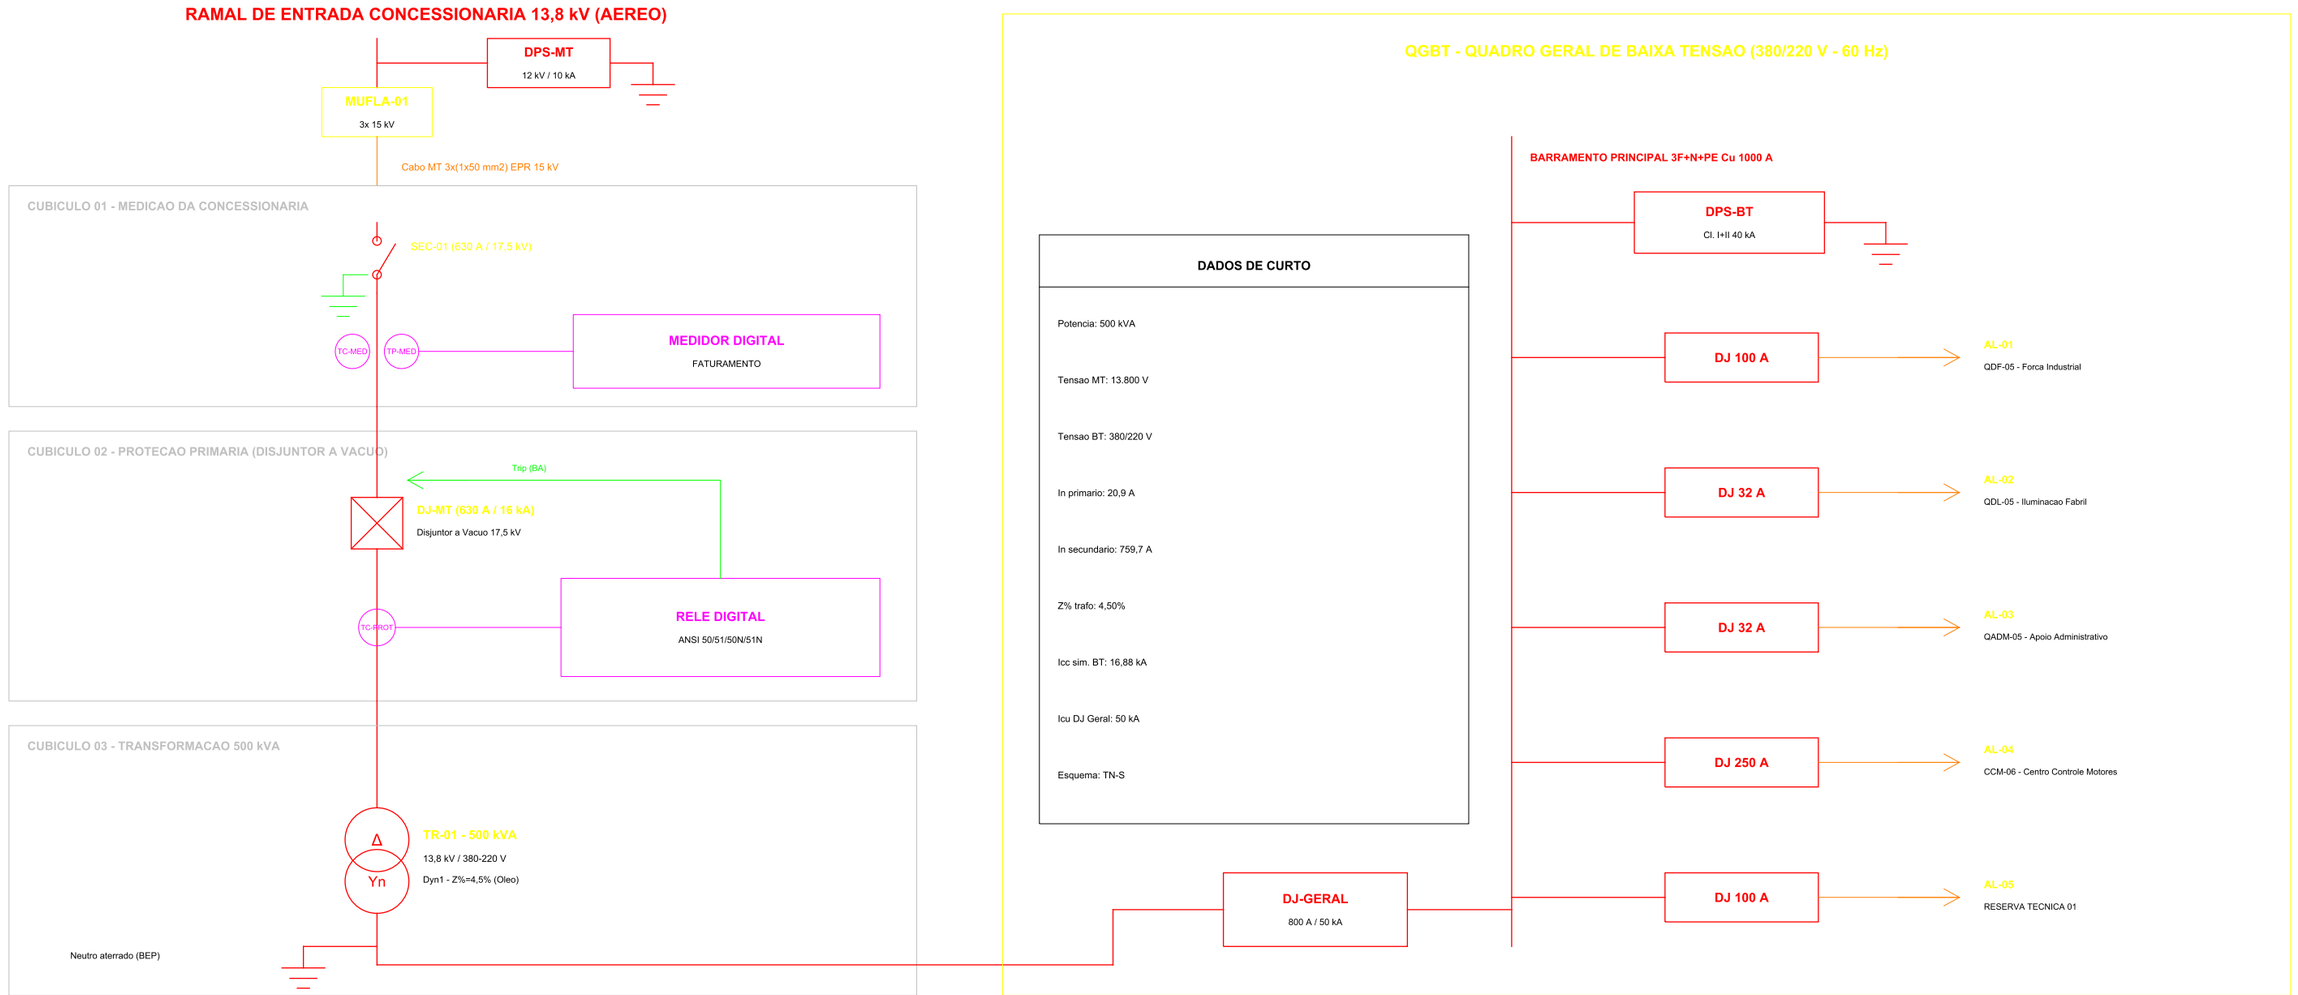

LEGENDA

MT: media tensao | DJ: disjuntor | TC: transfo. corrente | TP: transfo. potencial | DPS: prot. surto

NOTAS DA PRANCHA

Entrada em media tensao 13,8 kV conforme criterios da concessionaria.
Protecao por rele digital 50/51/50N/51N e disjuntor a vacuo 17,5 kV.
Transformador 500 kVA a oleo mineral Dyn1 com supervisao termica e Buchholz.

AVISO OBRIGATORIO

Projeto acadêmico e conceitual. Não deve ser utilizado para fabricação, instalação ou execução de serviços sem revisão, dimensionamento e responsabilidade de profissional legalmente habilitado.

REV.	DATA	DESCRICAO	RESP.
00	2026-09-25	EMISSAO INICIAL DO PROJETO 11	R.E.M.M.

PORTFOLIO DE
ENGENHARIA ELETRICA
BASE ACADEMICA REPRODUZIVEL

A3
PAISAGEM

TITULO

DIAGRAMA UNIFILAR GERAL

AUTOR	DATA	REV.	PRANCHA
Rogério Eduardo Moreira Menegueli	2026-09-25	00	01/06

ARQUIVO	UNIDADES	ESCALA	FOLHA	STATUS
01_diagrama_unifilar_geral.dxf	mm	S/ESC.	A3	CONCEIT.