
DIAGRAMA UNIFILAR

Arquitetura geral de potência e aterramento

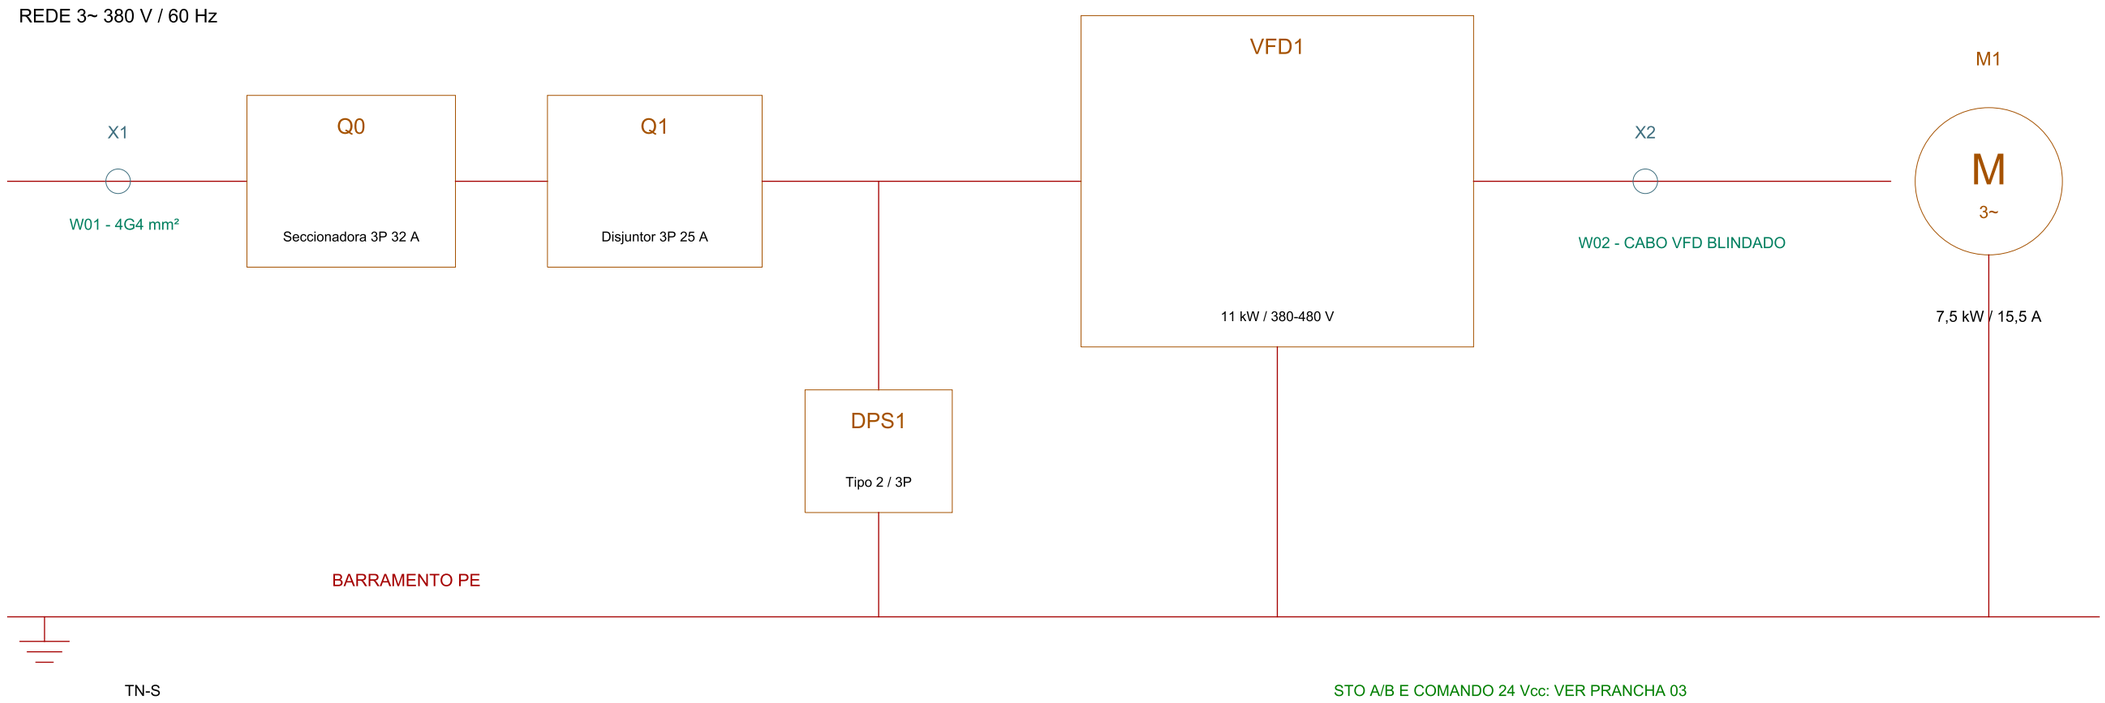

LEGENDA

Q: manobra/proteção | VFD: inversor | X: borne | M: motor | PE: proteção

NOTAS DA PRANCHA

Rede assumida: 380 V, 3 fases, 60 Hz, TN-S. Motor M1: 7,5 kW.
Q0, Q1, DPS1 e VFD1 exigem seleção final por estudo de aplicação.

AVISO OBRIGATÓRIO

Projeto acadêmico e conceitual. Não deve ser utilizado para fabricação, instalação ou execução de serviços sem revisão, dimensionamento e responsabilidade de profissional legalmente habilitado.

REV.	DATA	DESCRIÇÃO	RESP.
03	2026-11-06	REVISAO VISUAL 03	R.E.M.M.

PORTFOLIO DE
ENGENHARIA ELETRICA
BASE ACADEMICA REPRODUZIVEL

A3
PAISAGEM

TITULO

DIAGRAMA UNIFILAR

AUTOR	DATA	REV.	PRANCHA
Rogério Eduardo Moreira Menegueli	2026-11-06	03	01/08

ARQUIVO	UNIDADES	ESCALA	FOLHA	STATUS
01_diagrama_unifilar.dxf	mm	S/ESC.	A3	CONCEIT.