
DISTRIBUICAO E CIRCUITOS SERIE DOS AUXILIOS LUMINOSOS

Fonte BT, reguladores de corrente constante, circuitos e transformadores de isolamento

TOPOLOGIA DE CIRCUITOS SERIE E TRANSFORMADORES DE ISOLAMENTO

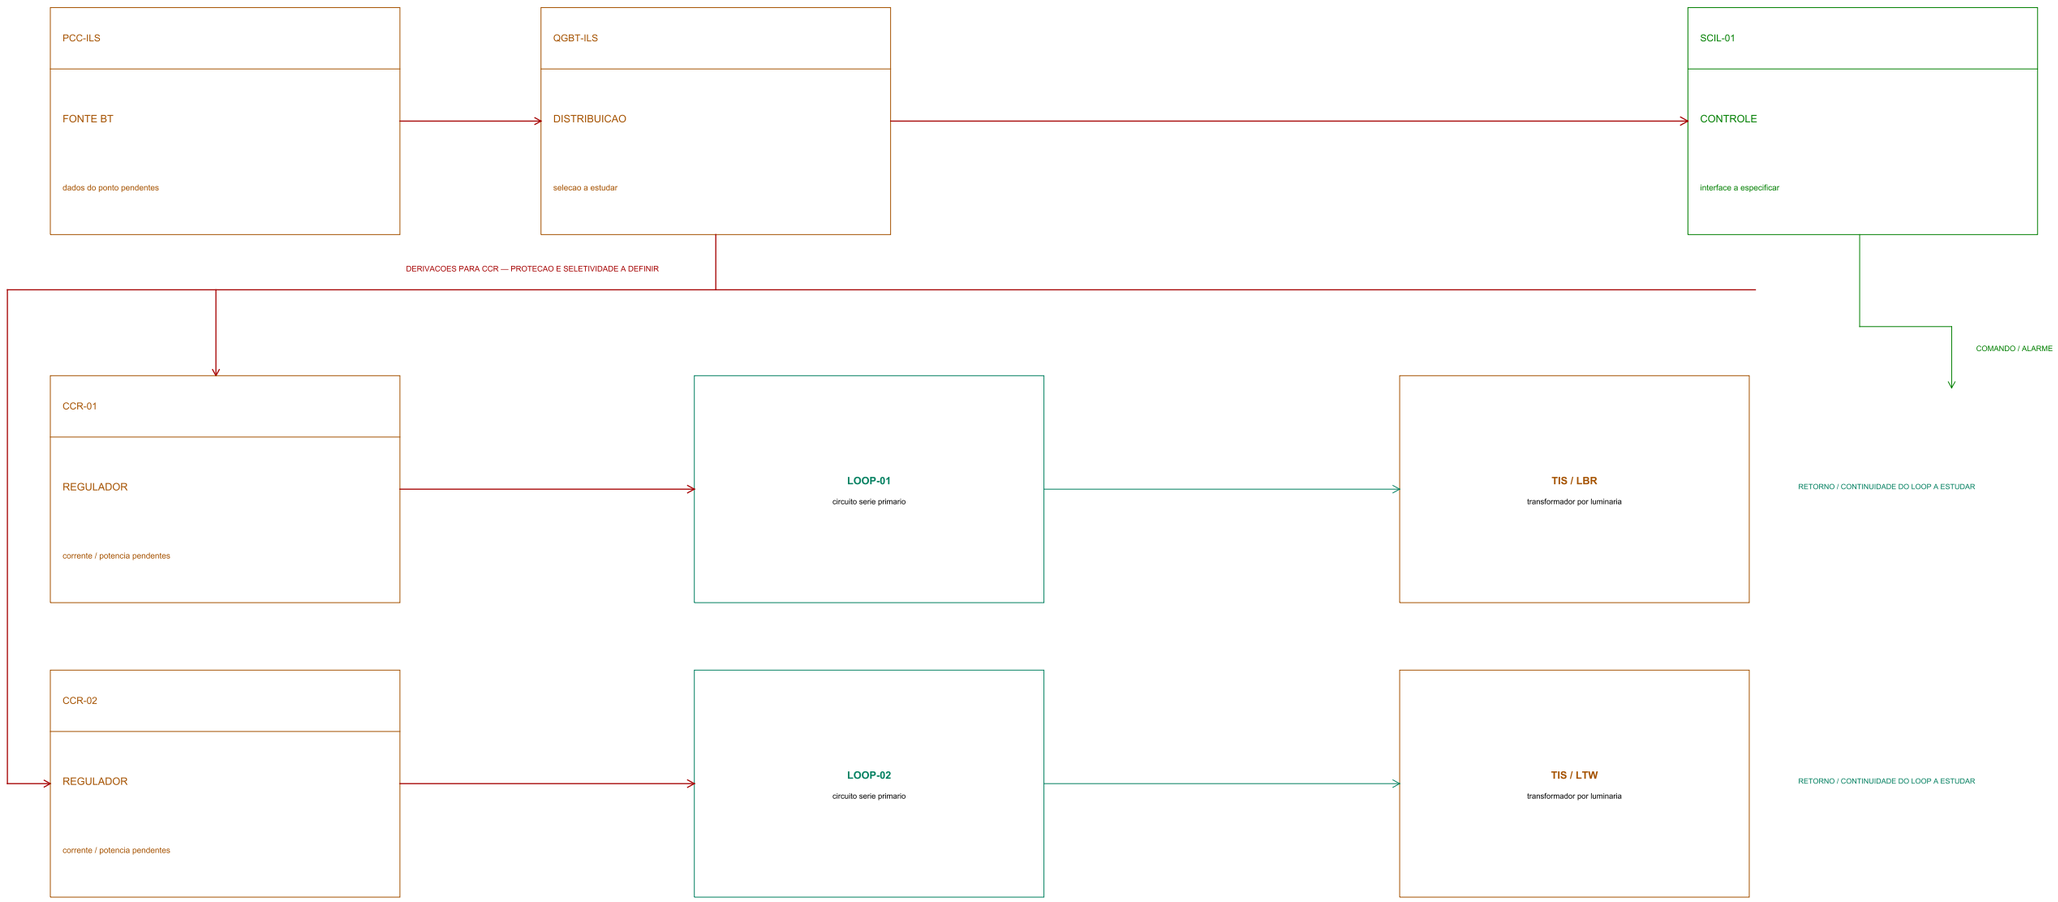

LEGENDA

PCC: ponto de conexao | QGBT: quadro geral | CCR: regulador de corrente constante | TIS: transformador de isolamento | LOOP: circuito serie

NOTAS DA PRANCHA

Topologia funcional; correntes, potencia, protecao, cabos e redundancia nao dimensionados.
Nao define tempo de comutacao, monitor de isolamento ou capacidade de contingencia.

AVISO OBRIGATORIO

Projeto acadêmico e conceitual. Não deve ser utilizado para fabricação, instalação ou execução de serviços sem revisão, dimensionamento e responsabilidade de profissional legalmente habilitado.

REV.	DATA	DESCRICAO	RESP.
00	2026-11-06	EMISSAO INICIAL	R.E.M.M.

PORTFOLIO DE
ENGENHARIA ELETRICA
BASE ACADEMICA REPRODUZIVEL

A3
PAISAGEM

TITULO

DISTRIBUICAO E CIRCUITOS SERIE DOS AUXILIOS LUMINOSOS

AUTOR	DATA	REV.	PRANCHA
Rogério Eduardo Moreira Menegueli	2026-11-06	00	02/03

ARQUIVO	UNIDADES	ESCALA	FOLHA	STATUS
02_unifilar_circuitos_serie_ccr.dxf	mm	S/ESC.	A3	CONCEIT.