
INTERLIGAÇÕES DE CAMPO

Interfaces do painel com rede, motor, emergência e automação

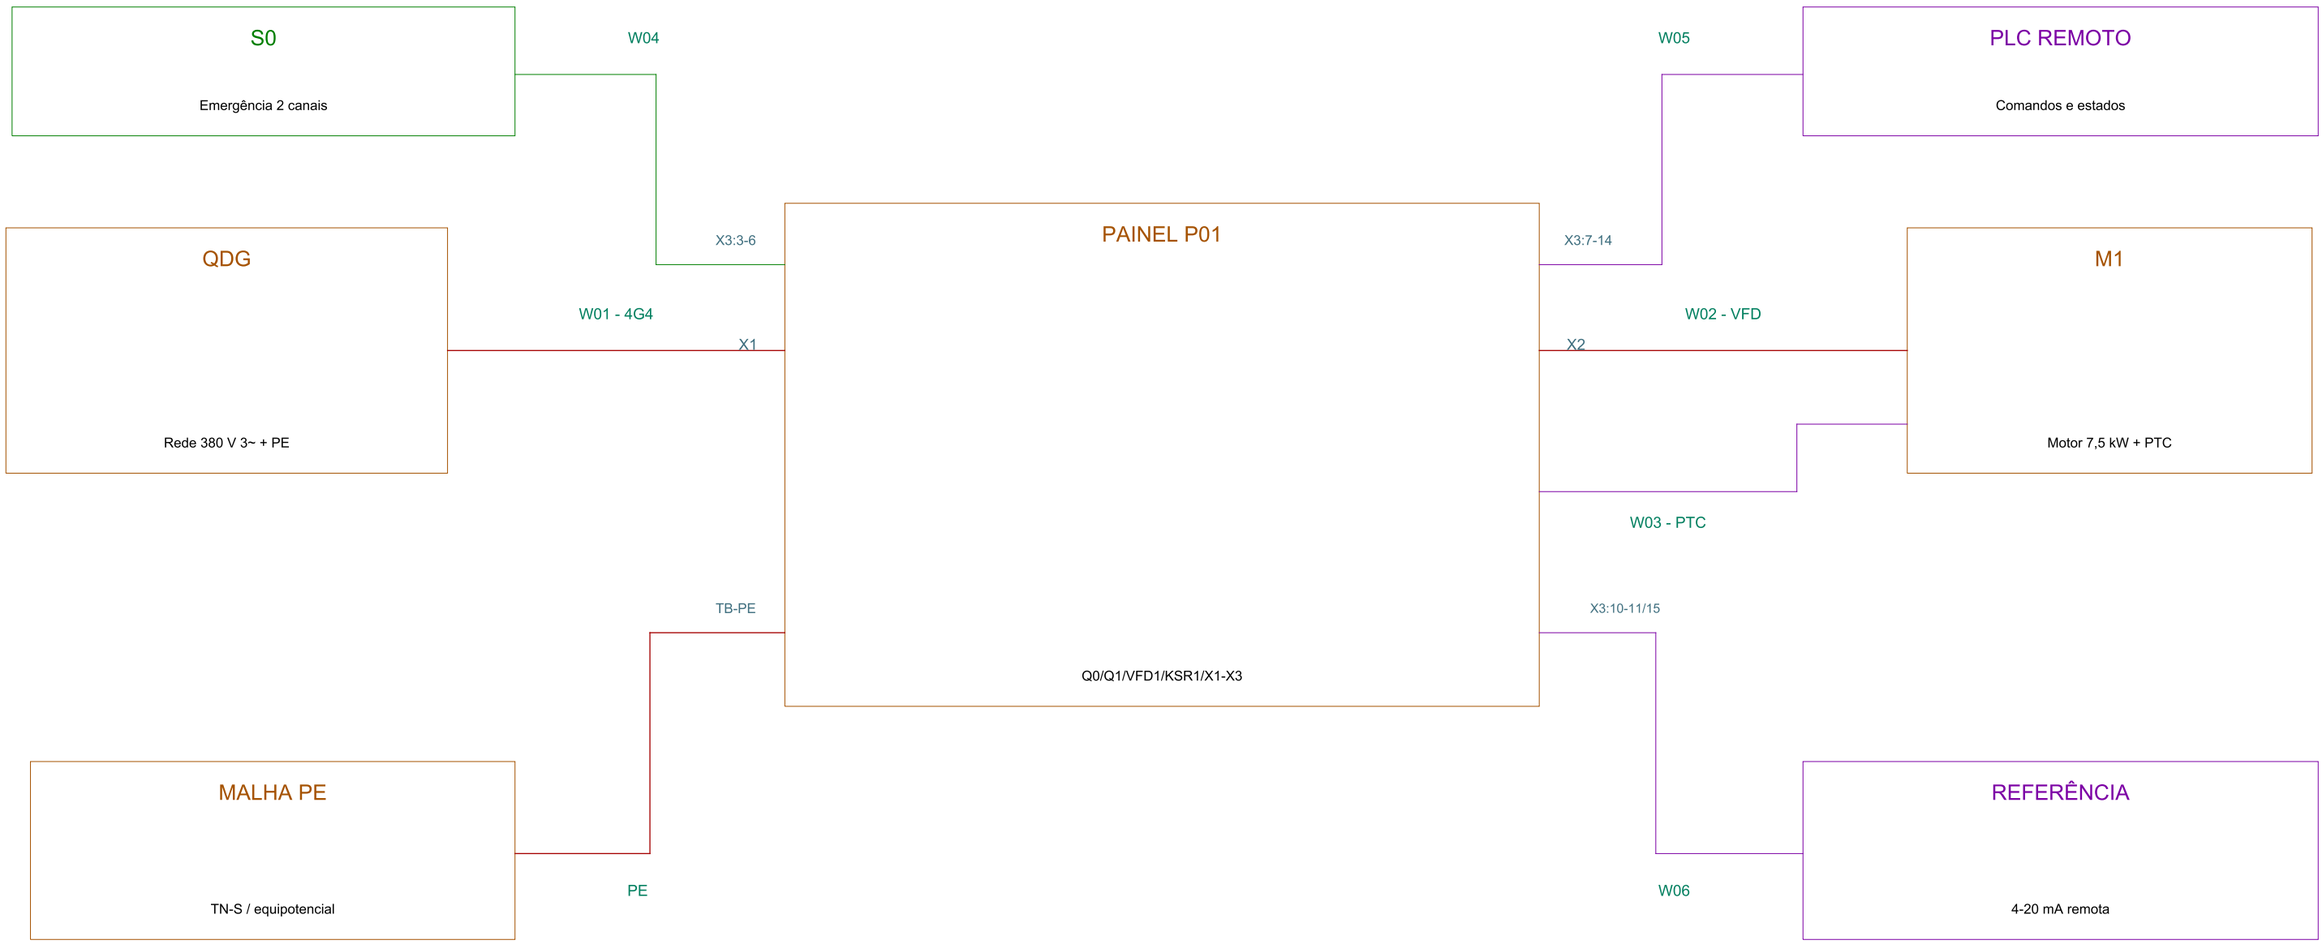

LEGENDA

W01/W02: potência | W03/W04/W05/W06: comando e instrumentação

NOTAS DA PRANCHA

Comprimentos são premissas para documentação e orçamento conceitual.
Rotas, segregação, queda de tensão e EMC dependem de levantamento em campo.

AVISO OBRIGATÓRIO

Projeto acadêmico e conceitual. Não deve ser utilizado para fabricação, instalação ou execução de serviços sem revisão, dimensionamento e responsabilidade de profissional legalmente habilitado.

REV.	DATA	DESCRIÇÃO	RESP.
02	2026-11-05	REVISAO VISUAL 02	R.E.M.M.

PORTFOLIO DE
ENGENHARIA ELETRICA
BASE ACADEMICA REPRODUZIVEL

A3
PAISAGEM

TITULO

INTERLIGAÇÕES DE CAMPO

AUTOR	DATA	REV.	PRANCHA
Rogério Eduardo Moreira Menegueli	2026-11-05	02	06/07

ARQUIVO	UNIDADES	ESCALA	FOLHA	STATUS
06_interligacoes_campo.dxf	mm	S/ESC.	A3	CONCEIT.