
ARQUITETURA ELETRICA DO DATA CENTER

Dois caminhos A/B ate a carga de TI; origem e independencia pendentes de estudo

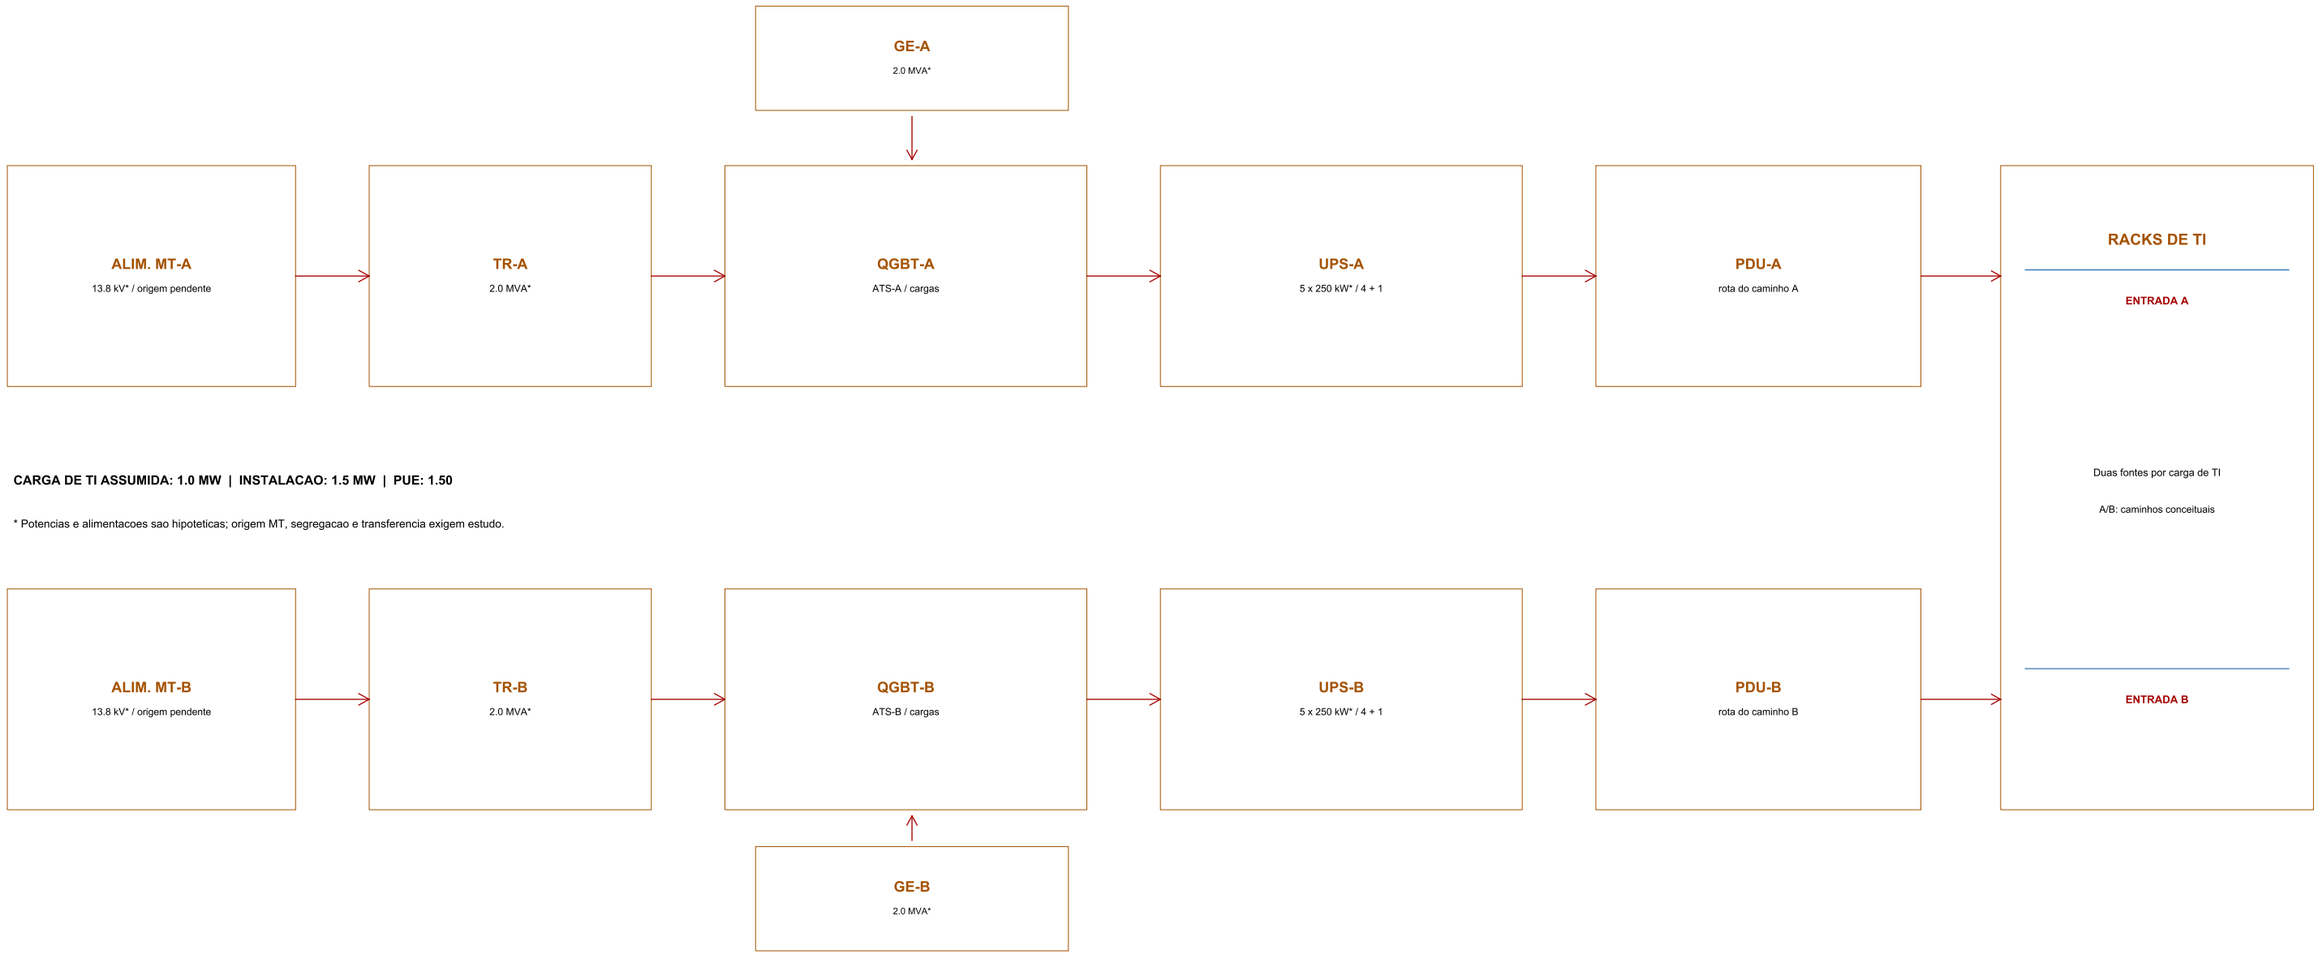

CARGA DE TI ASSUMIDA: 1.0 MW | INSTALACAO: 1.5 MW | PUE: 1.50

* Potencias e alimentacoes sao hipoteticas; origem MT, segregacao e transferencia exigem estudo.

LEGENDA

TR: transformador | QGBT: quadro BT | GE: gerador | ATS: transferencia | UPS: no-break | PDU: distribuicao aos racks | N+1: quatro modulos requeridos e um reserva

NOTAS DA PRANCHA

13,8 kV, 2,0 MVA, 1,0 MW TI e PUE 1,50 sao hipoteses didaticas.
A independencia de alimentacoes, geradores e caminhos fisicos nao foi demonstrada.

AVISO OBRIGATORIO

Projeto acadêmico e conceitual. Não deve ser utilizado para fabricação, instalação ou execução de serviços sem revisão, dimensionamento e responsabilidade de profissional legalmente habilitado.

REV.	DATA	DESCRICAO	RESP.
00	2026-11-06	EMISSAO INICIAL	R.E.M.M.

PORTFOLIO DE
ENGENHARIA ELETRICA
BASE ACADEMICA REPRODUZIVEL

A3
PAISAGEM

TITULO

ARQUITETURA ELETRICA DO DATA CENTER

AUTOR	DATA	REV.	PRANCHA
Rogério Eduardo Moreira Menegueli	2026-11-06	00	01/03

ARQUIVO	UNIDADES	ESCALA	FOLHA	STATUS
01_arquitetura_eletrica_ab.dxf	mm	S/ESC.	A3	CONCEIT.