
UNIFILAR GERAL DO COMPLEXO SIDERURGICO EAF

Rede 138 kV, subestacao 138/34,5 kV, forno 30 MVA e auxiliares

EQUIPAMENTO	POTENCIA	TENSAO	IMPEDANCIA
T1	45 MVA	138/34,5 kV	12,5%*
TF1	30 MVA	34,5/1,0 kV	10%*
SOMA CARGAS	28,0 MW	34,5 kV	fp 0,757

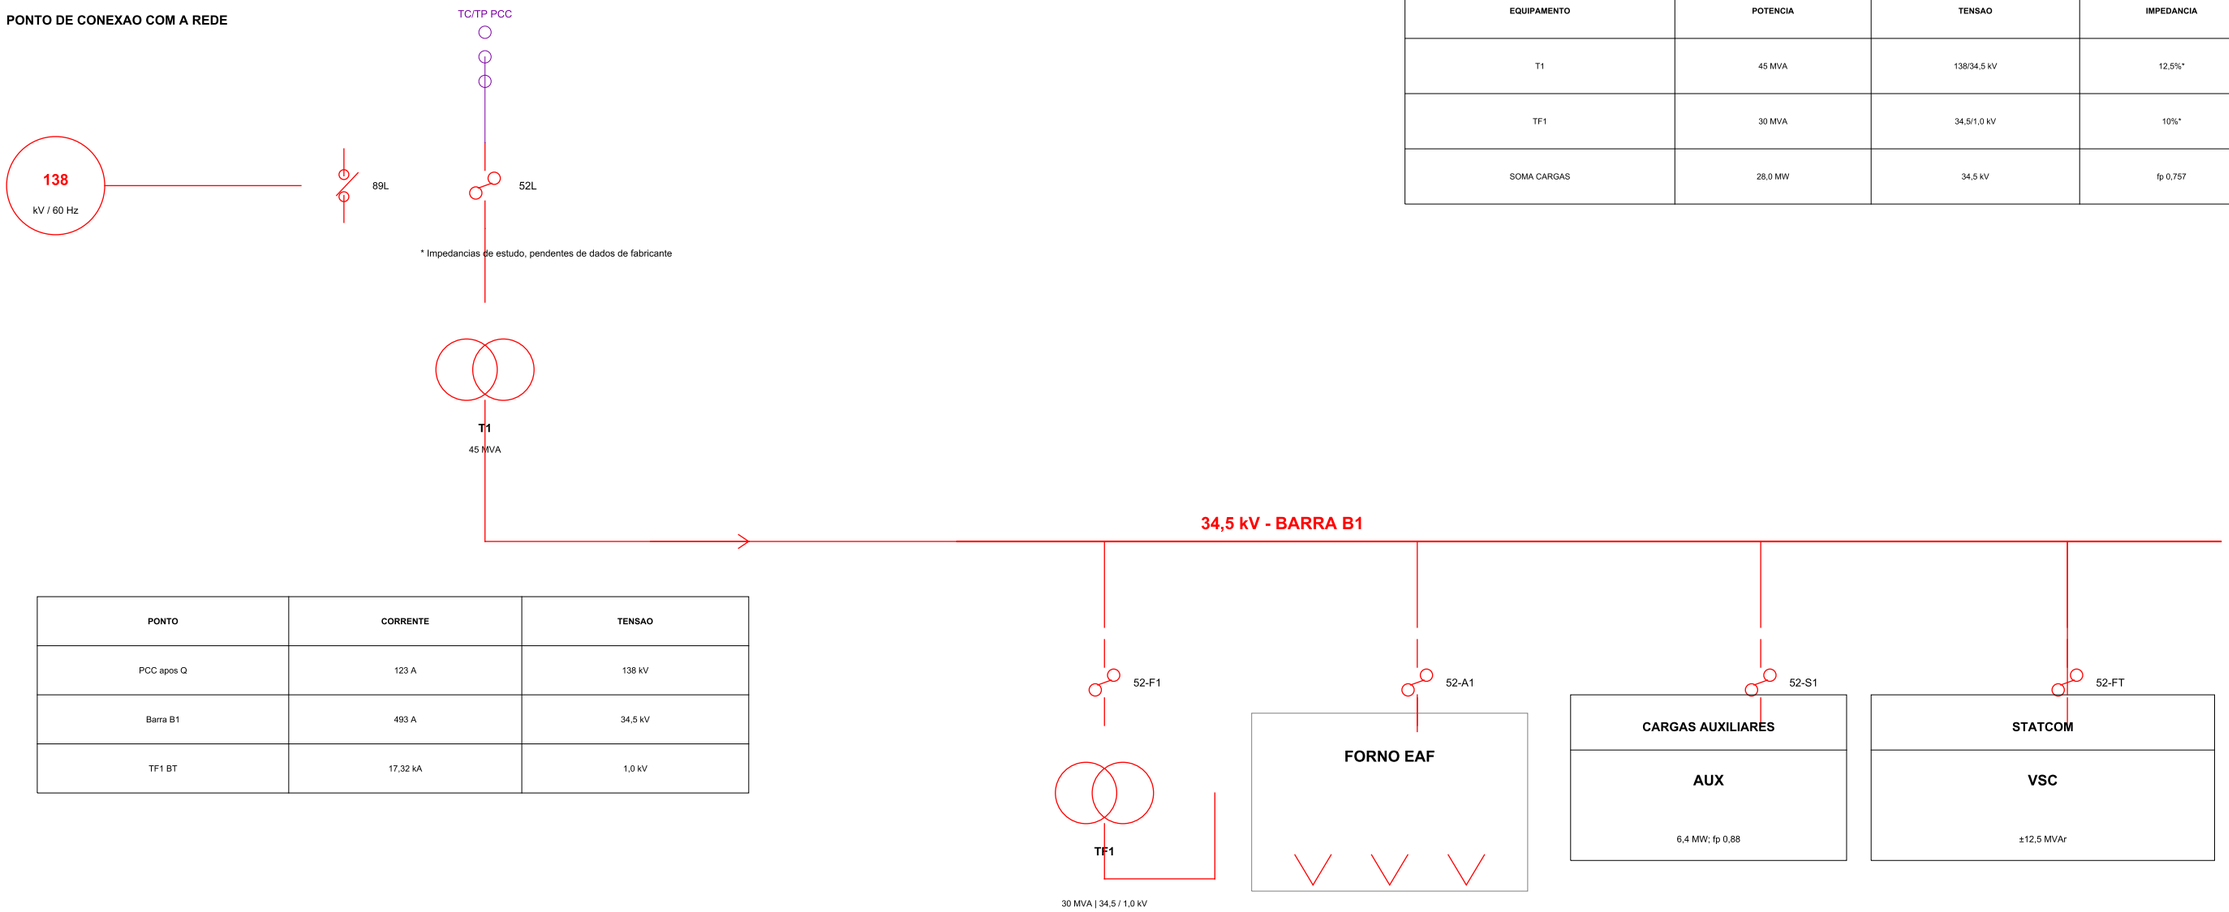

PONTO	CORRENTE	TENSAO
PCC apos Q	123 A	138 kV
Barra B1	493 A	34,5 kV
TF1 BT	17,32 kA	1,0 kV

LEGENDA

138 kV: entrada | T1: 45 MVA | TF1: 30 MVA | STATCOM: ±12,5 MVAr | F5/F7/HP: filtros

NOTAS DA PRANCHA

PCC no lado de 138 kV; barra industrial principal em 34,5 kV.
Transformador de forno de 30 MVA, secundario conceitual de 1,0 kV e derivacoes sob carga.
Compensacao dinamica e filtros conectados a barra de 34,5 kV.

AVISO OBRIGATORIO

Projeto acadêmico e conceitual. Não deve ser utilizado para fabricação, instalação ou execução de serviços sem revisão, dimensionamento e responsabilidade de profissional legalmente habilitado.

REV.	DATA	DESCRICAO	AUTOR
00	2026-11-09	EMISSAO INICIAL	R. MENEGUELI

PORTFOLIO DE
ENGENHARIA ELETRICA
BASE ACADEMICA REPRODUZIVEL

A3
PAISAGEM

TITULO

UNIFILAR GERAL DO COMPLEXO SIDERURGICO EAF

AUTOR	DATA	REV.	PRANCHA
Rogério Eduardo Moreira Menegueli	2026-11-09	00	01/10

ARQUIVO	UNIDADES	ESCALA	FOLHA	STATUS
01_diagrama_unifilar_geral.dxf	mm	S/ESC.	A3	CONCEIT.