
UNIFILAR DA USINA DE COGERACAO

Gerador 25 MW / 13,8 kV, transformador elevador e conexao em 138 kV

EQUIP.	S	TENSAO	CORRENTE	DADO
G1	32 MVA	13,8 kV	1.338 A	placa
T1	40 MVA	13,8/138	167 A AT	uk 12%*
Exportacao	22,8 MW	138 kV	100 A	fp ~0,95

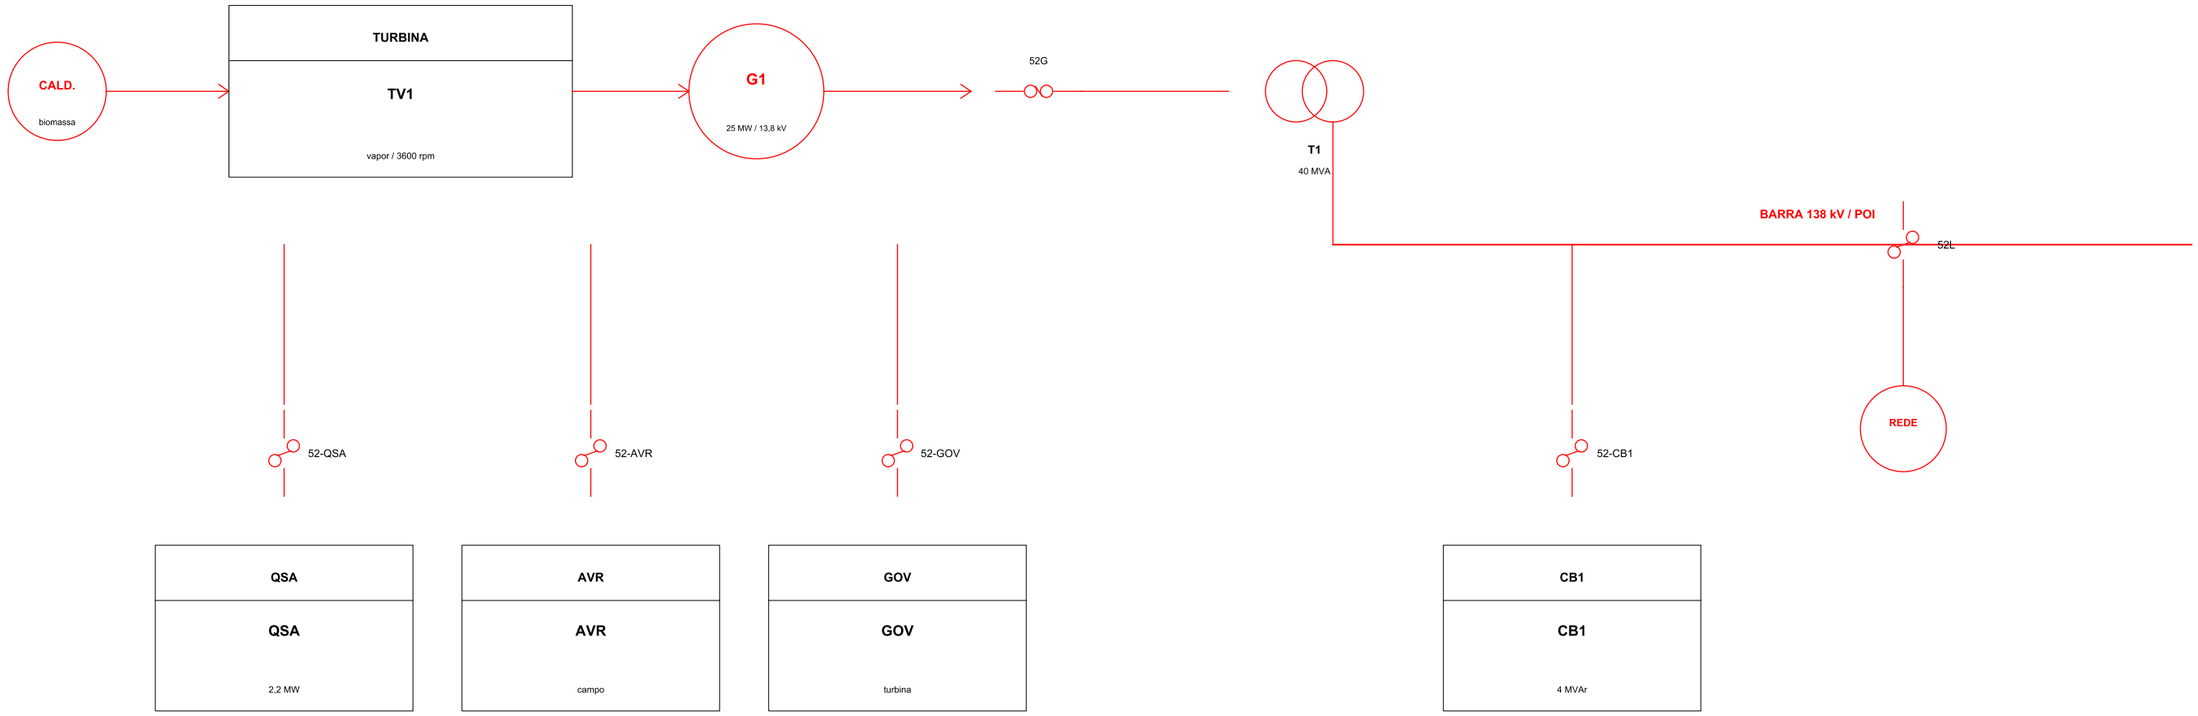

LEGENDA

G1: gerador 32 MVA | T1: 40 MVA, 13,8/138 kV | Qaux: auxiliares | POI: conexao

NOTAS DA PRANCHA

Geracao bruta de 25 MW; auxiliares estimados em 2,2 MW; exportacao liquida de 22,8 MW.
Transformador de 40 MVA; barra de geracao 13,8 kV e POI de 138 kV.

AVISO OBRIGATORIO

Projeto acadêmico e conceitual. Não deve ser utilizado para fabricação, instalação ou execução de serviços sem revisão, dimensionamento e responsabilidade de profissional legalmente habilitado.

REV.	DATA	DESCRICAO	AUTOR
00	2026-11-09	EMISSAO INICIAL	R. MENEGUELI

PORTFOLIO DE
ENGENHARIA ELETRICA
BASE ACADEMICA REPRODUZIVEL

A3
PAISAGEM

TITULO

UNIFILAR DA USINA DE COGERACAO

AUTOR	DATA	REV.	PRANCHA
Rogério Eduardo Moreira Menegueli	2026-11-09	00	01/10

ARQUIVO	UNIDADES	ESCALA	FOLHA	STATUS
01_diagrama_unifilar.dxf	mm	S/ESC.	A3	CONCEIT.