
# DIAGRAMA UNIFILAR

Entrada 380/220 V, QGBT-05, QDF-05, QDL-05 e QADM-05

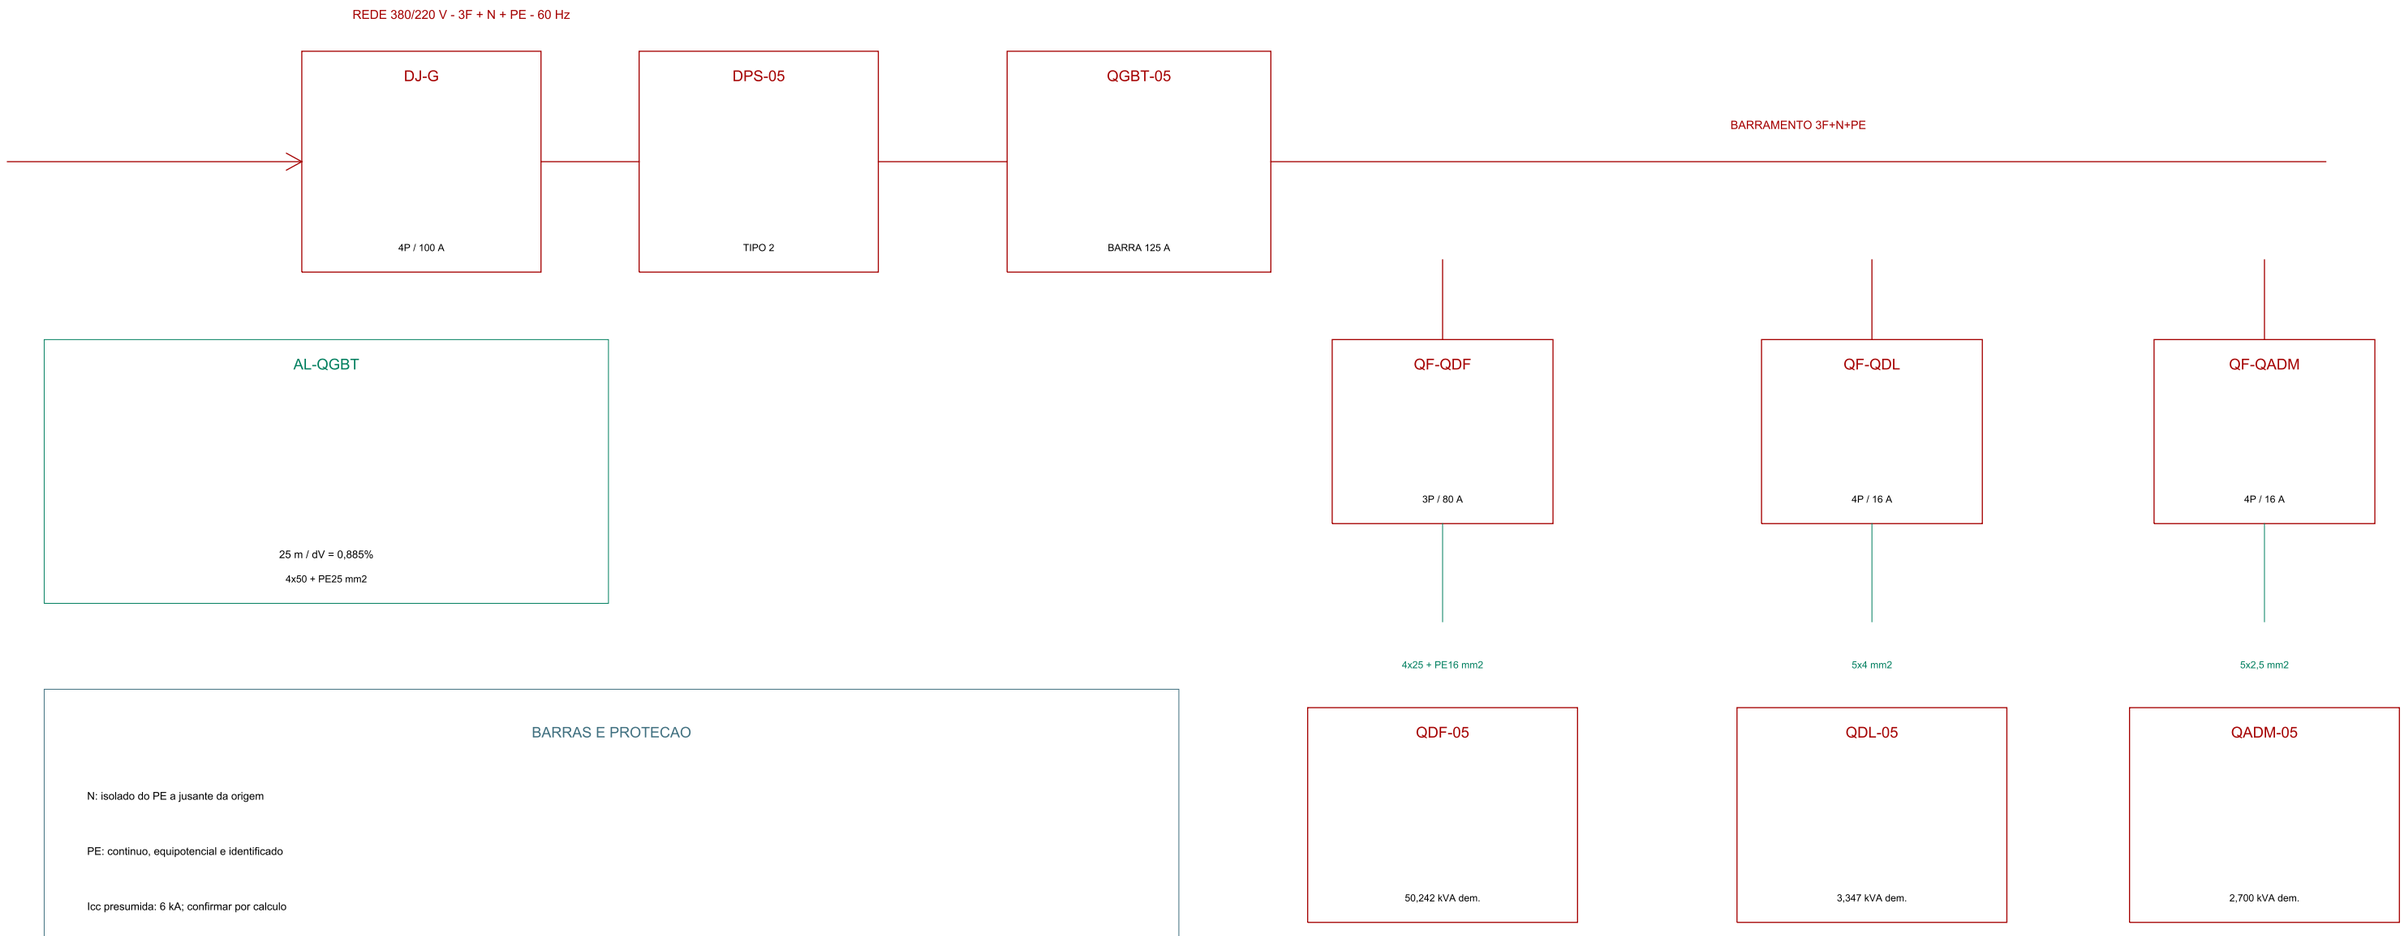


## LEGENDA

DJ: disjuntor | DPS: surto | DR: diferencial | N/PE: barras separadas

## NOTAS DA PRANCHA

Esquema TN-S conceitual a jusante do ponto de entrega. DR e DPS exigem coordenacao e selecao conforme rede, cargas, fabricante e estudo executivo.

## AVISO OBRIGATORIO

Projeto acadêmico e conceitual. Não deve ser utilizado para fabricação, instalação ou execução de serviços sem revisão, dimensionamento e responsabilidade de profissional legalmente habilitado.

| REV. | DATA | DESCRICAO | RESP. |
|---|---|---|---|
| 03 | 2026-11-05 | PLANO DE DADOS PARA COORDENACAO | R.E.M.M. |

**PORTFOLIO DE**
**ENGENHARIA ELETRICA**
BASE ACADEMICA REPRODUZIVEL

**A3**
PAISAGEM

TITULO

DIAGRAMA UNIFILAR

| AUTOR | DATA | REV. | PRANCHA |
|---|---|---|---|
| Rogério Eduardo Moreira Menegueli | 2026-11-05 | 03 | 05/09 |

| ARQUIVO | UNIDADES | ESCALA | FOLHA | STATUS |
|---|---|---|---|---|
| 05_diagrama_unifilar.dxf | mm | S/ESC. | A3 | CONCEIT. |