
ATERRAMENTO E EQUIPOTENCIALIZACAO

Malha conceitual da subestacao, estruturas, transformador e casa do forno

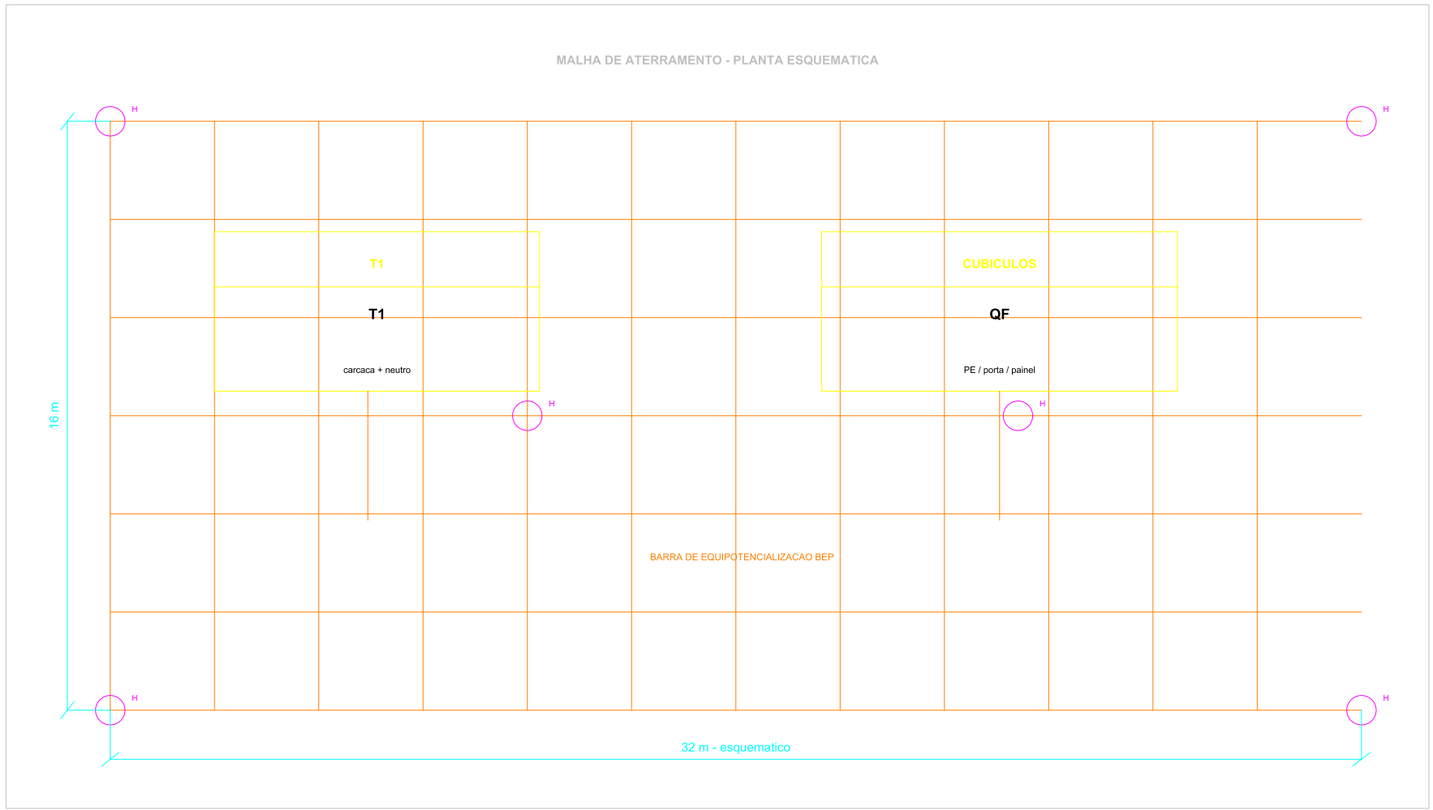

PONTOS A MEDIR

- ρ do solo por camada
- Icc e tempo de eliminacao
- toque e passo
- continuidade de ligacoes
- interferencia com tubulacoes

ITEM	PREMISSA
Condutor	Cu nu
Espacamento	8 m
Haste	3 m
Solo	100 Ω·m

LEGENDA

Cu: condutor de cobre | BEP: barra equipotencial | H: haste | ligacao a carcaças e estruturas

NOTAS DA PRANCHA

Malha indicativa; resistividade, corrente de falta, tempo de eliminacao e tensoes de toque/passo nao medidos.
Dimensionamento conforme estudo de solo e criterios vigentes da instalacao.

AVISO OBRIGATORIO

Projeto acadêmico e conceitual. Não deve ser utilizado para fabricação, instalação ou execução de serviços sem revisão, dimensionamento e responsabilidade de profissional legalmente habilitado.

REV.	DATA	DESCRICAO	AUTOR
00	2026-11-08	EMISSAO INICIAL	R. MENEGUELI

PORTFOLIO DE
ENGENHARIA ELETRICA
BASE ACADEMICA REPRODUZIVEL

A3
PAISAGEM

TITULO

ATERRAMENTO E EQUIPOTENCIALIZACAO

AUTOR	DATA	REV.	PRANCHA
Rogério Eduardo Moreira Menegueli	2026-11-08	00	09/10

ARQUIVO	UNIDADES	ESCALA	FOLHA	STATUS
09_aterramento_equipotencializacao.dxf	mm	S/ESC.	A3	CONCEIT.