
# UNIFILAR DA USINA DE COGERACAO

Gerador 25 MW / 13,8 kV, transformador elevador e conexao em 138 kV

| EQUIP. | S | TENSAO | CORRENTE | DADO |
|---|---|---|---|---|
| G1 | 32 MVA | 13,8 kV | 1.338 A | placa |
| T1 | 40 MVA | 13,8/138 | 167 A AT | uk 12%* |
| Exportacao | 22,8 MW | 138 kV | 100 A | fp ~0,95 |

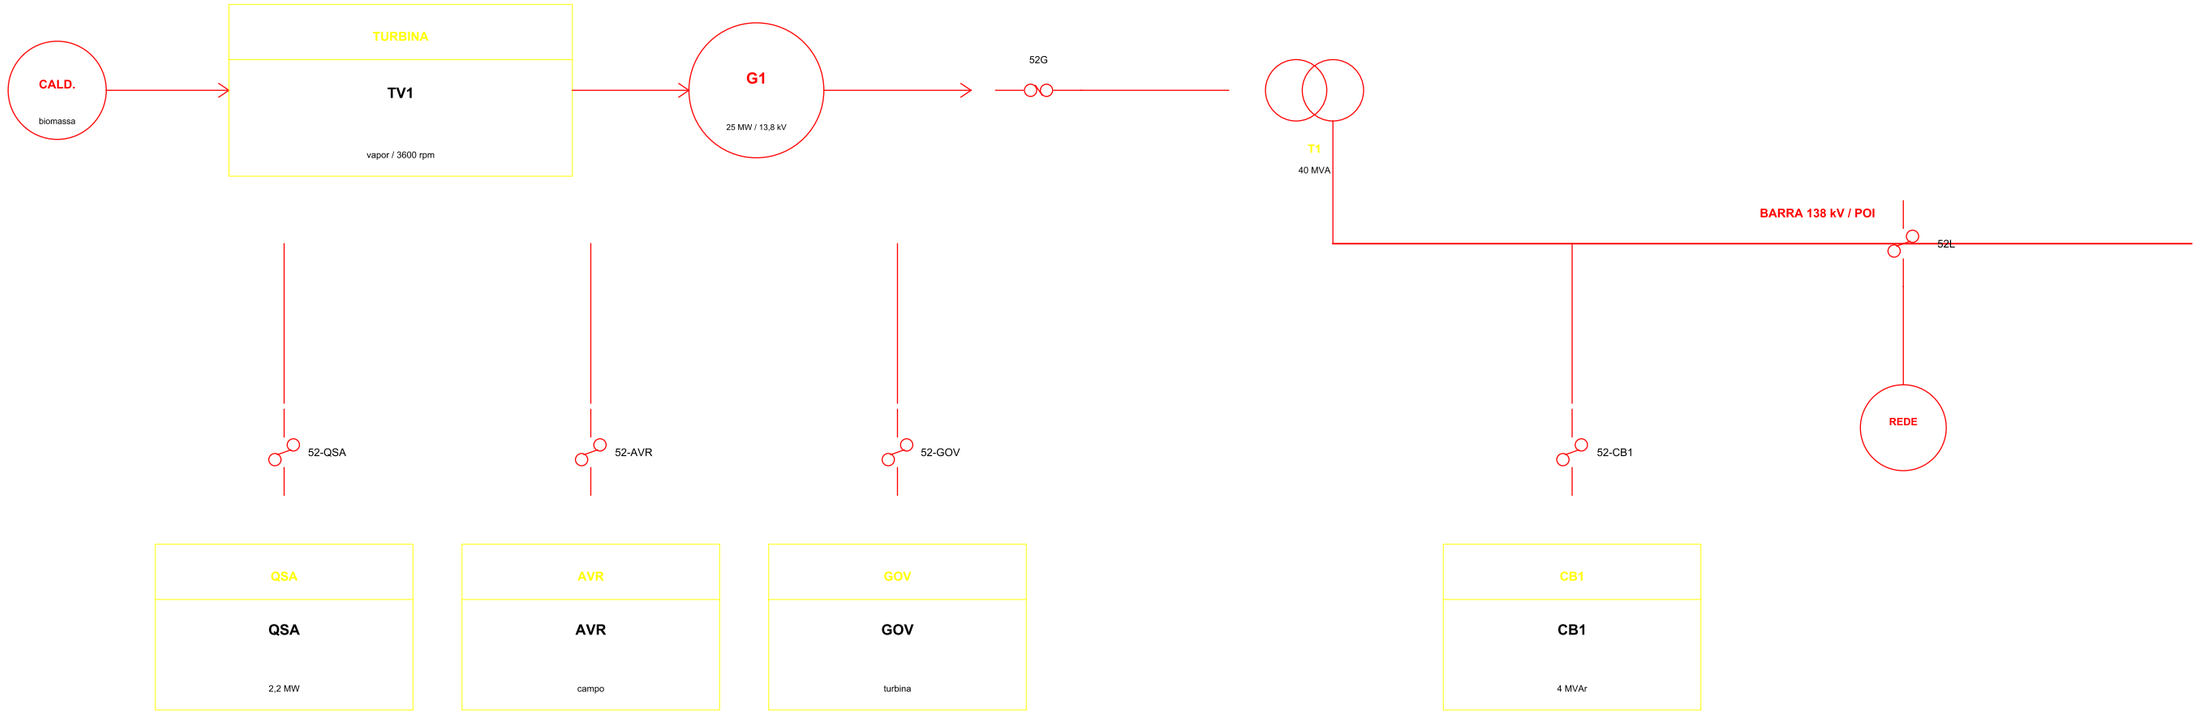


## LEGENDA

G1: gerador 32 MVA | T1: 40 MVA, 13,8/138 kV | Qaux: auxiliares | POI: conexao

## NOTAS DA PRANCHA

Geracao bruta de 25 MW; auxiliares estimados em 2,2 MW; exportacao liquida de 22,8 MW.
Transformador de 40 MVA; barra de geracao 13,8 kV e POI de 138 kV.

## AVISO OBRIGATORIO

Projeto acadêmico e conceitual. Não deve ser utilizado para fabricação, instalação ou execução de serviços sem revisão, dimensionamento e responsabilidade de profissional legalmente habilitado.

| REV. | DATA | DESCRICAO | AUTOR |
|---|---|---|---|
| 00 | 2026-11-08 | EMISSAO INICIAL | R. MENEGUELI |

**PORTFOLIO DE**
**ENGENHARIA ELETRICA**
BASE ACADEMICA REPRODUZIVEL

**A3**
PAISAGEM

TITULO

UNIFILAR DA USINA DE COGERACAO

| AUTOR | DATA | REV. | PRANCHA |
|---|---|---|---|
| Rogério Eduardo Moreira Menegueli | 2026-11-08 | 00 | 01/10 |

| ARQUIVO | UNIDADES | ESCALA | FOLHA | STATUS |
|---|---|---|---|---|
| 01_diagrama_unifilar.dxf | mm | S/ESC. | A3 | CONCEIT. |