
TRANSFORMADOR ELEVADOR E CONEXAO A REDE

Transformador 13,8/138 kV, bays de geracao e de linha

ITEM	S	LADO 13,8	LADO 138	uk*
T1	40 MVA	13,8 kV	138 kV	12%
In	-	1,673 kA	167 A	-
Ramo	13,8 kV	TC/TP	138 kV	-+

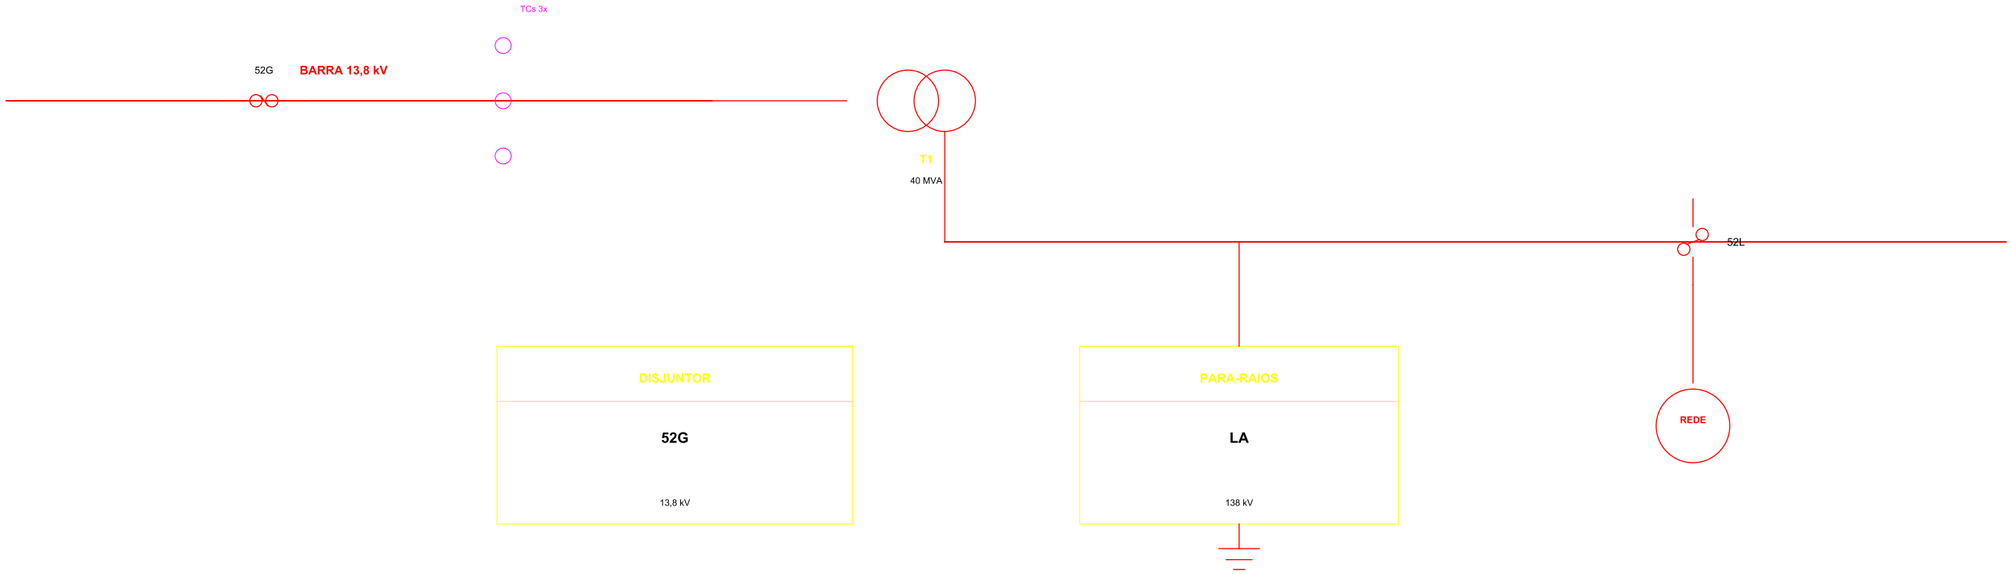

TCs e TPs: relacao/precisao a definir; uk assumido para estudos

LEGENDA

T1: elevador | QG/QP: disjuntores | TC/TP: medicao | LA: para-raios

NOTAS DA PRANCHA

Transformador 40 MVA com impedancia de 12% assumida.
Protecao, aterramento do neutro, isolamento e coordenacao dependem do arranjo real.

AVISO OBRIGATORIO

Projeto acadêmico e conceitual. Não deve ser utilizado para fabricação, instalação ou execução de serviços sem revisão, dimensionamento e responsabilidade de profissional legalmente habilitado.

REV.	DATA	DESCRICAO	AUTOR
00	2026-11-08	EMISSAO INICIAL	R. MENEGUELI

PORTFOLIO DE
ENGENHARIA ELETRICA
BASE ACADEMICA REPRODUZIVEL

A3
PAISAGEM

TITULO

TRANSFORMADOR ELEVADOR E CONEXAO A REDE

AUTOR	DATA	REV.	PRANCHA
Rogério Eduardo Moreira Menegueli	2026-11-08	00	04/10

ARQUIVO	UNIDADES	ESCALA	FOLHA	STATUS
04_transformador_conexao_rede.dxf	mm	S/ESC.	A3	CONCEIT.