
# ALIMENTAÇÃO 24 Vcc

Distribuição protegida da fonte aos circuitos de automação

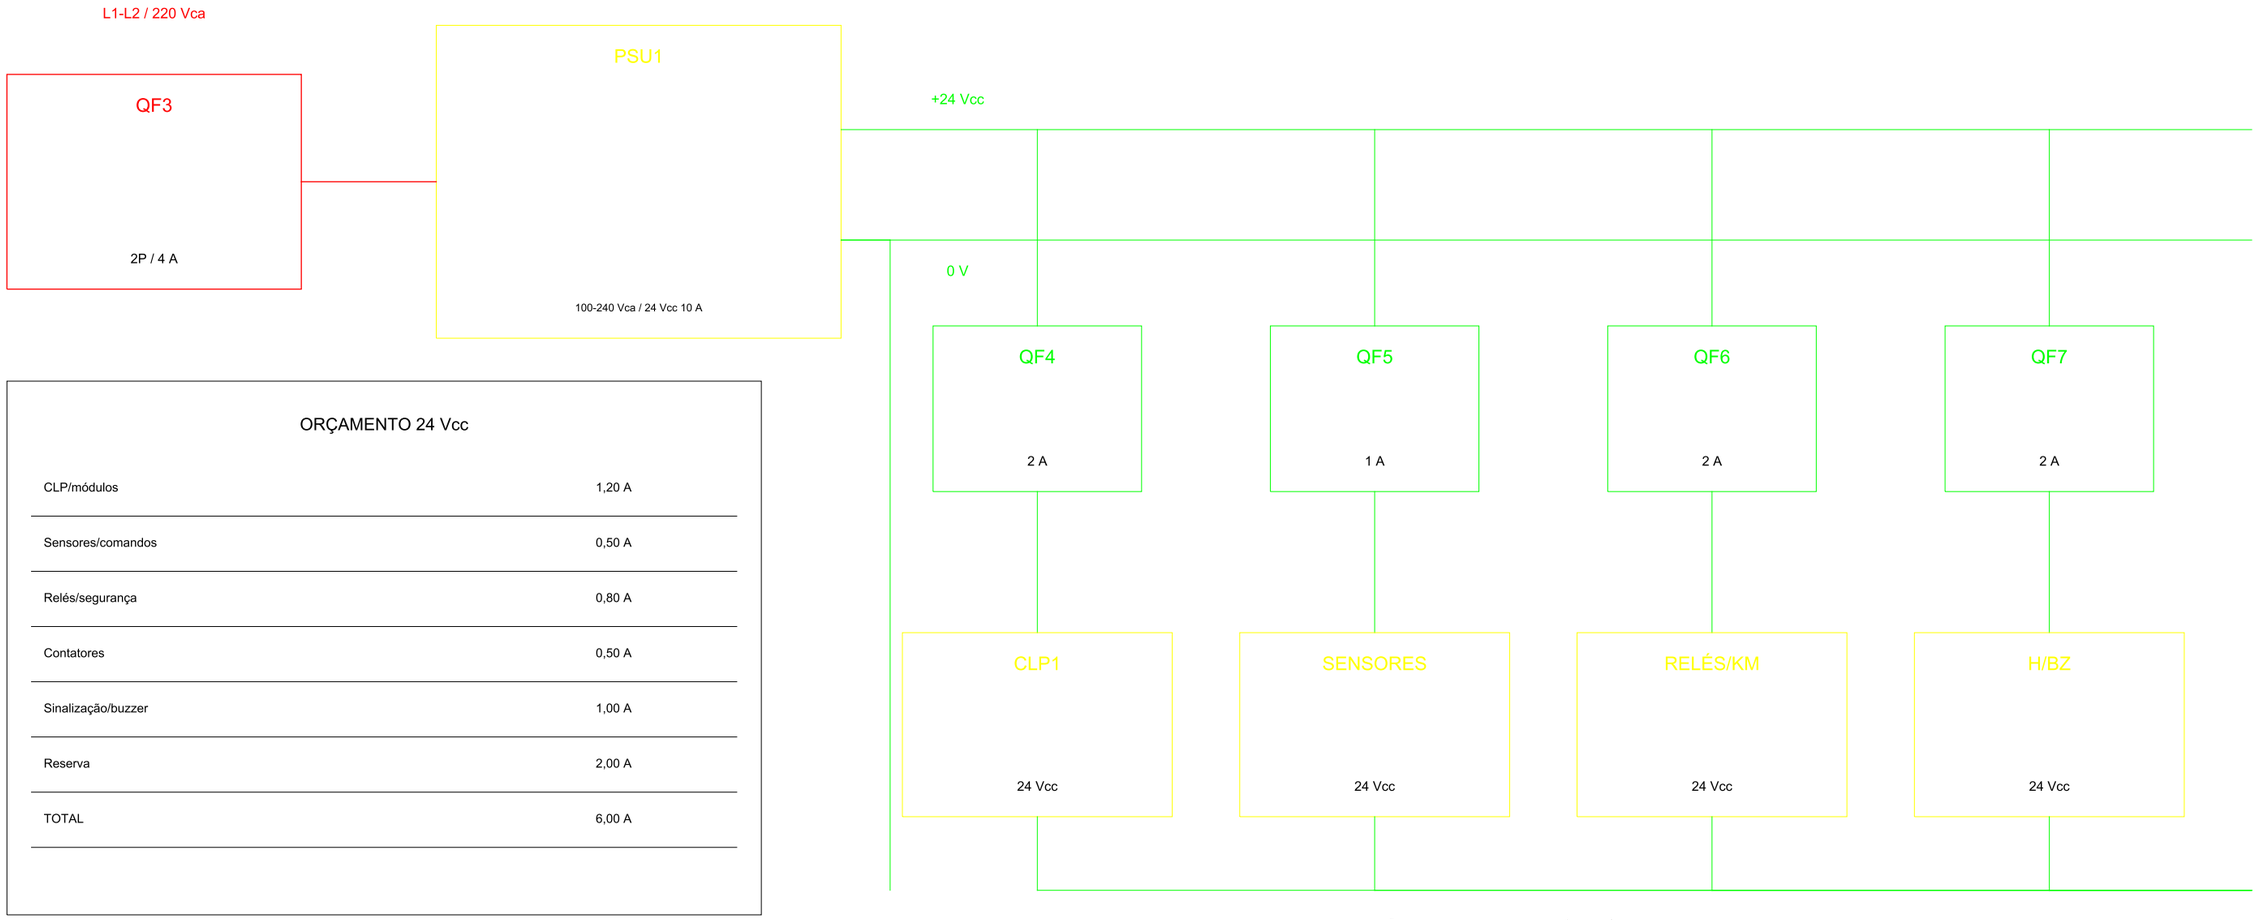


DISTRIBUIÇÃO RADIAL; 0 V COM REFERÊNCIA ÚNICA CONFORME HARDWARE

### ORÇAMENTO 24 Vcc

| | |
|---|---|
| CLP/módulos | 1,20 A |
| Sensores/comandos | 0,50 A |
| Relés/segurança | 0,80 A |
| Contatores | 0,50 A |
| Sinalização/buzzer | 1,00 A |
| Reserva | 2,00 A |
| TOTAL | 6,00 A |

### LEGENDA

+24V/0V: comando | QF4: CLP | QF5: sensores | QF6: relés | QF7: sinalização

### NOTAS DA PRANCHA

PSU1: 10 A; carga considerada: 6 A; reserva conceitual: 4 A.
Confirmar corrente de energização, temperatura, seletividade e PELV no projeto real.

### AVISO OBRIGATÓRIO

Projeto acadêmico e conceitual. Não deve ser utilizado para fabricação, instalação ou execução de serviços sem revisão, dimensionamento e responsabilidade de profissional legalmente habilitado.

| REV. | DATA | DESCRIÇÃO | RESP. |
|---|---|---|---|
| 00 | 2026-09-06 | EMISSÃO INICIAL DO PROJETO 03 | R.E.M.M. |

**PORTFOLIO DE**
**ENGENHARIA ELETRICA**
BASE ACADEMICA REPRODUZIVEL

**A3**
PAISAGEM

TITULO

ALIMENTAÇÃO 24 Vcc

| AUTOR | DATA | REV. | PRANCHA |
|---|---|---|---|
| Rogério Eduardo Moreira Menegueli | 2026-09-06 | 00 | 02/08 |

| ARQUIVO | UNIDADES | ESCALA | FOLHA | STATUS |
|---|---|---|---|---|
| 02_alimentacao_24v.dxf | mm | S/ESC. | A3 | CONCEIT. |