
DIAGRAMA DE INTERLIGAÇÃO

Cabos, bornes, canais, blindagem e equipotencialização

PAINEL PI-101

CABO	CAMPO	COND.	BORNE	+24V	CANAL	0V	SHIELD	REMOTA	FUNÇÃO
C-101	TT-101	1x2 SH	X3:01/02	X2:01	AI0	X2:02	BE-101	RIO-201	4-20 mA
C-102	PT-102	1x2 SH	X3:03/04	X2:01	AI1	X2:02	BE-101	RIO-201	4-20 mA
C-103	FT-103	1x2 SH	X3:05/06	X2:01	AI0	X2:02	BE-101	RIO-202	4-20 mA
C-104	LT-104	1x2 SH	X3:07/08	X2:01	AI1	X2:02	BE-101	RIO-202	4-20 mA
C-105	LSH-105	1x2	X4:01/02	X2:01	DI0	X2:02	—	RIO-201	digital
C-106	PSL-106	1x2	X4:03/04	X2:01	DI0	X2:02	—	RIO-202	digital

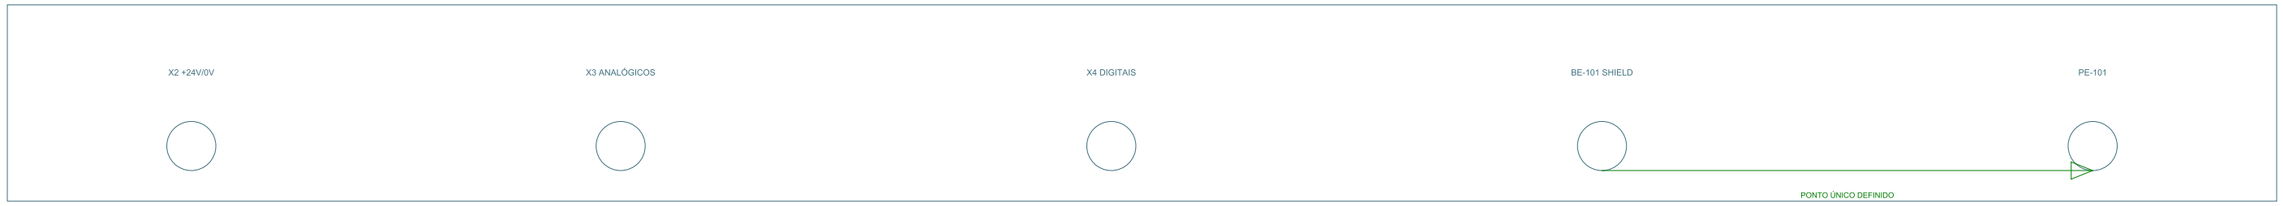

CAMPO: blindagem isolada

PAINEL: blindagem em BE-101

PE-101: proteção e equipotencialização

0 V é retorno funcional; PE não conduz corrente operacional; SHIELD não substitui PE.

LEGENDA

X2: 24 Vcc | X3: analógicos | X4: digitais | BE-101: barra de blindagem | PE-101: proteção

NOTAS DA PRANCHA

Blindagem analógica aterrada apenas em BE-101, no painel; extremidade de campo isolada.
PE, 0 V funcional e blindagem têm funções distintas e não devem ser confundidos.

AVISO OBRIGATÓRIO

Projeto acadêmico e conceitual. Não deve ser utilizado para fabricação, instalação ou execução de serviços sem revisão, dimensionamento e responsabilidade de profissional legalmente habilitado.

REV.	DATA	DESCRIÇÃO	RESP.
03	2026-11-05	REVISAO DE SINAIS	R.E.M.M.

PORTFOLIO DE
ENGENHARIA ELETRICA
BASE ACADEMICA REPRODUZIVEL

A3
PAISAGEM

TITULO

DIAGRAMA DE INTERLIGAÇÃO

AUTOR	DATA	REV.	PRANCHA
Rogério Eduardo Moreira Menegueli	2026-11-05	03	03/08

ARQUIVO	UNIDADES	ESCALA	FOLHA	STATUS
03_diagrama_interligacao.dxf	mm	S/ESC.	A3	CONCEIT.