
PLANTA DE INSTALACAO E DETALHES DO GMG

Arranjo fisico da sala do gerador, atenuacao acustica, escape e contencao

PLANTA BAIXA - SALA DO GERADOR

Dimensoes Internas: 6,50 x 4,00 m (Escala 1:50)

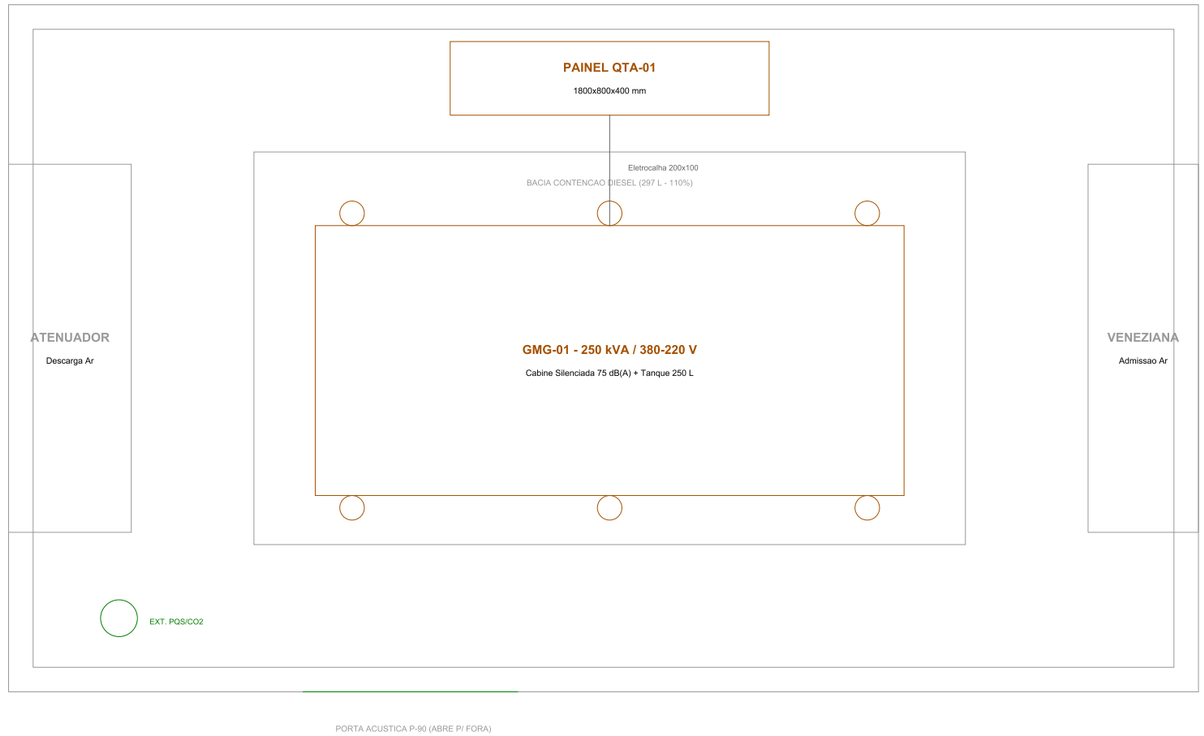

ESCAPE HOSPITALAR E REQUISITOS

Atenuacao Acustica e Gases

1. JUNTA EXPANSAO FLEXIVEL INOX

Absorcao de vibracao na saida do turbo

2. SILENCIOSO HOSPITALAR DN 4"

Atenuacao de 32 dB(A) c/ dreno condensado

3. TUBULACAO ISOLADA LA DE ROCHA

Espessura 50 mm + protecao aluminio

- Nivel sonoro externo <= 75 dB(A) a 1,5m (NBR 10151).
- Vazao de ar do radiador: 5,2 m3/s (18.720 m3/h).
- Autonomia do tanque 250 L: 5,7 h (100%) / 7,6 h (75%).
- Aterramento da carcaca e neutro em Cu 120 mm2 ao BEP.

LEGENDA

GMG-01: 250 kVA | ESC-01: silencioso hospitalar | TQ-01: tanque 250L | VIB: amortecedores

NOTAS DA PRANCHA

Base de concreto isolada com 6 amortecedores elastomericos antivibratorios.
Cabine silenciada 75 dB(A) com venezianas de admissao e descarga atenuadas.
Tanque integrado de 250 L sobre bacia de contencao estanque para 297 L (110%).

AVISO OBRIGATORIO

Projeto acadêmico e conceitual. Não deve ser utilizado para fabricação, instalação ou execução de serviços sem revisão, dimensionamento e responsabilidade de profissional legalmente habilitado.

REV.	DATA	DESCRICAO	RESP.
03	2026-11-05	REVISAO TECNICA E GRAFICA	R.E.M.M.

PORTFOLIO DE
ENGENHARIA ELETRICA
BASE ACADEMICA REPRODUZIVEL

A3
PAISAGEM

TITULO

PLANTA DE INSTALACAO E DETALHES DO GMG

AUTOR	DATA	REV.	PRANCHA
Rogério Eduardo Moreira Menegueli	2026-11-05	03	06/09

ARQUIVO	UNIDADES	ESCALA	FOLHA	STATUS
06_planta_instalacao_gmg.dxf	mm	1:50	A3	CONCEIT.