
DISTRIBUICAO DE ILUMINACAO

Iluminacao LED por setores, circuitos C09-C13 e QDL-05

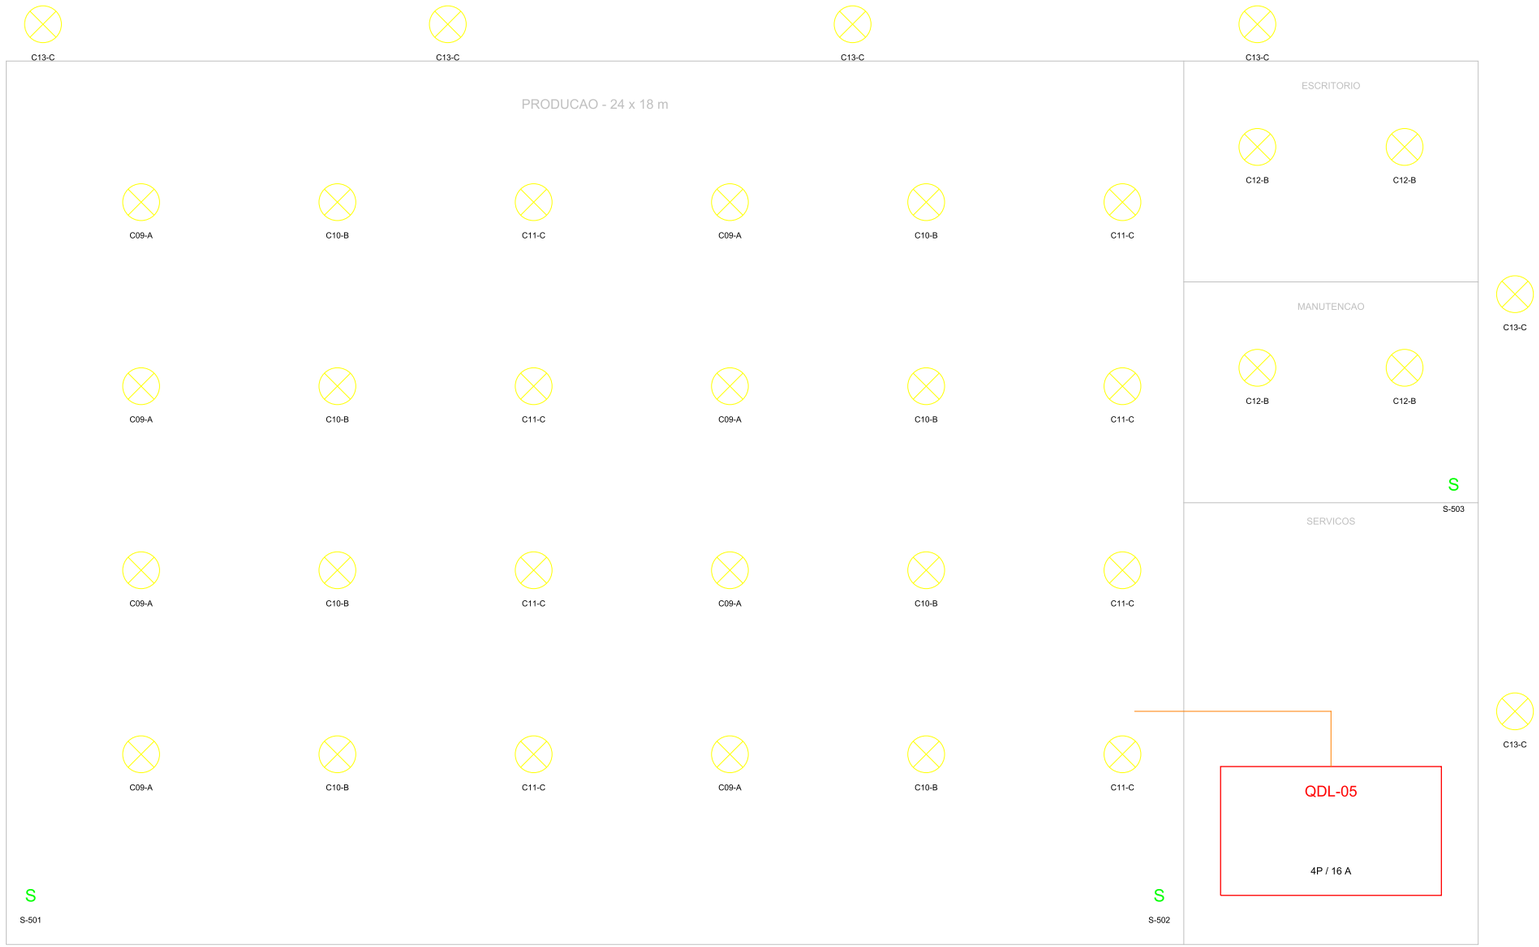

RESUMO DE ILUMINACAO

C09-A: 8 x 100 W = 800 W

C10-B: 8 x 100 W = 800 W

C11-C: 8 x 100 W = 800 W

C12-B: 12 x 40 W = 480 W

C13-C: 6 x 50 W = 300 W

Total ativo: 3,180 kW

Fator de potencia: 0,95

Total aparente: 3,347 kVA

Comando: local por setores

Emergencia: estudo especifico

LEGENDA

Circulo com X: luminaria | S: comando | Verde: comando | C09/C10/C11: galpao

NOTAS DA PRANCHA

Arranjo luminotecnico e potencias sao hipoteses. Confirmar iluminancia, uniformidade, ofuscamento, emergencia e influencias externas.

AVISO OBRIGATORIO

Projeto acadêmico e conceitual. Não deve ser utilizado para fabricação, instalação ou execução de serviços sem revisão, dimensionamento e responsabilidade de profissional legalmente habilitado.

REV.	DATA	DESCRICAO	RESP.
00	2026-09-09	EMISSAO INICIAL DO PROJETO 05	R.E.M.M.

PORTFOLIO DE
ENGENHARIA ELETRICA
BASE ACADEMICA REPRODUZIVEL

A3
PAISAGEM

TITULO

DISTRIBUICAO DE ILUMINACAO

AUTOR	DATA	REV.	PRANCHA
Rogério Eduardo Moreira Menegueli	2026-09-09	00	03/07

ARQUIVO	UNIDADES	ESCALA	FOLHA	STATUS
03_distribuicao_iluminacao.dxf	mm	1:125	A3	CONCEIT.