
ELETROCALHAS E ROTAS

Rotas E-501/E-502/E-503, alimentadores e descidas de circuitos

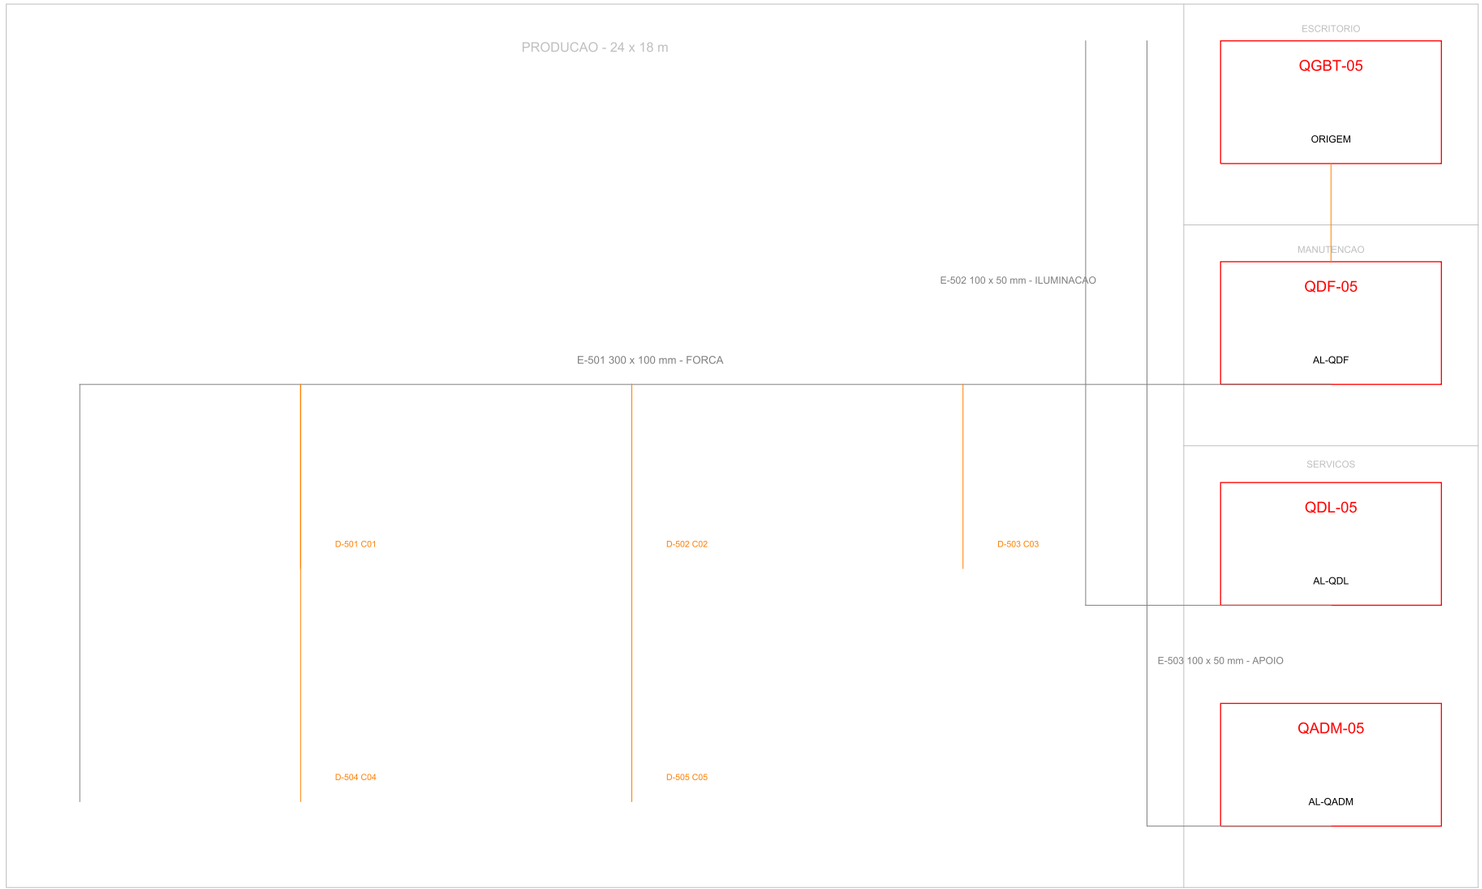

ALIMENTADORES

AL-QGBT: 25 m / 4x50+PE25 mm2

DJ-G: 4P 100 A / dV 0,885%

AL-QDF: 18 m / 4x25+PE16 mm2

DJ-QDF: 3P 80 A / dV 0,562%

AL-QDL: 20 m / 5x4 mm2

DJ-QDL: 4P 16 A / dV 0,626%

AL-QADM: 16 m / 5x2,5 mm2

DJ-QADM: 4P 16 A / dV 0,536%

PE acompanha todas as rotas

Segregar potencia e comunicacao

LEGENDA

Cinza grosso: eletrocalha | Laranja: cabo | D: descida | PE: protecao

NOTAS DA PRANCHA

Ocupacao, suportacao, raio de curvatura, segregacao e EMC nao foram verificados. Comprimentos sao premissas rastreadas na lista de cabos.

AVISO OBRIGATORIO

Projeto acadêmico e conceitual. Não deve ser utilizado para fabricação, instalação ou execução de serviços sem revisão, dimensionamento e responsabilidade de profissional legalmente habilitado.

REV.	DATA	DESCRICAO	RESP.
00	2026-09-09	EMISSAO INICIAL DO PROJETO 05	R.E.M.M.

PORTFOLIO DE
ENGENHARIA ELETRICA
BASE ACADEMICA REPRODUZIVEL

A3
PAISAGEM

TITULO

ELETROCALHAS E ROTAS

AUTOR	DATA	REV.	PRANCHA
Rogério Eduardo Moreira Menegueli	2026-09-09	00	04/07

ARQUIVO	UNIDADES	ESCALA	FOLHA	STATUS
04_eletrocalhas_rotas.dxf	mm	1:125	A3	CONCEIT.