
# PLANTA DE INSTALACAO E DETALHES DO GMG

Arranjo fisico da sala do gerador, atenuacao acustica, escape e contencao

### PLANTA BAIXA - SALA DO GERADOR

Dimensoes Internas: 6,50 x 4,00 m (Escala 1:50)

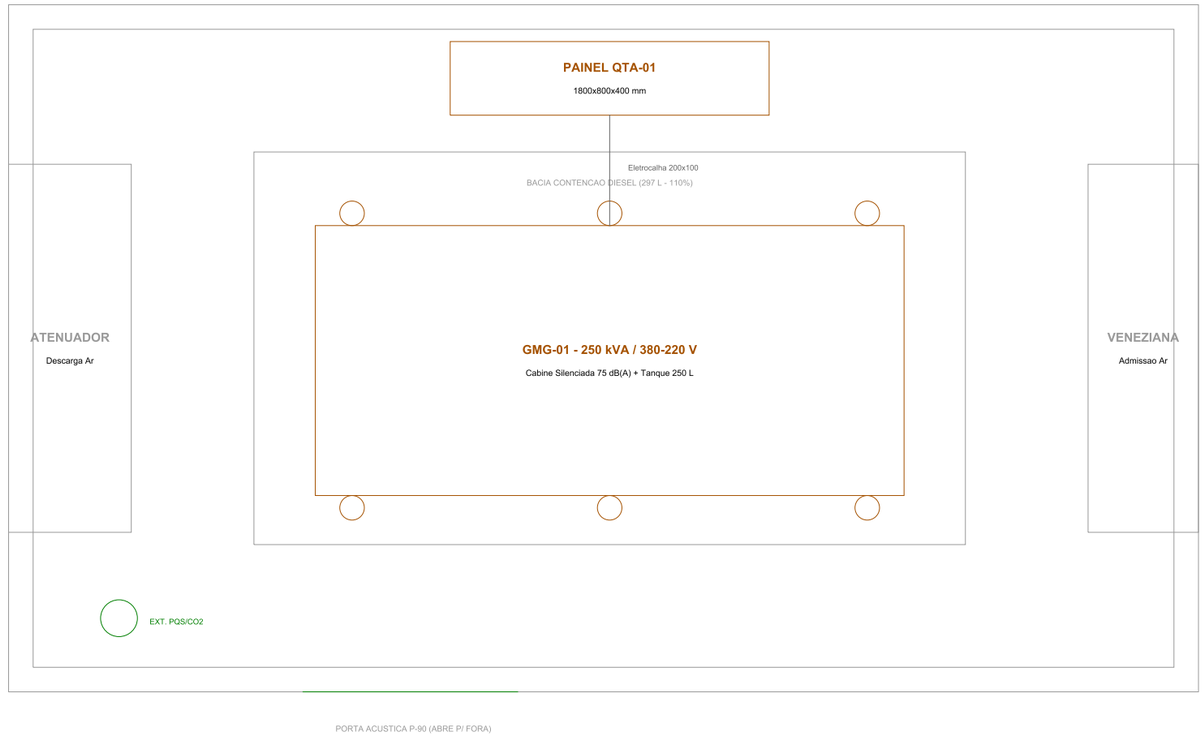


### ESCAPE HOSPITALAR E REQUISITOS

Atenuacao Acustica e Gases

**1. JUNTA EXPANSAO FLEXIVEL INOX**

Absorcao de vibracao na saida do turbo

**2. SILENCIOSO HOSPITALAR DN 4"**

Atenuacao de 32 dB(A) c/ dreno condensado

**3. TUBULACAO ISOLADA LA DE ROCHA**

Espessura 50 mm + protecao aluminio

- Nivel sonoro externo <= 75 dB(A) a 1,5m (NBR 10151).
- Vazao de ar do radiador: 5,2 m3/s (18.720 m3/h).
- Autonomia do tanque 250 L: 5,7 h (100%) / 7,6 h (75%).
- Aterramento da carcaca e neutro em Cu 120 mm2 ao BEP.

## LEGENDA

GMG-01: 250 kVA | ESC-01: silencioso hospitalar | TQ-01: tanque 250L | VIB: amortecedores

## NOTAS DA PRANCHA

Base de concreto isolada com 6 amortecedores elastomericos antivibratorios.
Cabine silenciada 75 dB(A) com venezianas de admissao e descarga atenuadas.
Tanque integrado de 250 L sobre bacia de contencao estanque para 297 L (110%).

## AVISO OBRIGATORIO

Projeto acadêmico e conceitual. Não deve ser utilizado para fabricação, instalação ou execução de serviços sem revisão, dimensionamento e responsabilidade de profissional legalmente habilitado.

| REV. | DATA | DESCRICAO | RESP. |
|---|---|---|---|
| 02 | 2026-11-05 | REVISAO TECNICA E GRAFICA | R.E.M.M. |

**PORTFOLIO DE**
**ENGENHARIA ELETRICA**
BASE ACADEMICA REPRODUZIVEL

**A3**
PAISAGEM

TITULO

PLANTA DE INSTALACAO E DETALHES DO GMG

| AUTOR | DATA | REV. | PRANCHA |
|---|---|---|---|
| Rogério Eduardo Moreira Menegueli | 2026-11-05 | 02 | 06/08 |

| ARQUIVO | UNIDADES | ESCALA | FOLHA | STATUS |
|---|---|---|---|---|
| 06_planta_instalacao_gmg.dxf | mm | 1:50 | A3 | CONCEIT. |