
REDE DE COMUNICAÇÃO

CAN-PT linear, gateway de diagnóstico e matriz de mensagens

CAN-PT 500 kbit/s - BARRAMENTO LINEAR PROPOSTO

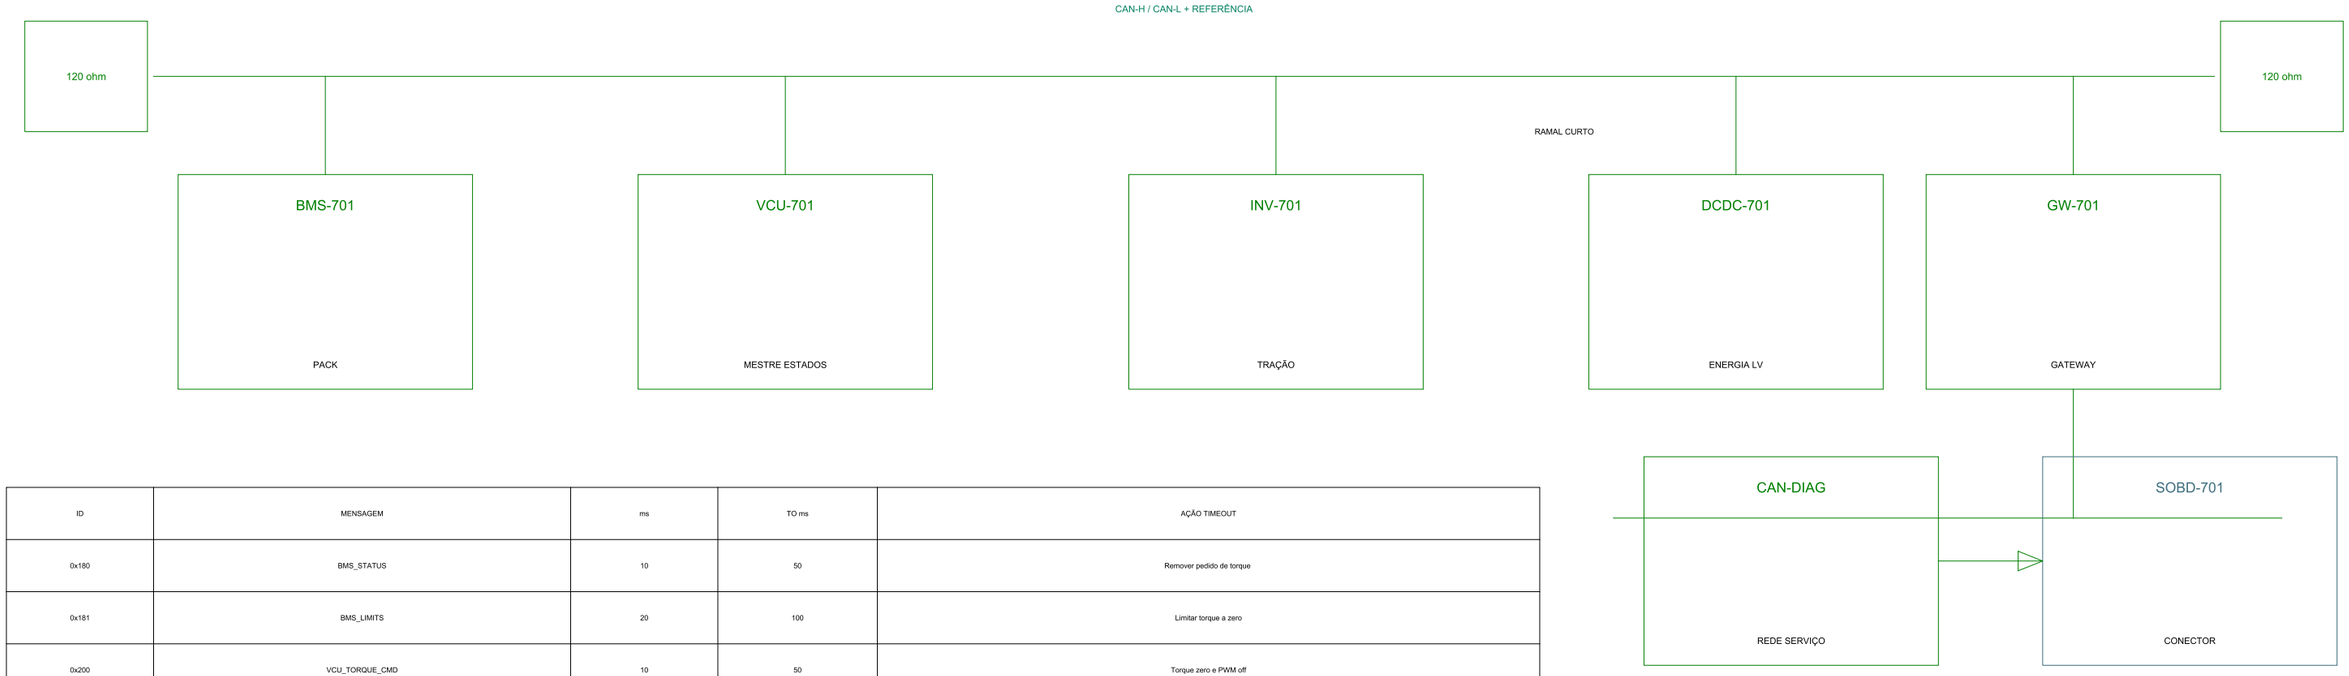

ID	MENSAGEM	ms	TO ms	AÇÃO TIMEOUT
0x180	BMS_STATUS	10	50	Remover pedido de torque
0x181	BMS_LIMITS	20	100	Limitar torque a zero
0x200	VCU_TORQUE_CMD	10	50	Torque zero e PWM off
0x201	INV_STATUS	10	50	Torque zero e abrir HV co
0x210	DCDC_STATUS	100	500	Alerta e estratégia de en

IDs, períodos e ações são PROPOSTAS; validar carga de barramento, prioridades, E2E e diagnóstico.

LEGENDA

RT: 120 ohm | CAN-H/L: par diferencial | GW: gateway | SOBD: diagnóstico

NOTAS DA PRANCHA

IDs, períodos e timeouts são premissas de arquitetura, não software validado.
O backbone requer duas terminações e ramais curtos, sujeitos a projeto EMC.

AVISO OBRIGATORIO

Projeto acadêmico e conceitual. Não deve ser utilizado para fabricação, instalação ou execução de serviços sem revisão, dimensionamento e responsabilidade de profissional legalmente habilitado.

REV.	DATA	DESCRICAO	RESP.
04	2026-11-06	SEQ PRE-CARGA 04	R.E.M.M.

PORTFOLIO DE
ENGENHARIA ELETRICA
BASE ACADEMICA REPRODUZIVEL

A3
PAISAGEM

TITULO

REDE DE COMUNICAÇÃO

AUTOR	DATA	REV.	PRANCHA
Rogério Eduardo Moreira Menegueli	2026-11-06	04	07/11

ARQUIVO	UNIDADES	ESCALA	FOLHA	STATUS
07_rede_comunicacao.dxf	mm	S/ESC.	A3	CONCEIT.