
FLUXOGRAMA DO PROCESSO

Enchimento de TK-101 por P-101; origem a montante não especificada

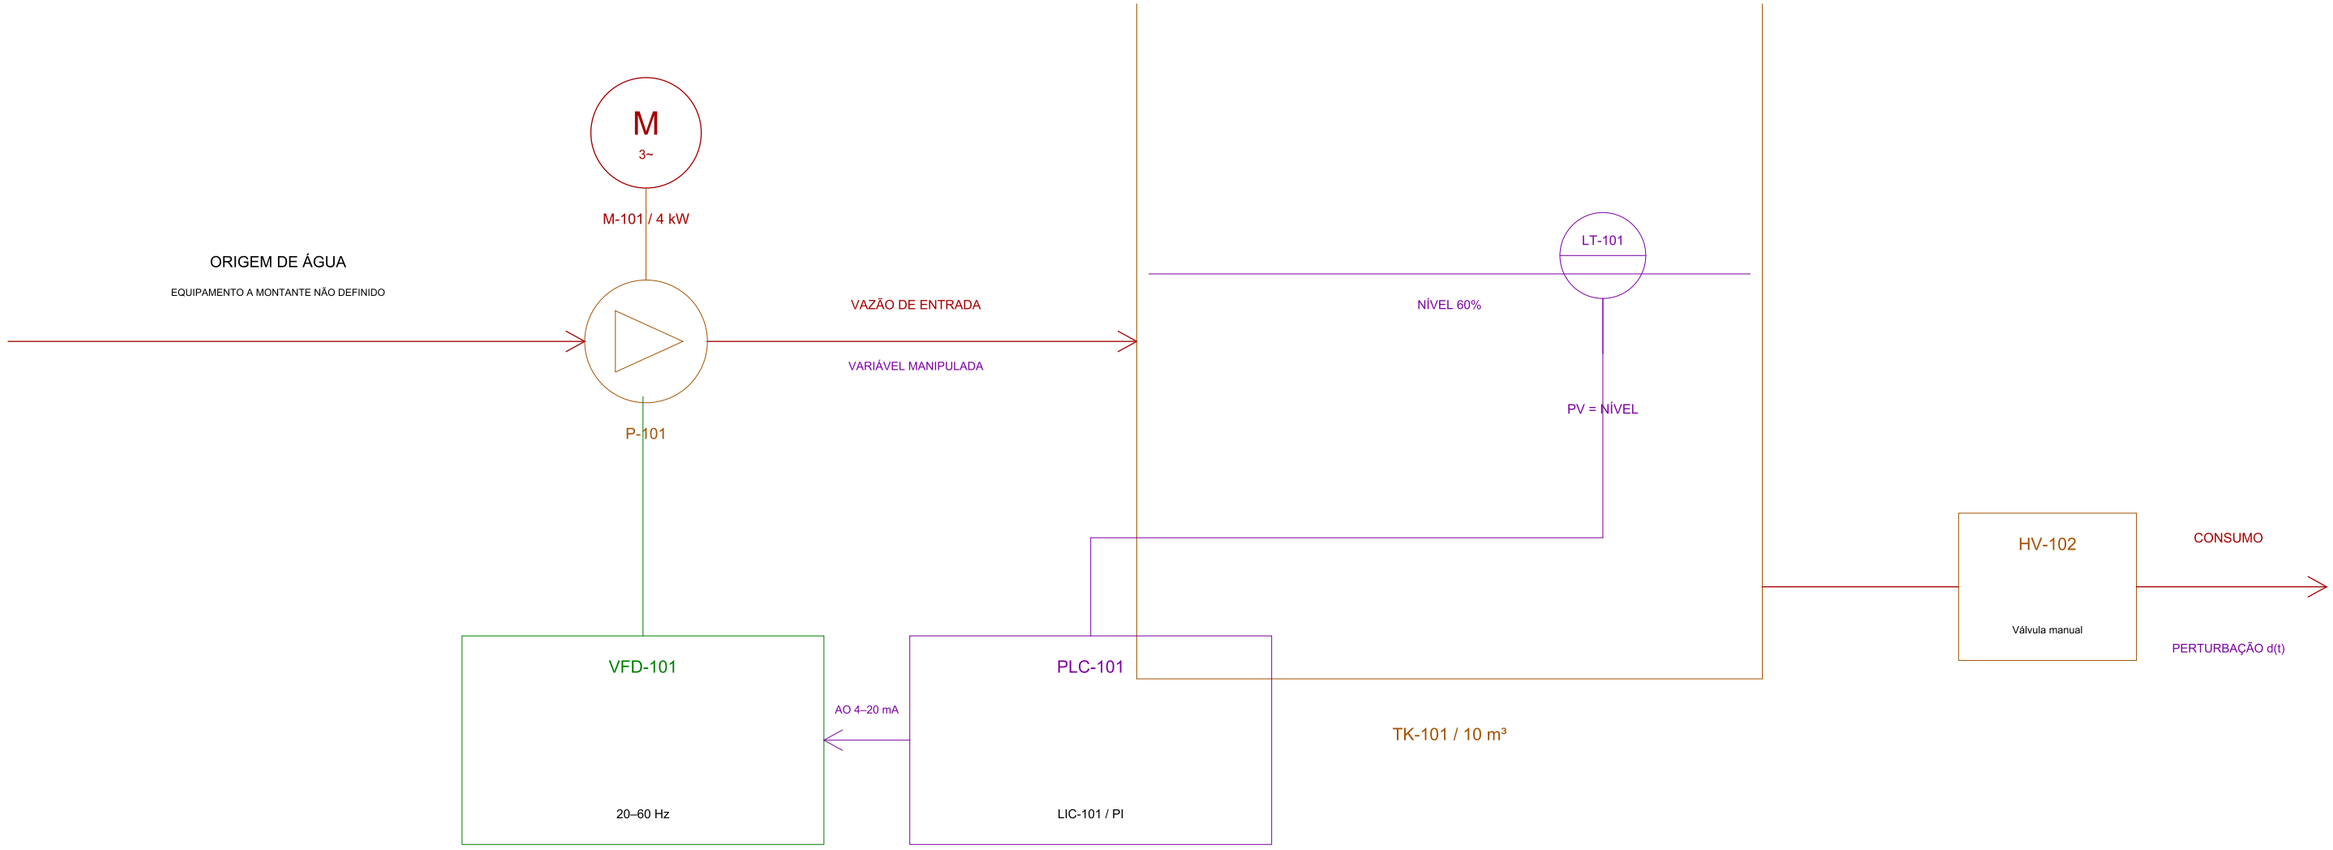

LEGENDA

Tubulação: linha grossa | Sinal: linha fina | HV-102: válvula manual (premissa)

NOTAS DA PRANCHA

TK-101: 10 m³ (premissa). Operação normal: 30–80%; SP inicial: 60%.
Origem e equipamento a montante não definidos.
A vazão de consumo é a perturbação principal da malha de nível.

AVISO OBRIGATÓRIO

Projeto acadêmico e conceitual. Não deve ser utilizado para fabricação, instalação ou execução de serviços sem revisão, dimensionamento e responsabilidade de profissional legalmente habilitado.

REV.	DATA	DESCRIÇÃO	RESP.
05	2026-11-06	LEVANTAMENTO DA FONTE	R.E.M.M.

PORTFOLIO DE
ENGENHARIA ELETRICA
BASE ACADEMICA REPRODUZIVEL

A3
PAISAGEM

TITULO

FLUXOGRAMA DO PROCESSO

AUTOR	DATA	REV.	PRANCHA
Rogério Eduardo Moreira Menegueli	2026-11-06	05	01/09

ARQUIVO	UNIDADES	ESCALA	FOLHA	STATUS
01_fluxograma_processo.dxf	mm	S/ESC.	A3	CONCEIT.