
INTERLIGAÇÕES

Conectividade de rede, barramentos, saída, Kelvin, comandos e PE

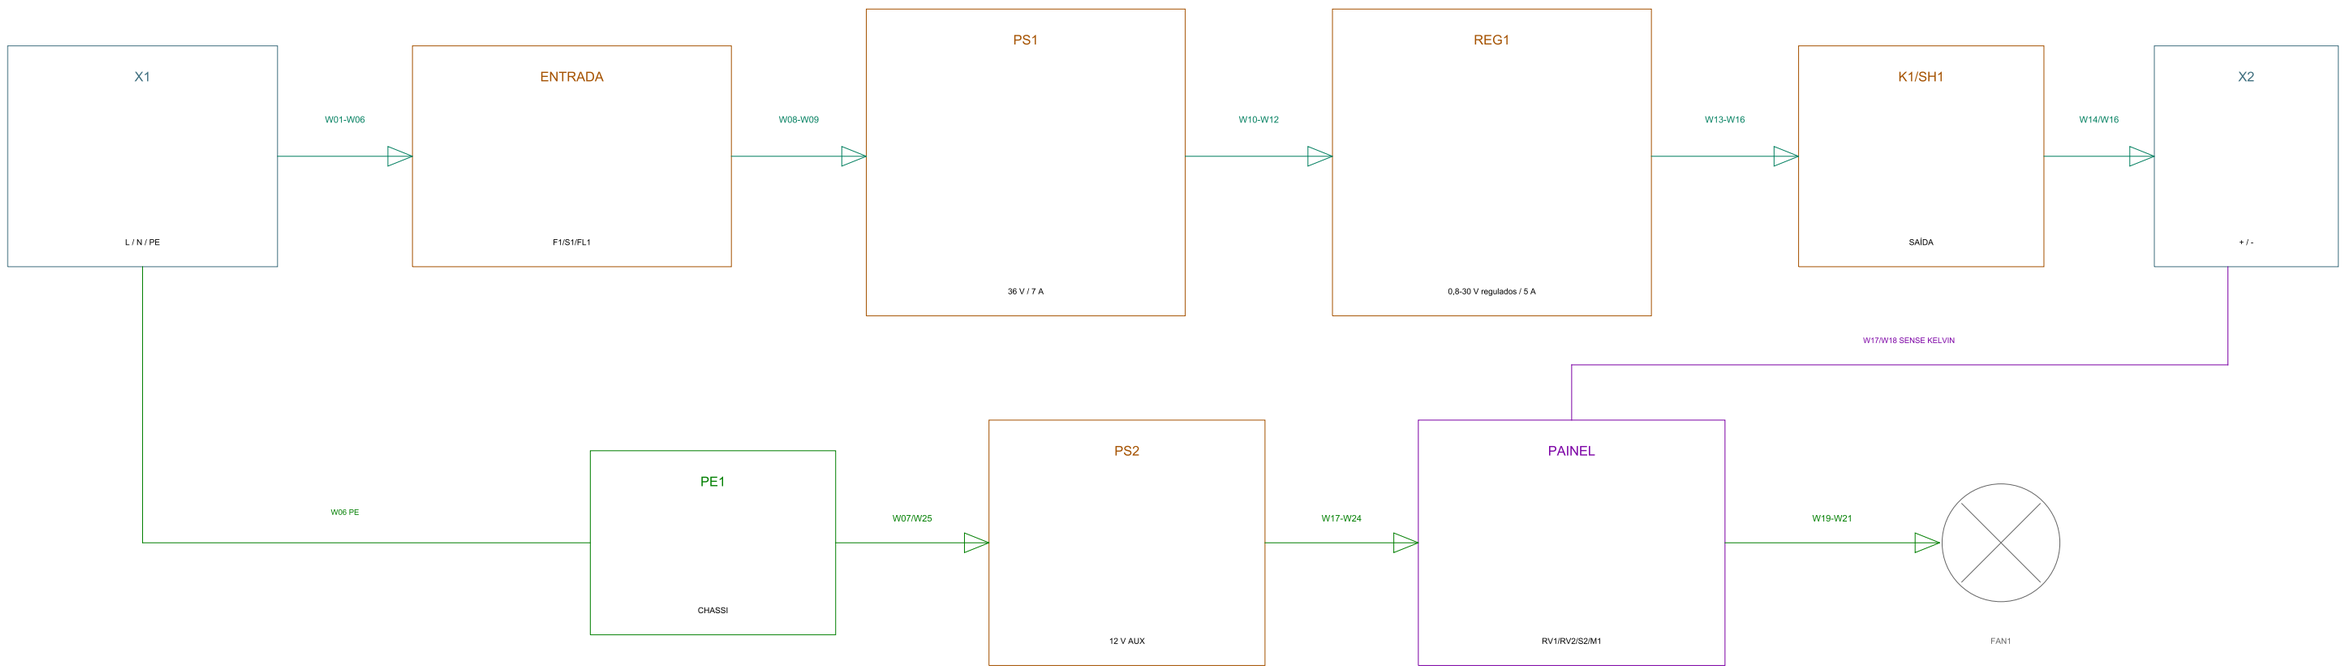

GRUPO	ORIGEM	DESTINO	SEÇÃO	IDENTIFICAÇÃO	FUNÇÃO
W01-W05	X1/F1/S1	FL1	0,75	preto/azul	rede L/N
W06-W07	X1/PE1	chassi/PS1	1,5	verde-amarelo	proteção
W08-W09	FL1	PS1	0,75	preto/azul	rede filtrada
W10-W12	PS1/F2	REG1	2,5	vermelho/preto	barramento 36 V
W13-W16	REG1/K1/SH1	X2	2,5	vermelho/preto	0,8-30 V regulados; 5 A / 150 W máx.
W17-W18	X2	M1	0,5	par vermelho/preto	sense Kelvin
W19-W21	PS2/TH1	FAN1	0,5	vermelho/preto	ventilação
W22-W24	PS2/TS1/S2	K1	0,5	vermelho/branco	habilitação
W25	X3	PE1	1,5	verde-amarelo	borne de chassi
W26-W28	REG1 OUT+/RET	KD1+RD1	A DEFINIR	vermelho/preto	descarga interna parametrizada
W29-W31	X2+/X2-	KD2+RD2	A DEFINIR	vermelho/preto	bloquear se fonte externa conectada

LISTA COMPLETA W01-W31 EM lista-interligacoes.csv | SEÇÕES EM mm²

LEGENDA

Preto/azul: L/N | Verde-amarelo: PE | Vermelho/preto: CC | Branco: comando

NOTAS DA PRANCHA

A lista W01-W31 define intenção de ligação, não chicote liberado.
Confirmar terminais, crimpagem, torque, isolação, cores, proteção e alívio mecânico.

AVISO OBRIGATORIO

Projeto acadêmico e conceitual. Não deve ser utilizado para fabricação, instalação ou execução de serviços sem revisão, dimensionamento e responsabilidade de profissional legalmente habilitado.

REV.	DATA	DESCRICAO	RESP.
04	2026-11-05	TOPOLOGIA E PRE-DIMENSIONAMENTO	R.E.M.M.

PORTFOLIO DE
ENGENHARIA ELETRICA
BASE ACADEMICA REPRODUZIVEL

A3
PAISAGEM

TITULO

INTERLIGAÇÕES

AUTOR	DATA	REV.	PRANCHA
Rogério Eduardo Moreira Menegueli	2026-11-05	04	06/10

ARQUIVO	UNIDADES	ESCALA	FOLHA	STATUS
06_interligacoes.dxf	mm	S/ESC.	A3	CONCEIT.