
PLANTA BAIXA DA SUBESTACAO ABRIGADA

Arranjo fisico, alvenaria, acessos e afastamentos normativos NBR 14039

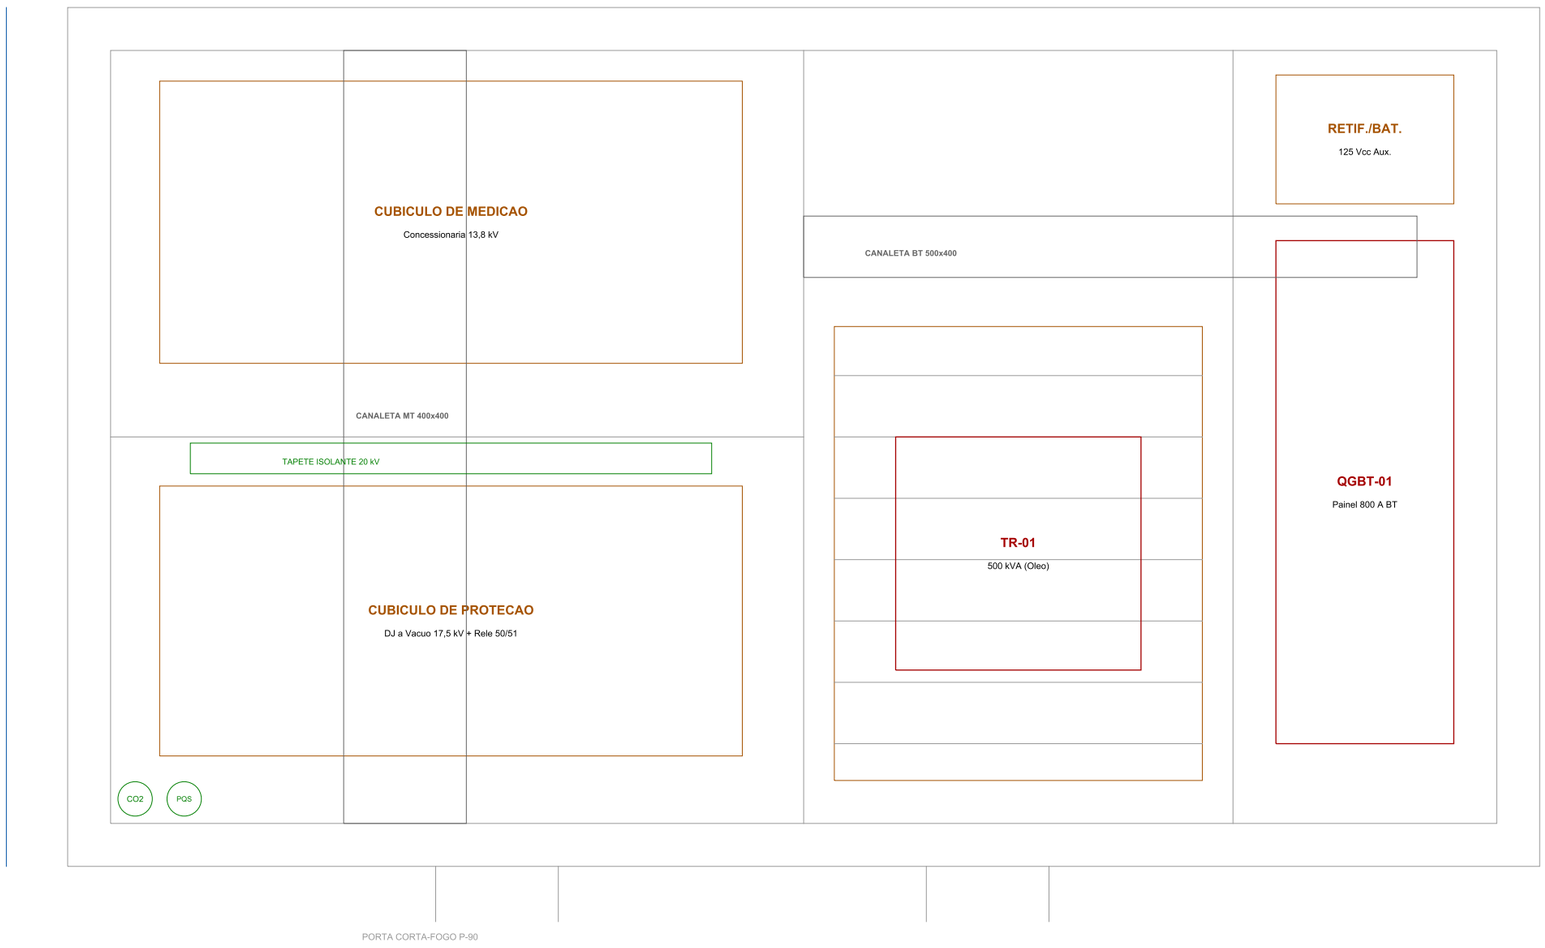

PREMISSAS NBR 14039

1. Pe-direito livre: 3,50 m.

2. Corredor de manobra >= 1,20 m.

3. Abertura das portas para fora.

4. Bacia com volume >= 1,2 m3
   (oleo total trafo = 850 L).

5. Brita n. 1 h=10 cm abafa-chama.

6. Ventilacao natural cruzada:
   - venezianas com tela 2 mm;
   - area util calculada: 1,8 m2.

7. Tapete de seguranca 20 kV.

8. Iluminacao normal e emergencia.

9. Placas 'ALTA TENSAO 13.800 V'.

LEGENDA

Vermelho: equipamentos MT/BT | Cinza: alvenaria/portas | Azul: canaletas | Verde: seguranca

NOTAS DA PRANCHA

Dimensoes civis: 6,00 x 4,00 m externo. Portas corta-fogo P-90 abrindo para fora.
Piso com canaletas tecnicas para cabos de MT e BT. Ventilacao natural cruzada.
Bacia de contencao de oleo sob o transformador com brita n. 1 e dreno sifonado.

AVISO OBRIGATORIO

Projeto acadêmico e conceitual. Não deve ser utilizado para fabricação, instalação ou execução de serviços sem revisão, dimensionamento e responsabilidade de profissional legalmente habilitado.

REV.	DATA	DESCRICAO	RESP.
03	2026-11-06	ESTUDO DE ATERRAMENTO	R.E.M.M.

PORTFOLIO DE
ENGENHARIA ELETRICA
BASE ACADEMICA REPRODUZIVEL

A3
PAISAGEM

TITULO

PLANTA BAIXA DA SUBESTACAO ABRIGADA

AUTOR	DATA	REV.	PRANCHA
Rogério Eduardo Moreira Menegueli	2026-11-06	03	02/08

ARQUIVO	UNIDADES	ESCALA	FOLHA	STATUS
02_planta_baixa_subestacao.dxf	mm	1:50	A3	CONCEIT.