
ARQUITETURA GERAL DO VEÍCULO ELÉTRICO

EV-07: domínios de energia, controle e comunicação

DOMÍNIO DE TRAÇÃO HV - 320 A 450 Vcc (PREMISSA)

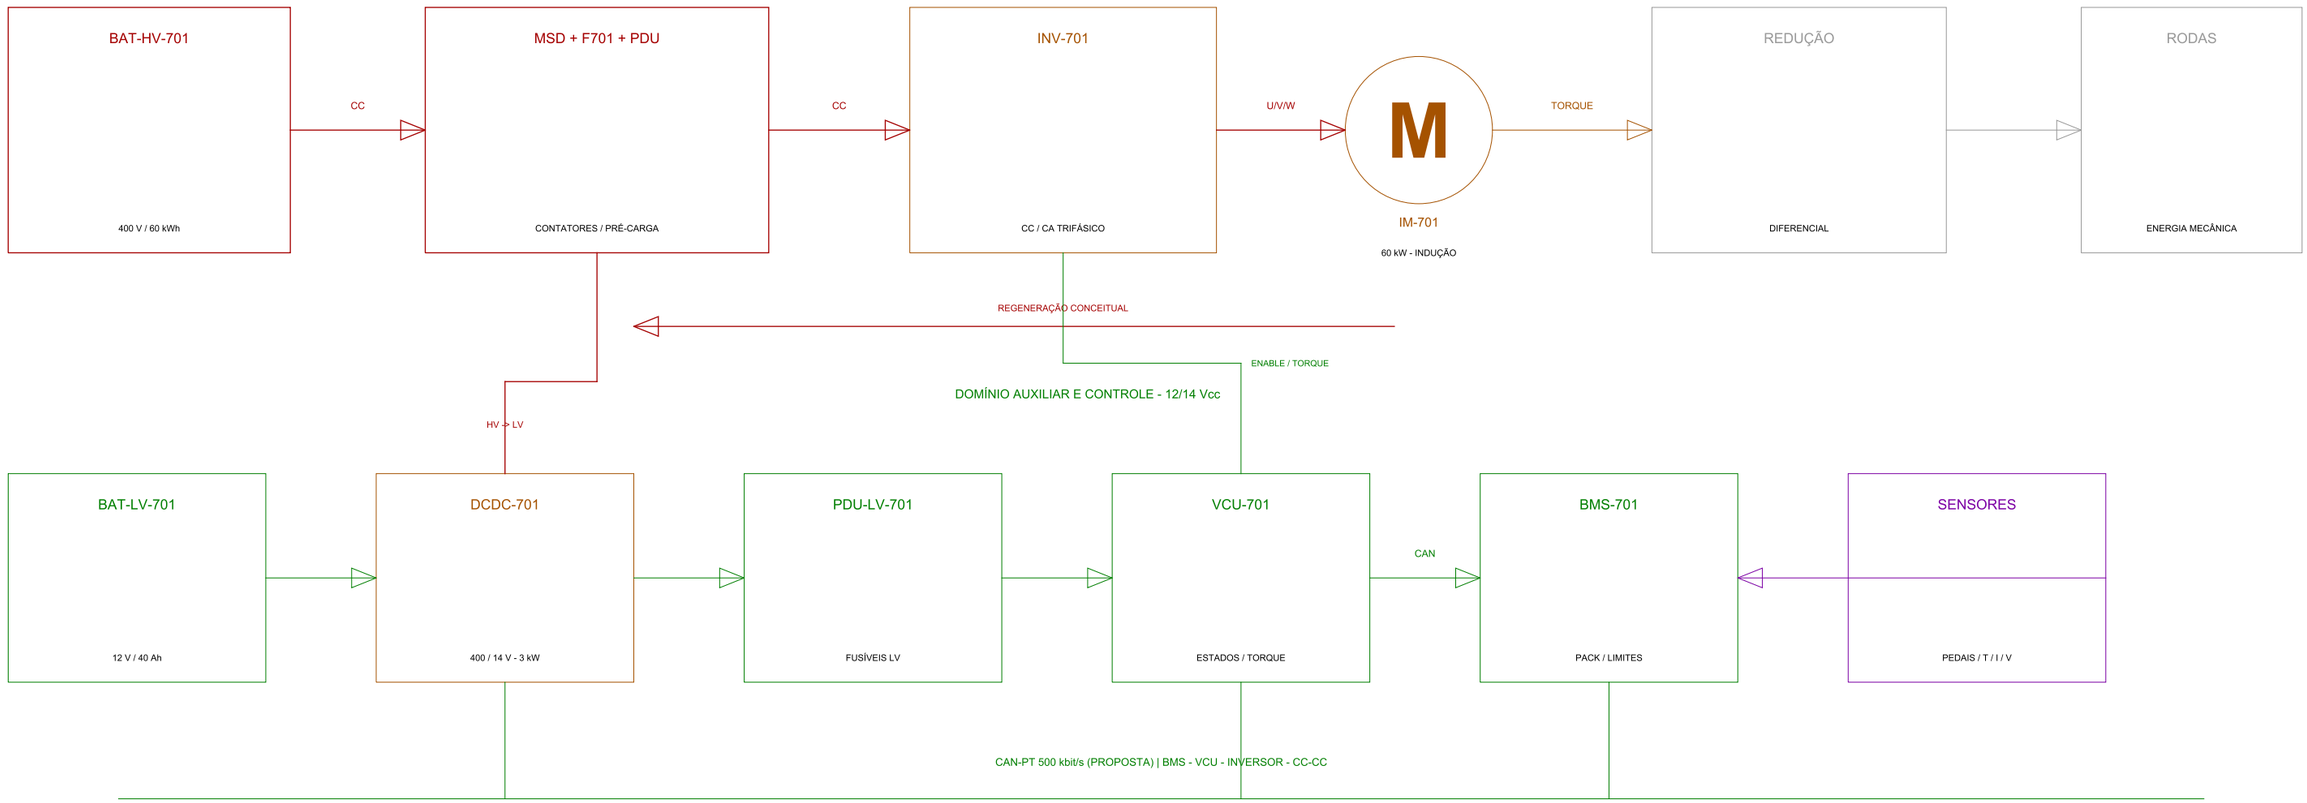

FATO: funções gerais | PREMISSA: valores | PROPOSTA: topologia EV-07 | RESULTADO EXPERIMENTAL: NENHUM

LEGENDA

Vermelho: HV | Azul: LV | Verde: comando/CAN | Ciano: sinais | Tracejado: limite funcional

NOTAS DA PRANCHA

Setas mostram fluxo funcional, não posição física nem chicote executivo.
Regeneração é conceitual e depende dos limites de INV-701, BMS-701 e bateria.

AVISO OBRIGATORIO

Projeto acadêmico e conceitual. Não deve ser utilizado para fabricação, instalação ou execução de serviços sem revisão, dimensionamento e responsabilidade de profissional legalmente habilitado.

REV.	DATA	DESCRICAO	RESP.
02	2026-11-05	REVISAO VISUAL 02	R.E.M.M.

PORTFOLIO DE
ENGENHARIA ELETRICA
BASE ACADEMICA REPRODUZIVEL

A3
PAISAGEM

TITULO

ARQUITETURA GERAL DO VEÍCULO ELÉTRICO

AUTOR	DATA	REV.	PRANCHA
Rogério Eduardo Moreira Menegueli	2026-11-05	02	01/09

ARQUIVO	UNIDADES	ESCALA	FOLHA	STATUS
01_arquitetura_geral.dxf	mm	S/ESC.	A3	CONCEIT.