
INTERLIGAÇÕES DE CAMPO

Painel, reservatório, bombas, emergência e supervisão remota

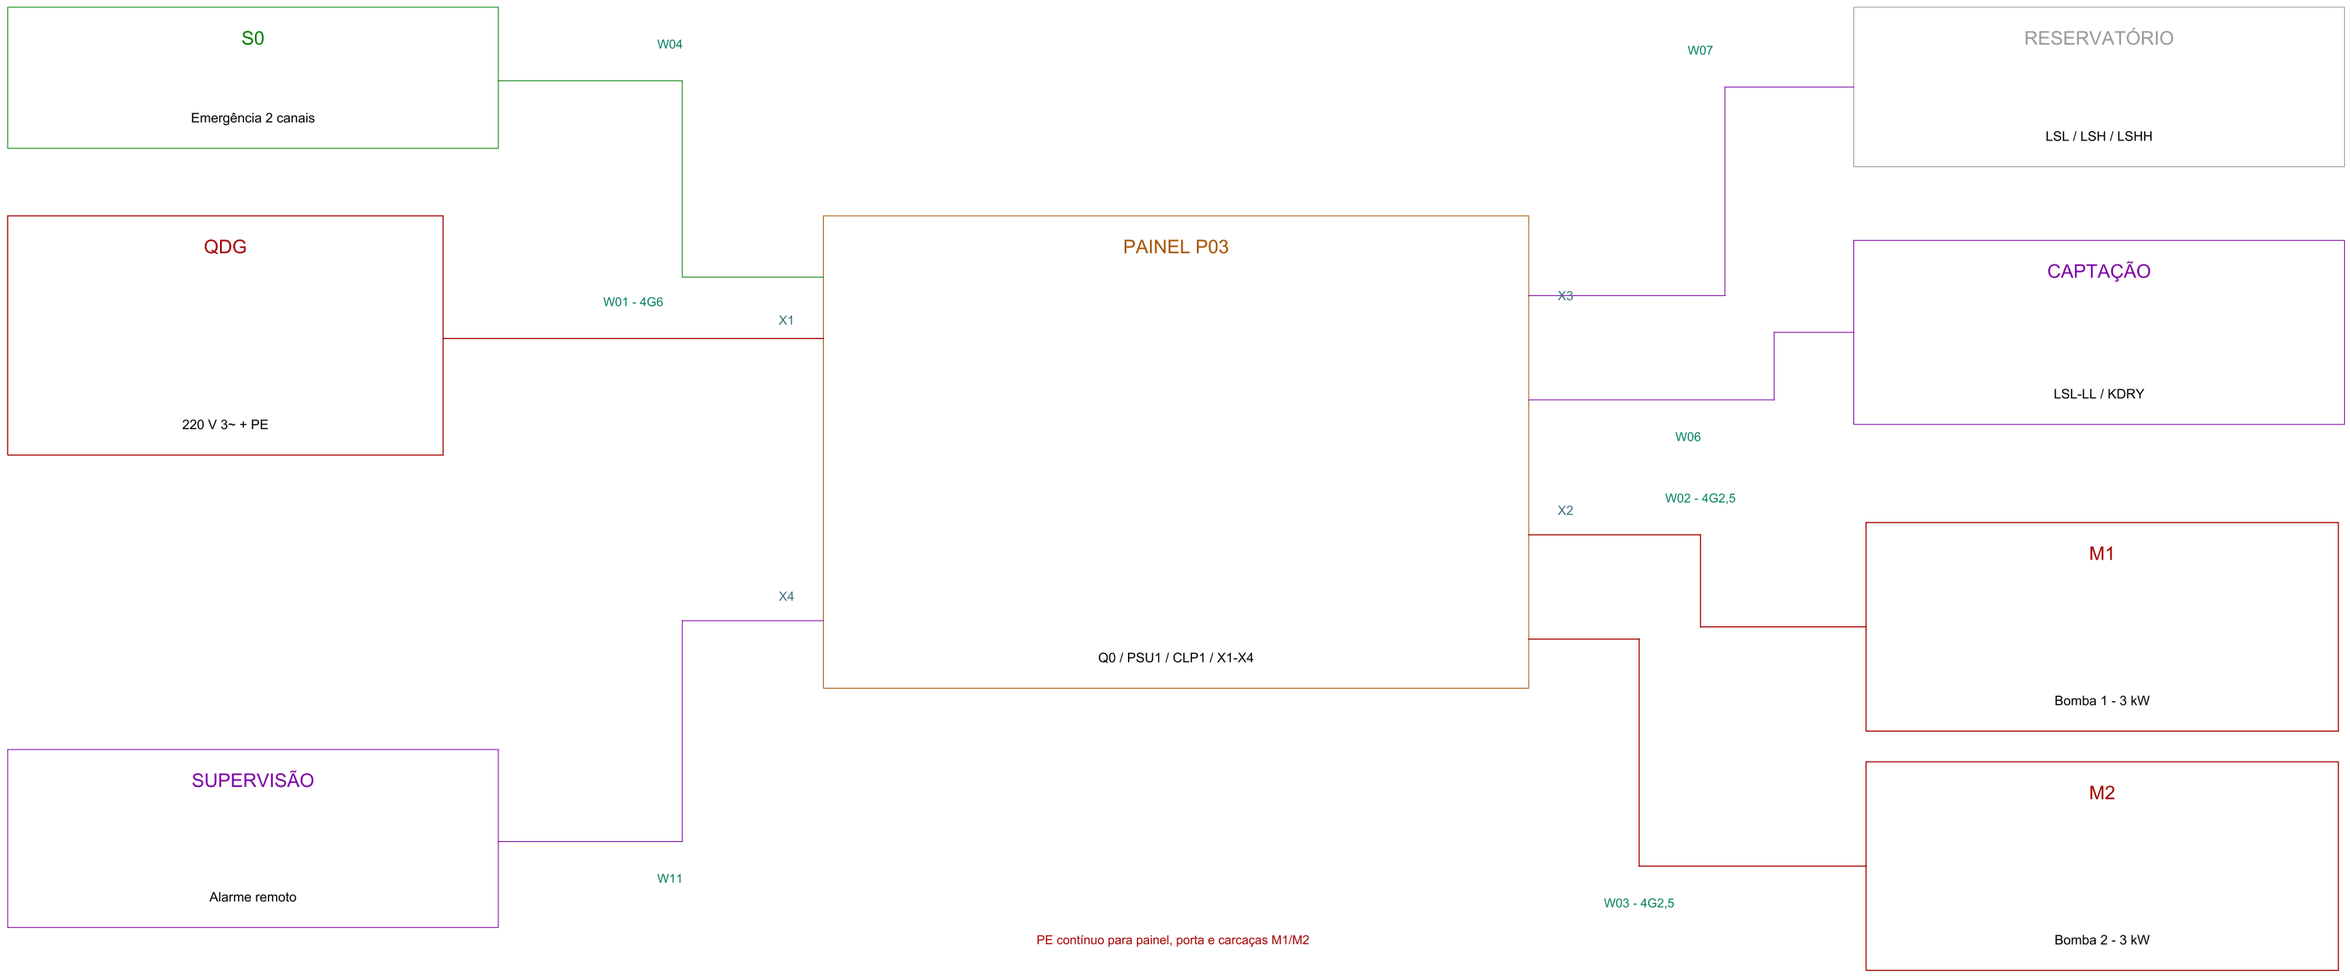

LEGENDA

Linha cheia: potência | tracejado funcional: controle | LS: nível | PE: proteção

NOTAS DA PRANCHA

Comprimentos de W01-W12 são premissas. Confirmar rotas, segregação, EMC, queda de tensão, tipo de sensor e equipotencialização após levantamento de campo.

AVISO OBRIGATÓRIO

Projeto acadêmico e conceitual. Não deve ser utilizado para fabricação, instalação ou execução de serviços sem revisão, dimensionamento e responsabilidade de profissional legalmente habilitado.

REV.	DATA	DESCRIÇÃO	RESP.
01	2026-11-05	REVISAO VISUAL 01	R.E.M.M.

PORTFOLIO DE
ENGENHARIA ELETRICA
BASE ACADEMICA REPRODUZIVEL

A3
PAISAGEM

TITULO

INTERLIGAÇÕES DE CAMPO

AUTOR	DATA	REV.	PRANCHA
Rogério Eduardo Moreira Menegueli	2026-11-05	01	08/08

ARQUIVO	UNIDADES	ESCALA	FOLHA	STATUS
08_interligacoes_campo.dxf	mm	S/ESC.	A3	CONCEIT.