
DIAGRAMA ELÉTRICO

Potência 220 V 3~ e comando/instrumentação em 24 Vcc

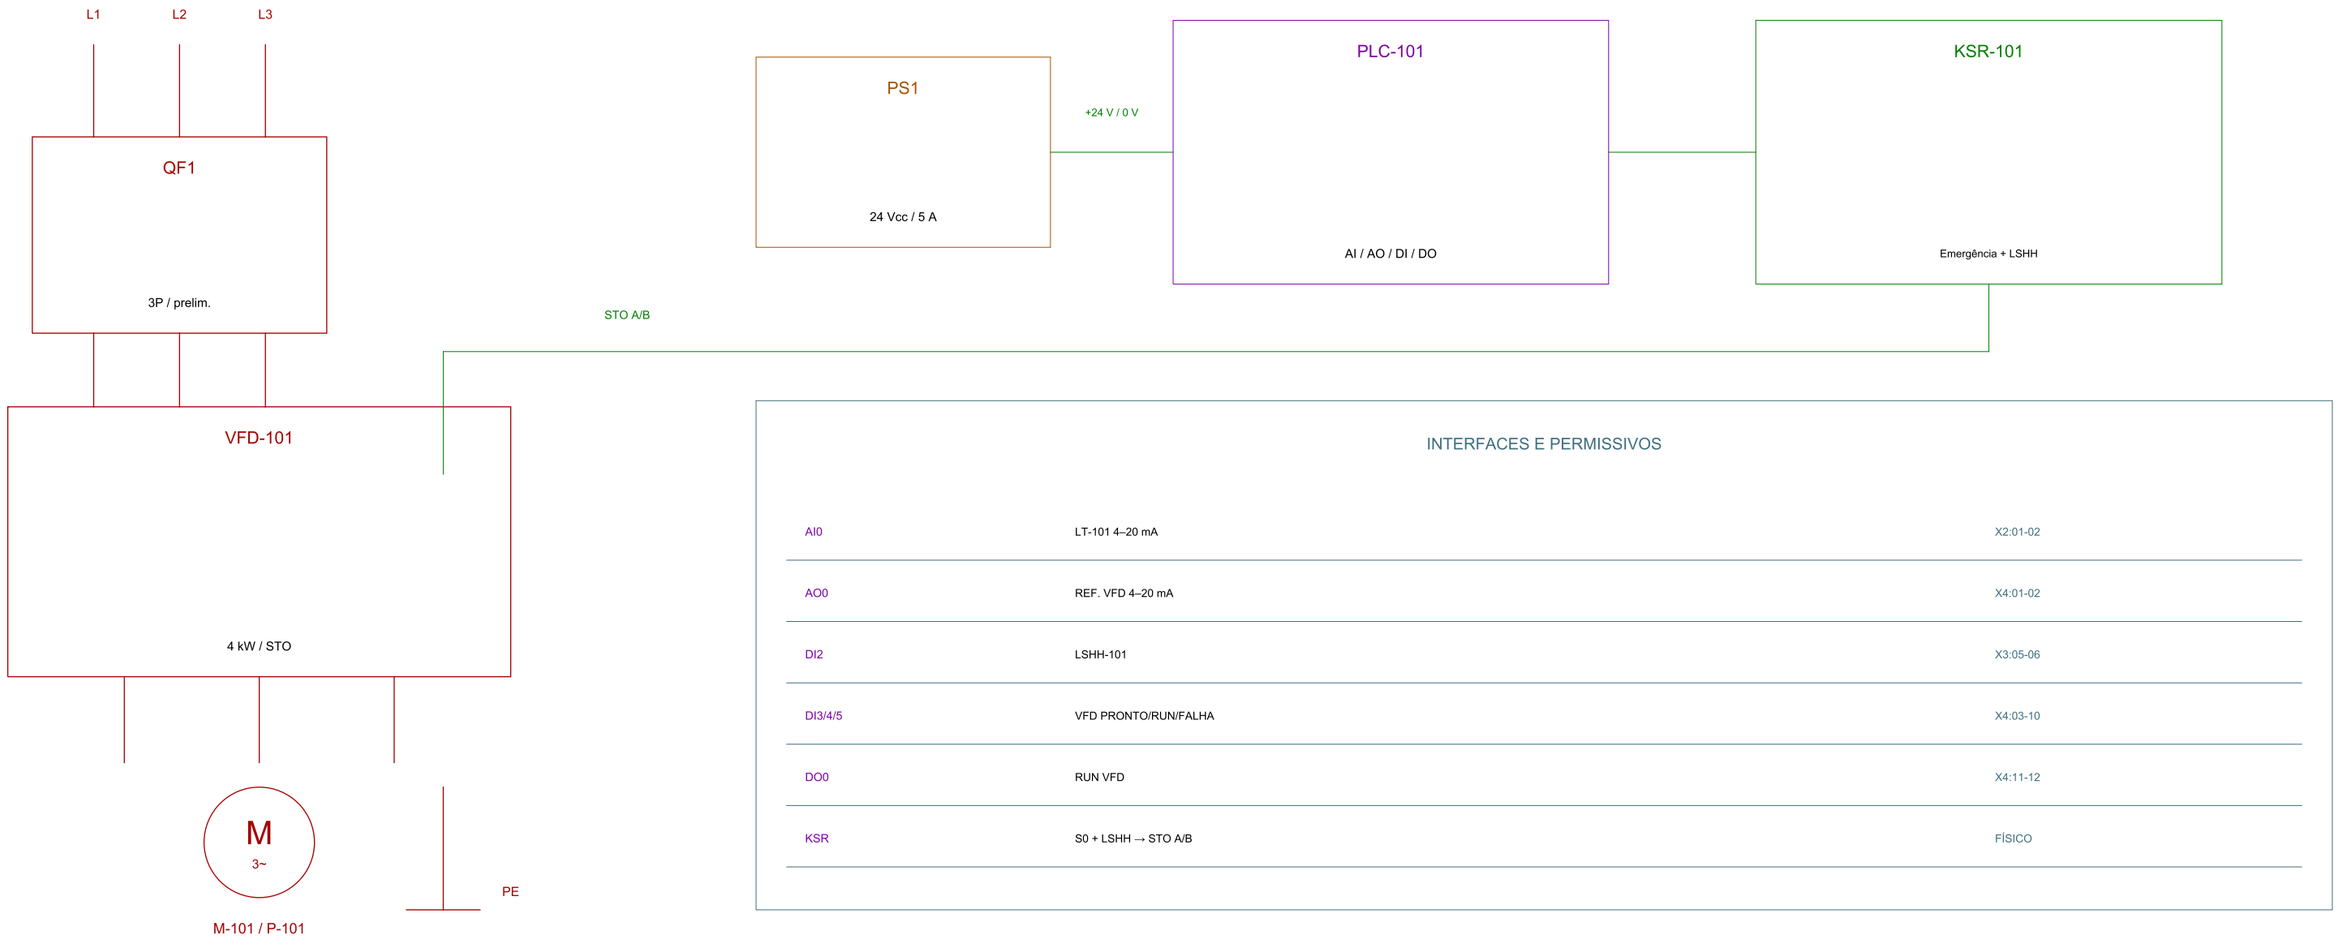

INTERFACES E PERMISSIVOS

AI0	LT-101 4–20 mA	X2:01-02
AO0	REF. VFD 4–20 mA	X4:01-02
DI2	LSHH-101	X3:05-06
DI3/4/5	VFD PRONTO/RUN/FALHA	X4:03-10
DO0	RUN VFD	X4:11-12
KSR	S0 + LSHH → STO A/B	FÍSICO

LEGENDA

QF: disjuntor | PS: fonte | KSR: relé | STO: torque seguro desligado | PE: proteção

NOTAS DA PRANCHA

Proteções e bitolas são preliminares. LSHH-101 participa do bloqueio de STO fora da rotina PID; não se declara categoria, PL ou SIL sem análise de risco.

AVISO OBRIGATÓRIO

Projeto acadêmico e conceitual. Não deve ser utilizado para fabricação, instalação ou execução de serviços sem revisão, dimensionamento e responsabilidade de profissional legalmente habilitado.

REV.	DATA	DESCRIÇÃO	RESP.
01	2026-11-05	REVISAO VISUAL 01	R.E.M.M.

PORTFOLIO DE
ENGENHARIA ELETRICA
BASE ACADEMICA REPRODUZIVEL

A3
PAISAGEM

TITULO

DIAGRAMA ELÉTRICO

AUTOR	DATA	REV.	PRANCHA
Rogério Eduardo Moreira Menegueli	2026-11-05	01	04/06

ARQUIVO	UNIDADES	ESCALA	FOLHA	STATUS
04_diagrama_eletrico.dxf	mm	S/ESC.	A3	CONCEIT.