
DIAGRAMA UNIFILAR CA

Inversor 6 kWca, proteção dedicada e conexão residencial 220 V

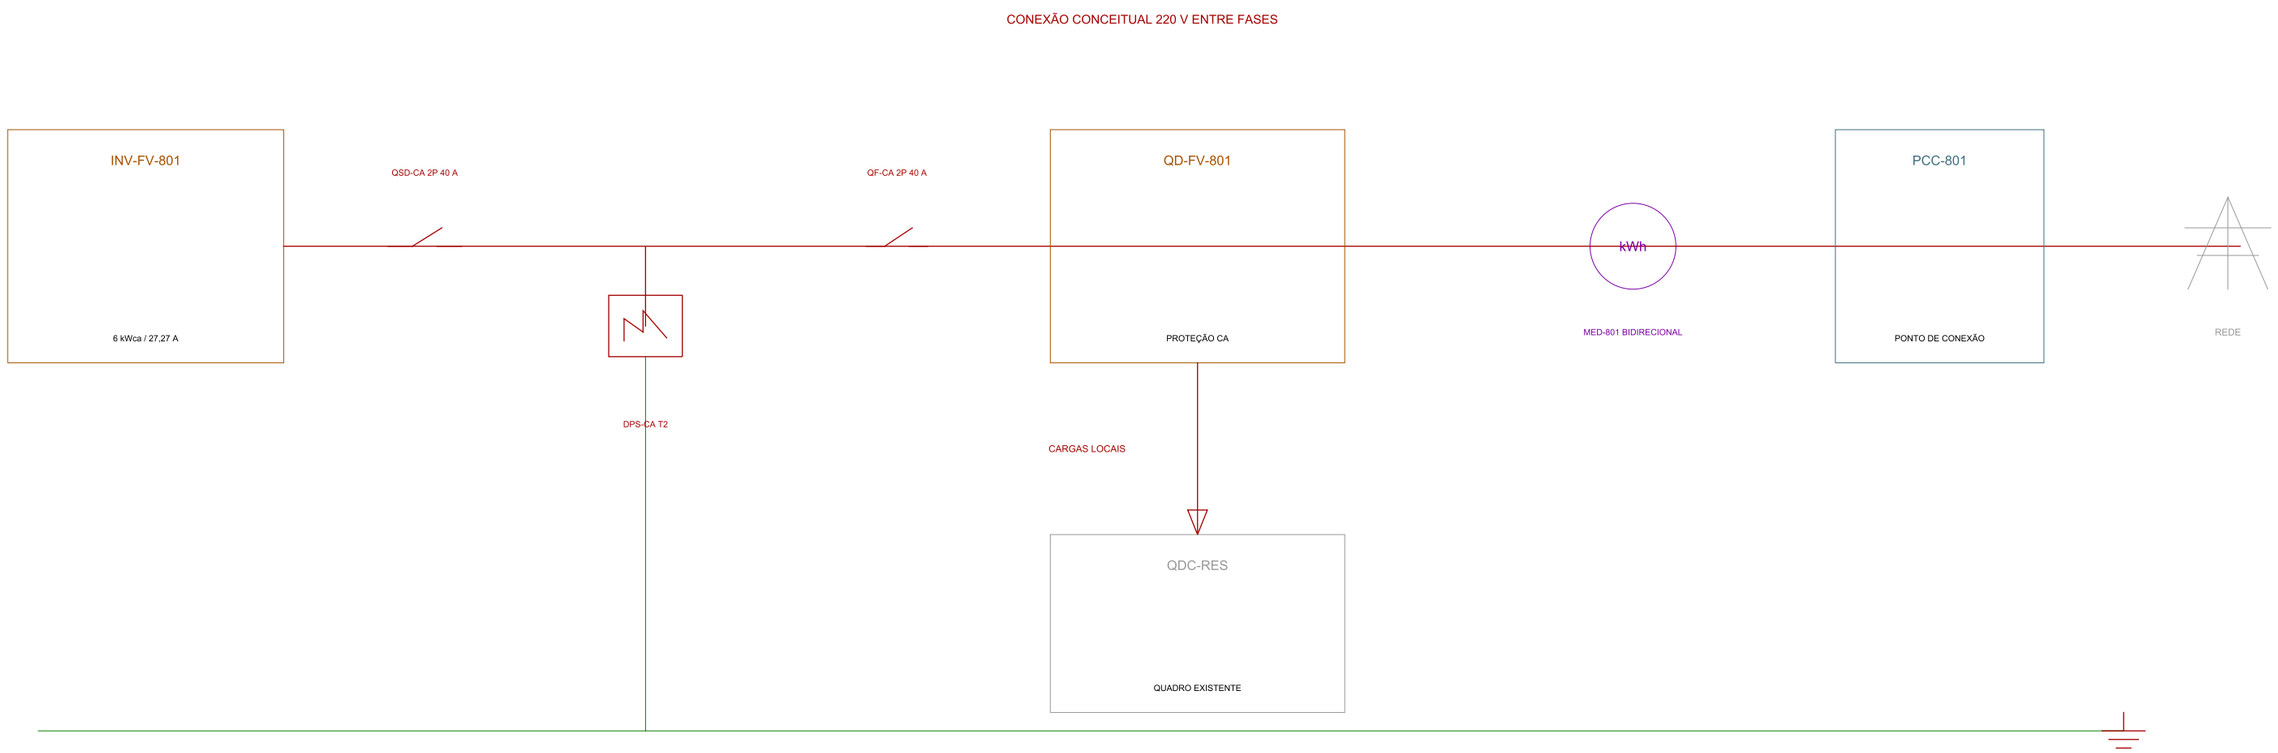

DADO	VALOR	PROTEÇÃO	OBSERVAÇÃO
Potência	6,00 kW	QF 40 A	PREMISSA
Corrente	27,273 A	2 polos	fp=1 ideal
Cabo	10 mm²	PE 10 mm²	A confirmar

REQUISITOS DE CONEXÃO

Distribuidora, orçamento de conexão, medição, anti-ilhamento, qualidade de energia e vistoria permanecem obrigatórios.

LEGENDA

QSD: seccionador | QF: disjuntor | DPS: proteção contra surtos | MED: medidor

NOTAS DA PRANCHA

Anti-ilhamento e parâmetros de rede pertencem ao inversor homologado e à distribuidora.
O circuito CA, Icn, seletividade e aterramento devem ser recalculados no imóvel.

AVISO OBRIGATORIO

Projeto acadêmico e conceitual. Não deve ser utilizado para fabricação, instalação ou execução de serviços sem revisão, dimensionamento e responsabilidade de profissional legalmente habilitado.

REV.	DATA	DESCRICAO	RESP.
01	2026-11-05	REVISAO VISUAL 01	R.E.M.M.

PORTFOLIO DE
ENGENHARIA ELETRICA
BASE ACADEMICA REPRODUZIVEL

A3
PAISAGEM

TITULO

DIAGRAMA UNIFILAR CA

AUTOR	DATA	REV.	PRANCHA
Rogério Eduardo Moreira Menegueli	2026-11-05	01	03/06

ARQUIVO	UNIDADES	ESCALA	FOLHA	STATUS
03_diagrama_unifilar_ca.dxf	mm	S/ESC.	A3	CONCEIT.