
DIAGRAMA DE BLOCOS

Fonte acadêmica 0-30 Vcc / 0-5 A / 150 W com saída isolada e flutuante

CADEIA PRINCIPAL DE ENERGIA

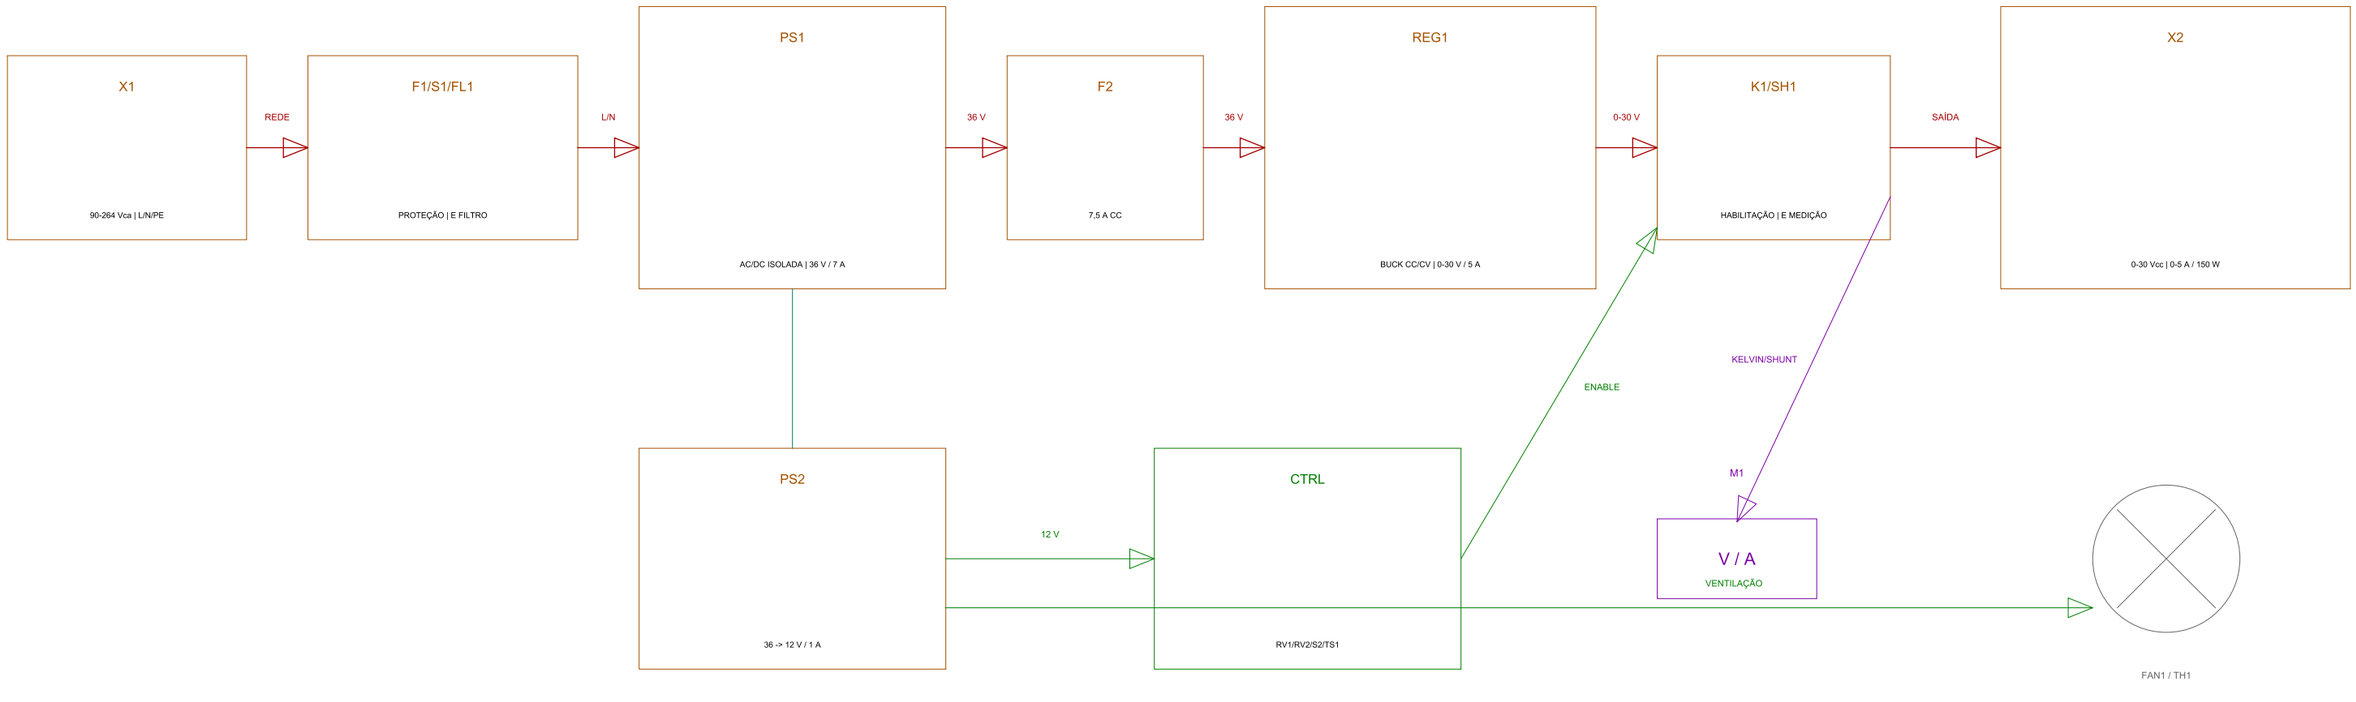

LIMITES DA ARQUITETURA

PE PERMANENTE NO CHASSI | SAÍDA CC FLUTUANTE | NEGATIVO SEM VÍNCULO INTERNO AO PE

Sem PCB, seleção comercial, ensaios dielétricos, EMC, corrente de toque, falha única, calibração, térmica ou certificação.

LEGENDA

Vermelho: potência | Verde: comando/PE | Magenta: medição | Azul: bornes

NOTAS DA PRANCHA

Blocos PS1, REG1, PS2 e M1 são especificações funcionais fictícias.
A arquitetura não comprova isolação, segurança, EMC, precisão ou desempenho.

AVISO OBRIGATORIO

Projeto acadêmico e conceitual. Não deve ser utilizado para fabricação, instalação ou execução de serviços sem revisão, dimensionamento e responsabilidade de profissional legalmente habilitado.

REV.	DATA	DESCRICAO	RESP.
01	2026-11-05	REVISAO VISUAL 01	R.E.M.M.

PORTFOLIO DE
ENGENHARIA ELETRICA
BASE ACADEMICA REPRODUZIVEL

A3
PAISAGEM

TITULO

DIAGRAMA DE BLOCOS

AUTOR	DATA	REV.	PRANCHA
Rogério Eduardo Moreira Menegueli	2026-11-05	01	01/06

ARQUIVO	UNIDADES	ESCALA	FOLHA	STATUS
01_diagrama_blocos.dxf	mm	S/ESC.	A3	CONCEIT.