
ALIMENTAÇÃO 24 Vcc

Distribuição protegida da fonte aos circuitos de automação

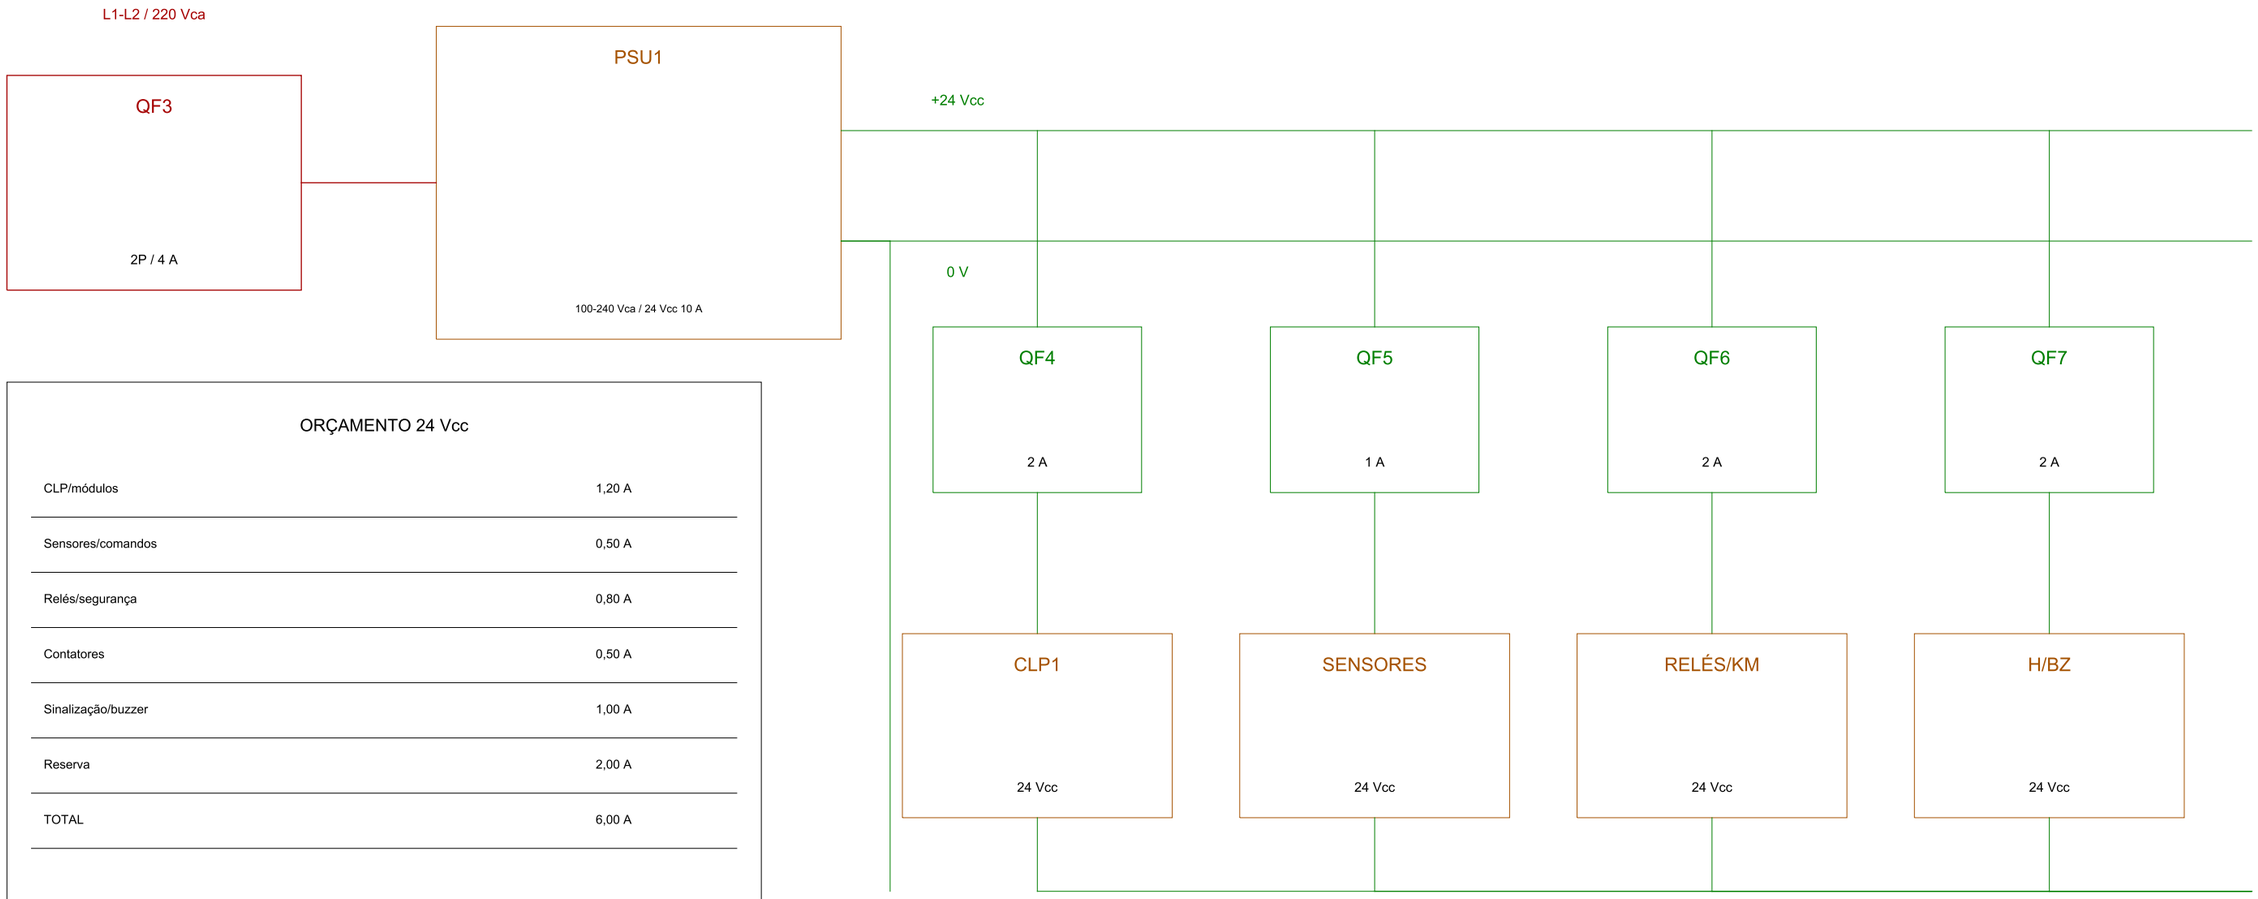

DISTRIBUIÇÃO RADIAL; 0 V COM REFERÊNCIA ÚNICA CONFORME HARDWARE

ORÇAMENTO 24 Vcc

CLP/módulos	1,20 A
Sensores/comandos	0,50 A
Relés/segurança	0,80 A
Contatores	0,50 A
Sinalização/buzzer	1,00 A
Reserva	2,00 A
TOTAL	6,00 A

LEGENDA

+24V/0V: comando | QF4: CLP | QF5: sensores | QF6: relés | QF7: sinalização

NOTAS DA PRANCHA

PSU1: 10 A; carga considerada: 6 A; reserva conceitual: 4 A.
Confirmar corrente de energização, temperatura, seletividade e PELV no projeto real.

AVISO OBRIGATÓRIO

Projeto acadêmico e conceitual. Não deve ser utilizado para fabricação, instalação ou execução de serviços sem revisão, dimensionamento e responsabilidade de profissional legalmente habilitado.

REV.	DATA	DESCRIÇÃO	RESP.
05	2026-11-06	ALTERNATIVAS DO PROCESSO	R.E.M.M.

PORTFOLIO DE
ENGENHARIA ELETRICA
BASE ACADEMICA REPRODUZIVEL

A3
PAISAGEM

TITULO

ALIMENTAÇÃO 24 Vcc

AUTOR	DATA	REV.	PRANCHA
Rogério Eduardo Moreira Menegueli	2026-11-06	05	02/11

ARQUIVO	UNIDADES	ESCALA	FOLHA	STATUS
02_alimentacao_24v.dxf	mm	S/ESC.	A3	CONCEIT.