
MALHA DE ATERRAMENTO E EQUIPOTENCIALIZACAO

Arranjo conceitual; resistividade e seguranca sem estudo

PLANTA DA MALHA DE ATERRAMENTO (ANEL E QUADRICULAS)

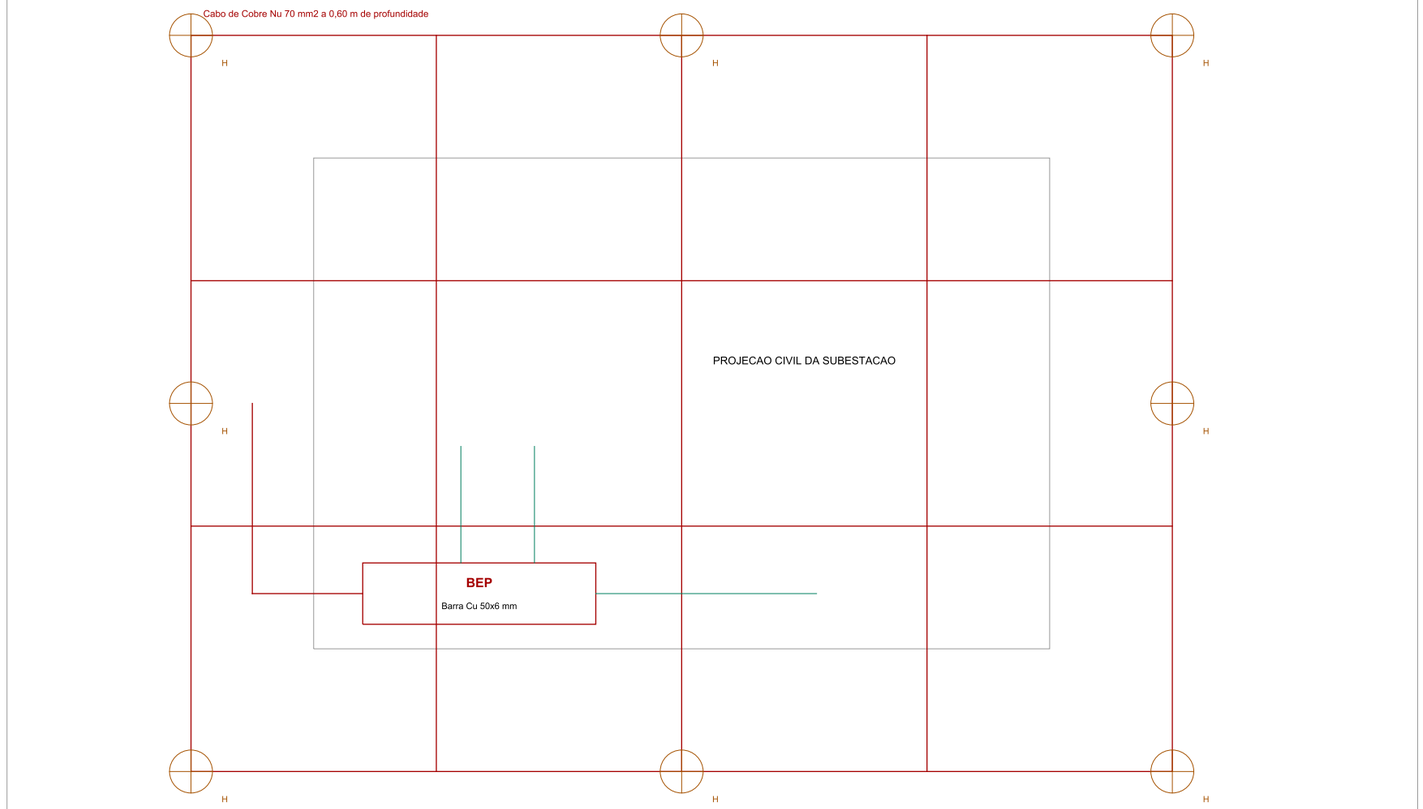

LIMITES DO ESTUDO DE ATERRAMENTO

SEM APROVACAO DE SEGURANCA

DADOS DE SOLO

Resistividade, camadas e camada superficial nao foram medidas.

ARRANJO ILUSTRATIVO

Cu nu 70 mm2 e 8 hastes sao premissas, sem dimensionamento do local.

RESULTADO DA MALHA

Resistencia e elevacao de potencial nao determinadas; sem valor de aprovacao.

POTENCIAIS

GPR, toque, passo e transferencia ainda nao calculados.

PROXIMA ETAPA

Consolidar dados de campo e de falta conforme a prancha 07.

LEGENDA

Cobre nu 70 mm2 | Haste 5/8"x2,4m | Caixa de inspecao solo | BEP: barramento equipotencializacao

NOTAS DA PRANCHA

Anel e grade conceituais em cobre nu 70 mm2 a 0,60 m de profundidade.
8 hastes 5/8 pol. x 2,40 m sao premissas, sem dimensionamento do local.
Resistividade e dados de falta nao medidos; resistencia, GPR, toque e passo nao determinados.

AVISO OBRIGATORIO

Projeto acadêmico e conceitual. Não deve ser utilizado para fabricação, instalação ou execução de serviços sem revisão, dimensionamento e responsabilidade de profissional legalmente habilitado.

REV.	DATA	DESCRICAO	RESP.
04	2026-11-06	CLAREZA DE ESCALAS E LIMITES	R.E.M.M.

PORTFOLIO DE
ENGENHARIA ELETRICA
BASE ACADEMICA REPRODUZIVEL

A3
PAISAGEM

TITULO

MALHA DE ATERRAMENTO E EQUIPOTENCIALIZACAO

AUTOR	DATA	REV.	PRANCHA
Rogério Eduardo Moreira Menegueli	2026-11-06	04	05/08

ARQUIVO	UNIDADES	ESCALA	FOLHA	STATUS
05_malha_aterramento.dxf	mm	1:75	A3	CONCEIT.