
# DIAGRAMA UNIFILAR CA

Inversor 6 kWca, proteção dedicada e conexão residencial 220 V

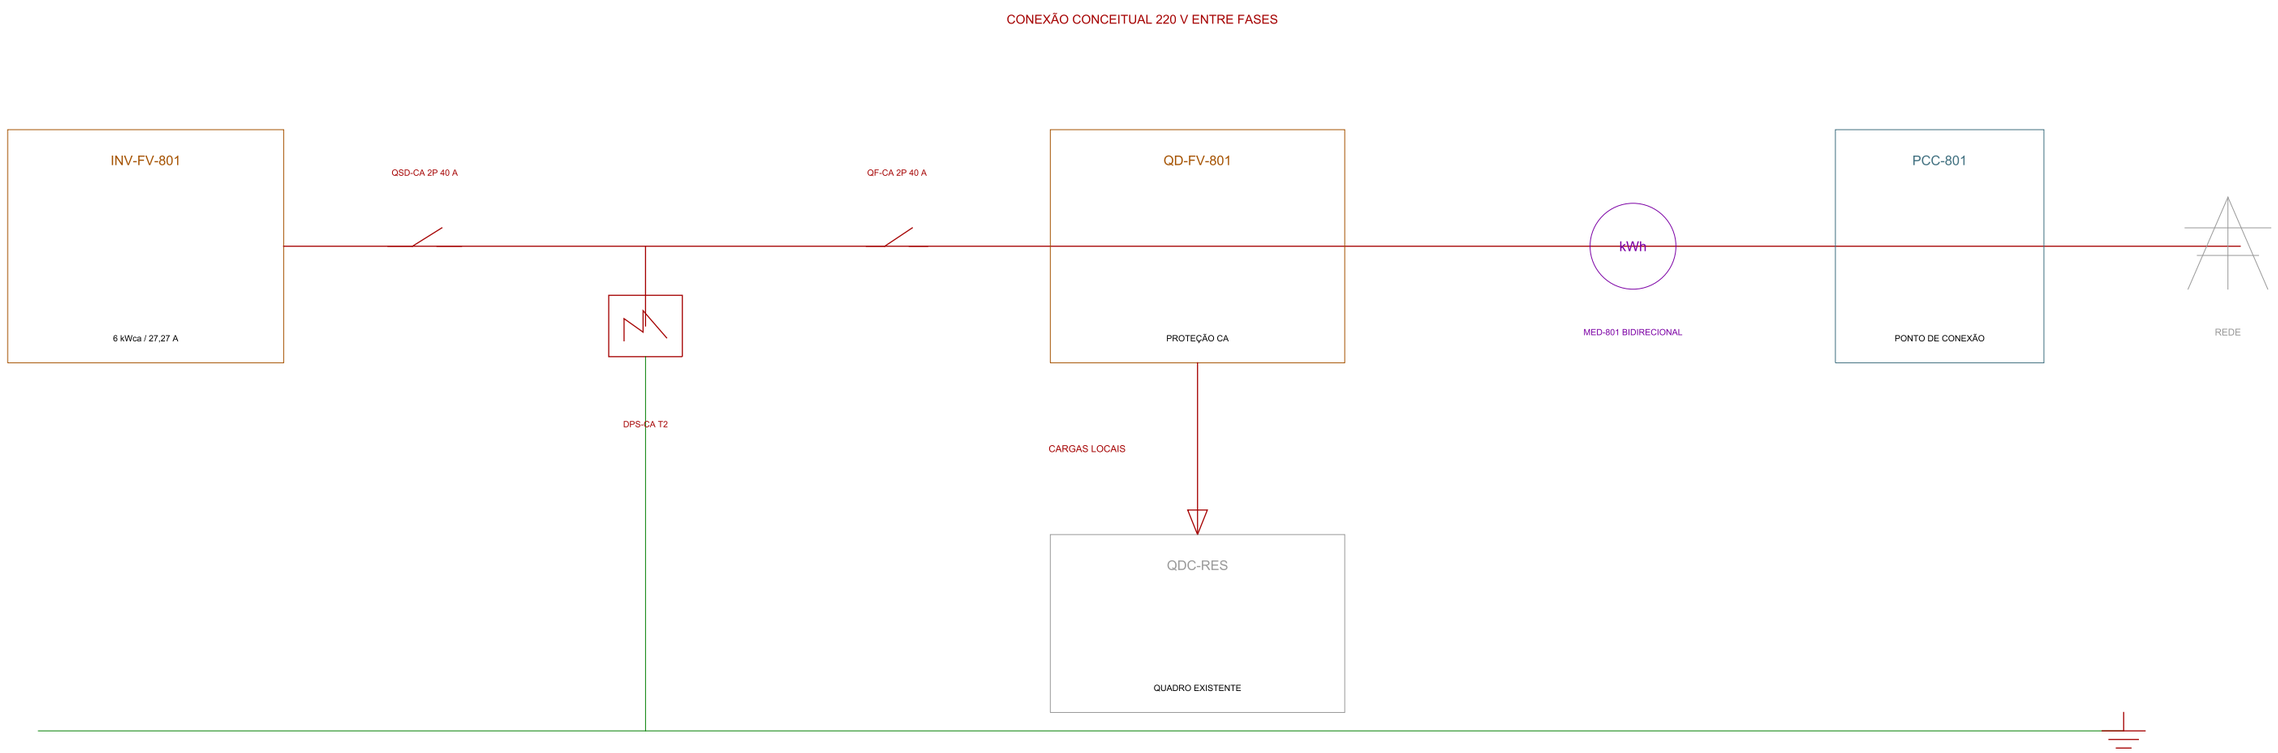


| DADO | VALOR | PROTEÇÃO | OBSERVAÇÃO |
|---|---|---|---|
| Potência | 6,00 kW | QF 40 A | PREMISSA |
| Corrente | 27,273 A | 2 polos | fp=1 ideal |
| Cabo | 10 mm² | PE 10 mm² | A confirmar |

REQUISITOS DE CONEXÃO

Distribuidora, orçamento de conexão, medição, anti-ilhamento, qualidade de energia e vistoria permanecem obrigatórios.

## LEGENDA

QSD: seccionador | QF: disjuntor | DPS: proteção contra surtos | MED: medidor

## NOTAS DA PRANCHA

Anti-ilhamento e parâmetros de rede pertencem ao inversor homologado e à distribuidora.
O circuito CA, Icn, seletividade e aterramento devem ser recalculados no imóvel.

## AVISO OBRIGATORIO

Projeto acadêmico e conceitual. Não deve ser utilizado para fabricação, instalação ou execução de serviços sem revisão, dimensionamento e responsabilidade de profissional legalmente habilitado.

| REV. | DATA | DESCRICAO | RESP. |
|---|---|---|---|
| 03 | 2026-11-06 | ENVELOPE TERMICO 03 | R.E.M.M. |

**PORTFOLIO DE**
**ENGENHARIA ELETRICA**
BASE ACADEMICA REPRODUZIVEL

**A3**
PAISAGEM

TITULO

DIAGRAMA UNIFILAR CA

| AUTOR | DATA | REV. | PRANCHA |
|---|---|---|---|
| Rogério Eduardo Moreira Menegueli | 2026-11-06 | 03 | 03/08 |

| ARQUIVO | UNIDADES | ESCALA | FOLHA | STATUS |
|---|---|---|---|---|
| 03_diagrama_unifilar_ca.dxf | mm | S/ESC. | A3 | CONCEIT. |