
LAYOUT DO CCM

Arranjo conceitual do invólucro 1800 x 1000 x 400 mm

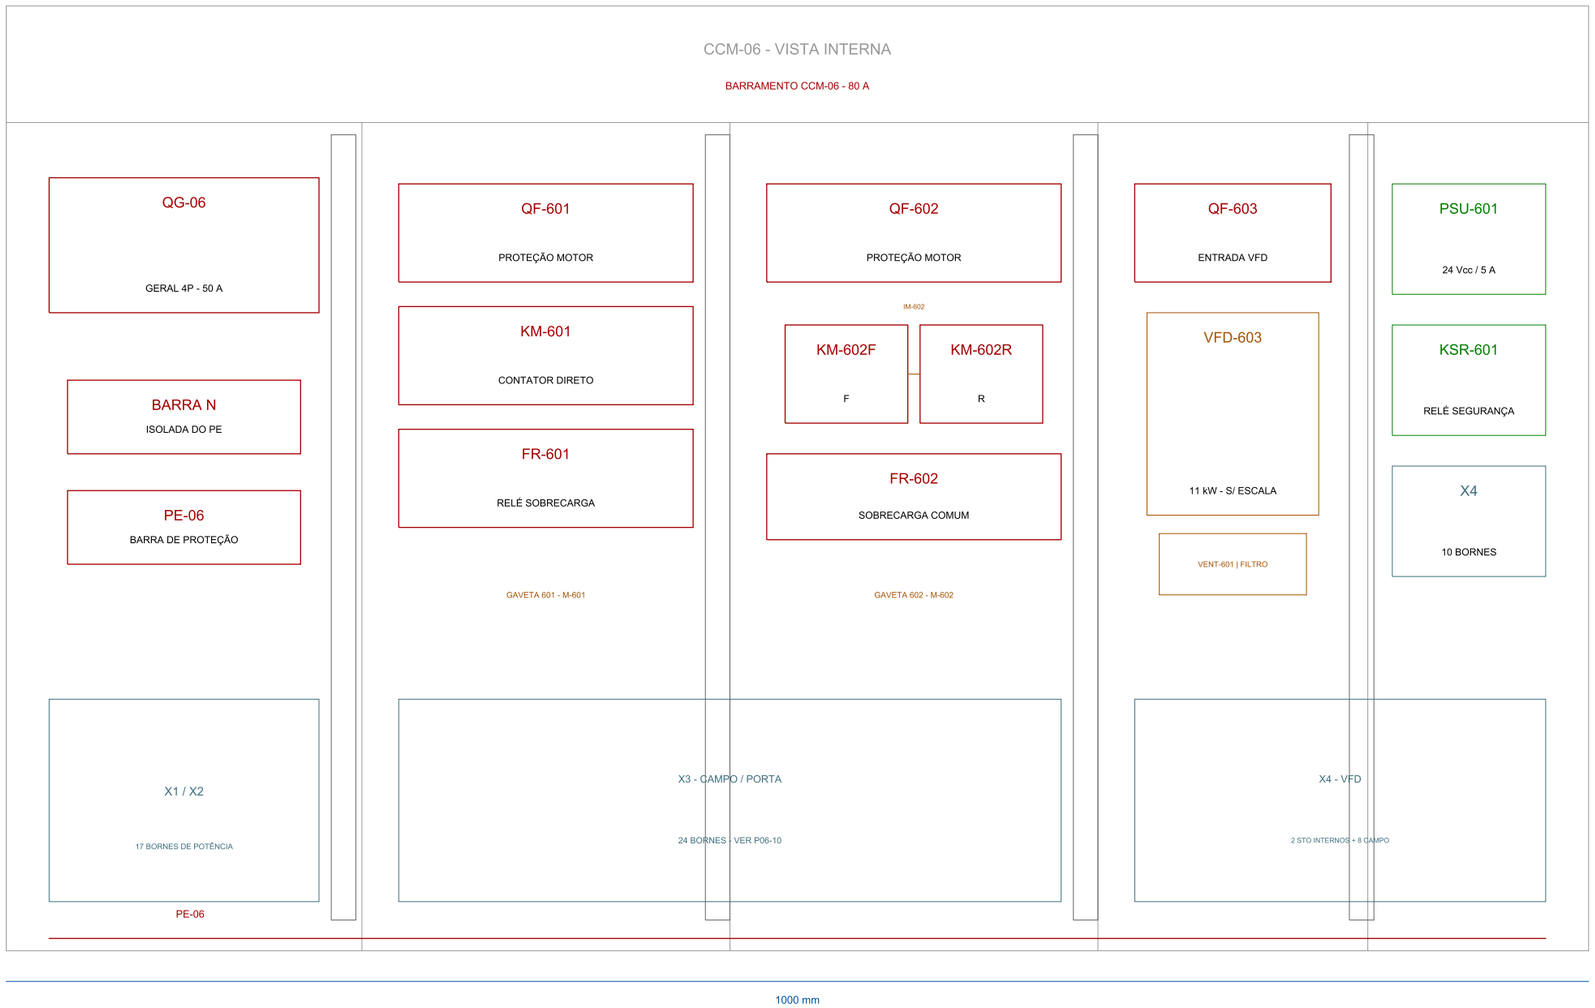

ARRANJO FUNCIONAL

- Invólucro: 1800 x 1000 x 400 mm
- Acesso frontal: >= 1,20 m
- Entrada de cabos: inferior
- QF, contator e relé por gaveta
- Reversão: dois contatores + IM
- VFD com ventilação indicada
- PE contínuo; N isolado de PE
- STO ligado ao KSR internamente
- Comando separado da potência
- Canaletas com reserva >= 30%
- Botoeiras: lista de bornes P06-10
- Grau IP depende do ambiente
- Dimensões de fabricante pendentes
- Dissipação requer cálculo térmico

LEGENDA

Azul: comando | Vermelho: potência | Cinza: canaleta | PE: barra de proteção

NOTAS DA PRANCHA

Confirmar ventilação, perdas, segregação, acesso, EMC e raios de curvatura.
Dimensões, folgas e forma de separação são premissas acadêmicas.

AVISO OBRIGATORIO

Projeto acadêmico e conceitual. Não deve ser utilizado para fabricação, instalação ou execução de serviços sem revisão, dimensionamento e responsabilidade de profissional legalmente habilitado.

REV.	DATA	DESCRICAO	RESP.
04	2026-11-05	INTERLIGACAO X3/X4	R.E.M.M.

PORTFOLIO DE
ENGENHARIA ELETRICA
BASE ACADEMICA REPRODUZIVEL

A3
PAISAGEM

TITULO

LAYOUT DO CCM

AUTOR	DATA	REV.	PRANCHA
Rogério Eduardo Moreira Menegueli	2026-11-05	04	05/10

ARQUIVO	UNIDADES	ESCALA	FOLHA	STATUS
05_layout_ccm.dxf	mm	S/ESC.	A3	CONCEIT.