
ALIMENTACAO HVSC NO CAIS — DIAGRAMA UNIFILAR

Rede do porto, transformacao, quadro HVSC e interface eletrica com o navio

HVSC CONCEITUAL | S=3,2 MVA* | 13,8/6,6 kV* | 60 Hz*

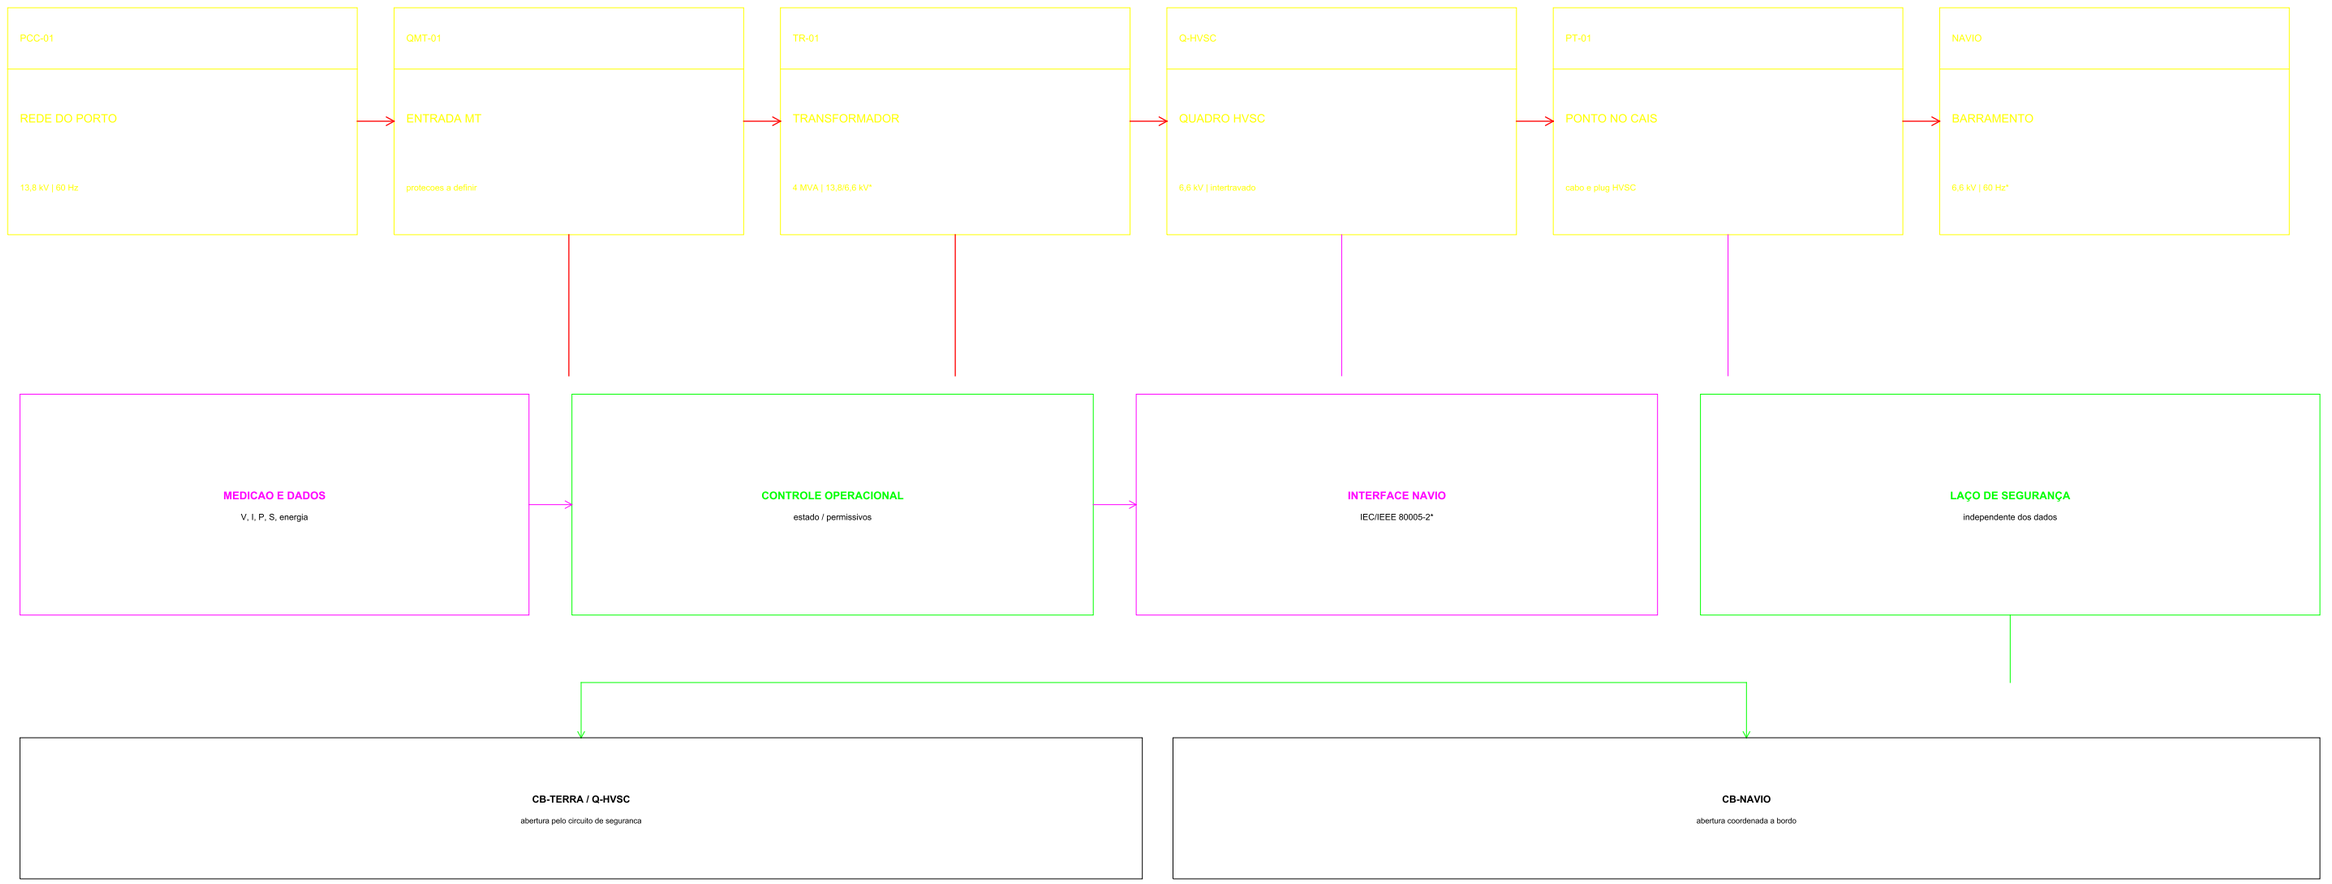

* Compatibilidade de tensao, frequencia, aterramento, conectores e protecao depende do navio e do porto.

LEGENDA

HVSC: conexao de alta tensao em terra | QMT: quadro MT | CB: disjuntor | PCC: ponto de acoplamento comum | S: potencia aparente

NOTAS DA PRANCHA

Base ilustrativa: 3,2 MVA em 6,6 kV/60 Hz; entrada 13,8 kV; transformador 4 MVA.
Nao define protecoes, aterramento, cabos, aterramento do neutro ou parametros de equipamento.

AVISO OBRIGATORIO

Projeto acadêmico e conceitual. Não deve ser utilizado para fabricação, instalação ou execução de serviços sem revisão, dimensionamento e responsabilidade de profissional legalmente habilitado.

REV.	DATA	DESCRICAO	RESP.
00	2026-11-06	EMISSAO INICIAL	R.E.M.M.

PORTFOLIO DE
ENGENHARIA ELETRICA
BASE ACADEMICA REPRODUZIVEL

A3
PAISAGEM

TITULO

ALIMENTACAO HVSC NO CAIS — DIAGRAMA UNIFILAR

AUTOR	DATA	REV.	PRANCHA
Rogério Eduardo Moreira Menegueli	2026-11-06	00	01/03

ARQUIVO	UNIDADES	ESCALA	FOLHA	STATUS
01_unifilar_hvsc_cais.dxf	mm	S/ESC.	A3	CONCEIT.