
DISPOSIÇÃO DOS MÓDULOS

Arranjo acadêmico de 6,60 kWp em duas strings independentes

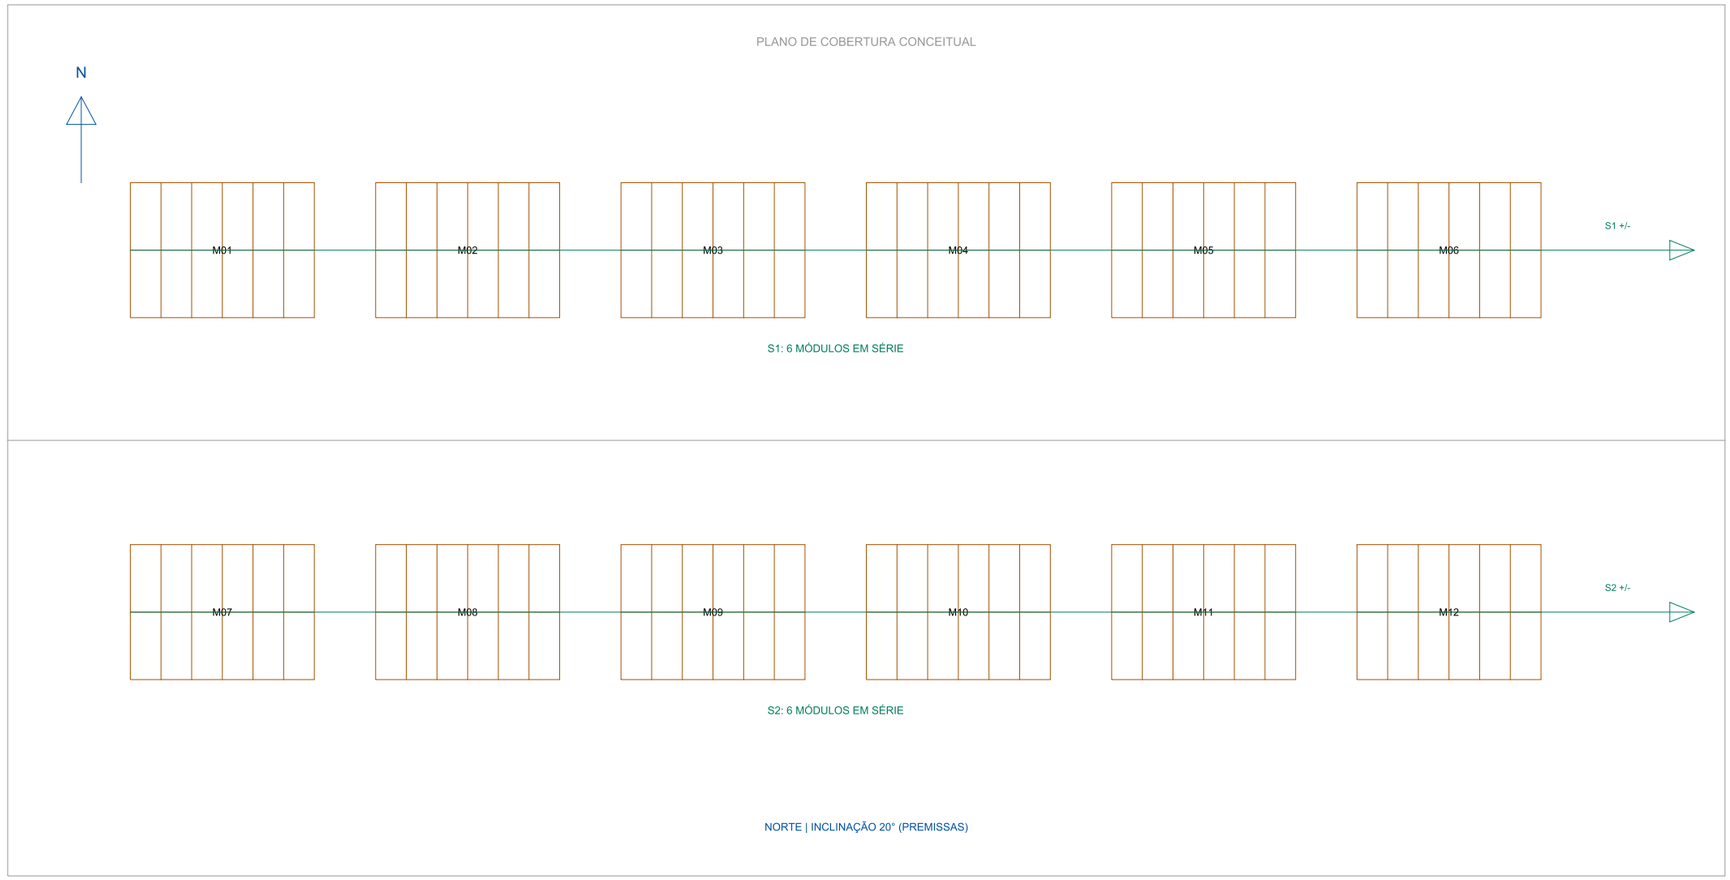

DADO	VALOR
POTÊNCIA CC	6,60 kWp
MÓDULOS	12 x 550 Wp
STRINGS	2 x 6S
Vmp/string	250,8 V
Voc/string	299,4 V
Imp / Isc	13,16 / 13,92 A
Tmin / Tcél	-5 / 70 °C
Irrad. máx.	1.100 W/m²

LIMITES DA DISPOSIÇÃO

Sem levantamento de sombras, estrutura, vento, fixações, impermeabilização, acesso ou afastamentos normativos.

LEGENDA

Amarelo: módulos | Laranja: CC | Verde: PE | S1/S2: strings | MPPT: rastreamento

NOTAS DA PRANCHA

Implantação esquemática, sem levantamento de sombras ou validação estrutural.
Orientação, inclinação, afastamentos e acesso devem ser confirmados no local.

AVISO OBRIGATORIO

Projeto acadêmico e conceitual. Não deve ser utilizado para fabricação, instalação ou execução de serviços sem revisão, dimensionamento e responsabilidade de profissional legalmente habilitado.

REV.	DATA	DESCRICAO	RESP.
02	2026-11-05	ESTUDO DE SENSIBILIDADE 02	R.E.M.M.

PORTFOLIO DE
ENGENHARIA ELETRICA
BASE ACADEMICA REPRODUZIVEL

A3
PAISAGEM

TITULO

DISPOSIÇÃO DOS MÓDULOS

AUTOR	DATA	REV.	PRANCHA
Rogério Eduardo Moreira Menegueli	2026-11-05	02	01/07

ARQUIVO	UNIDADES	ESCALA	FOLHA	STATUS
01_disposicao_modulos.dxf	mm	S/ESC.	A3	CONCEIT.