
DIAGRAMA UNIFILAR DA MICRORREDE

Rede, FV, armazenamento e geracao local em barramento CA comum

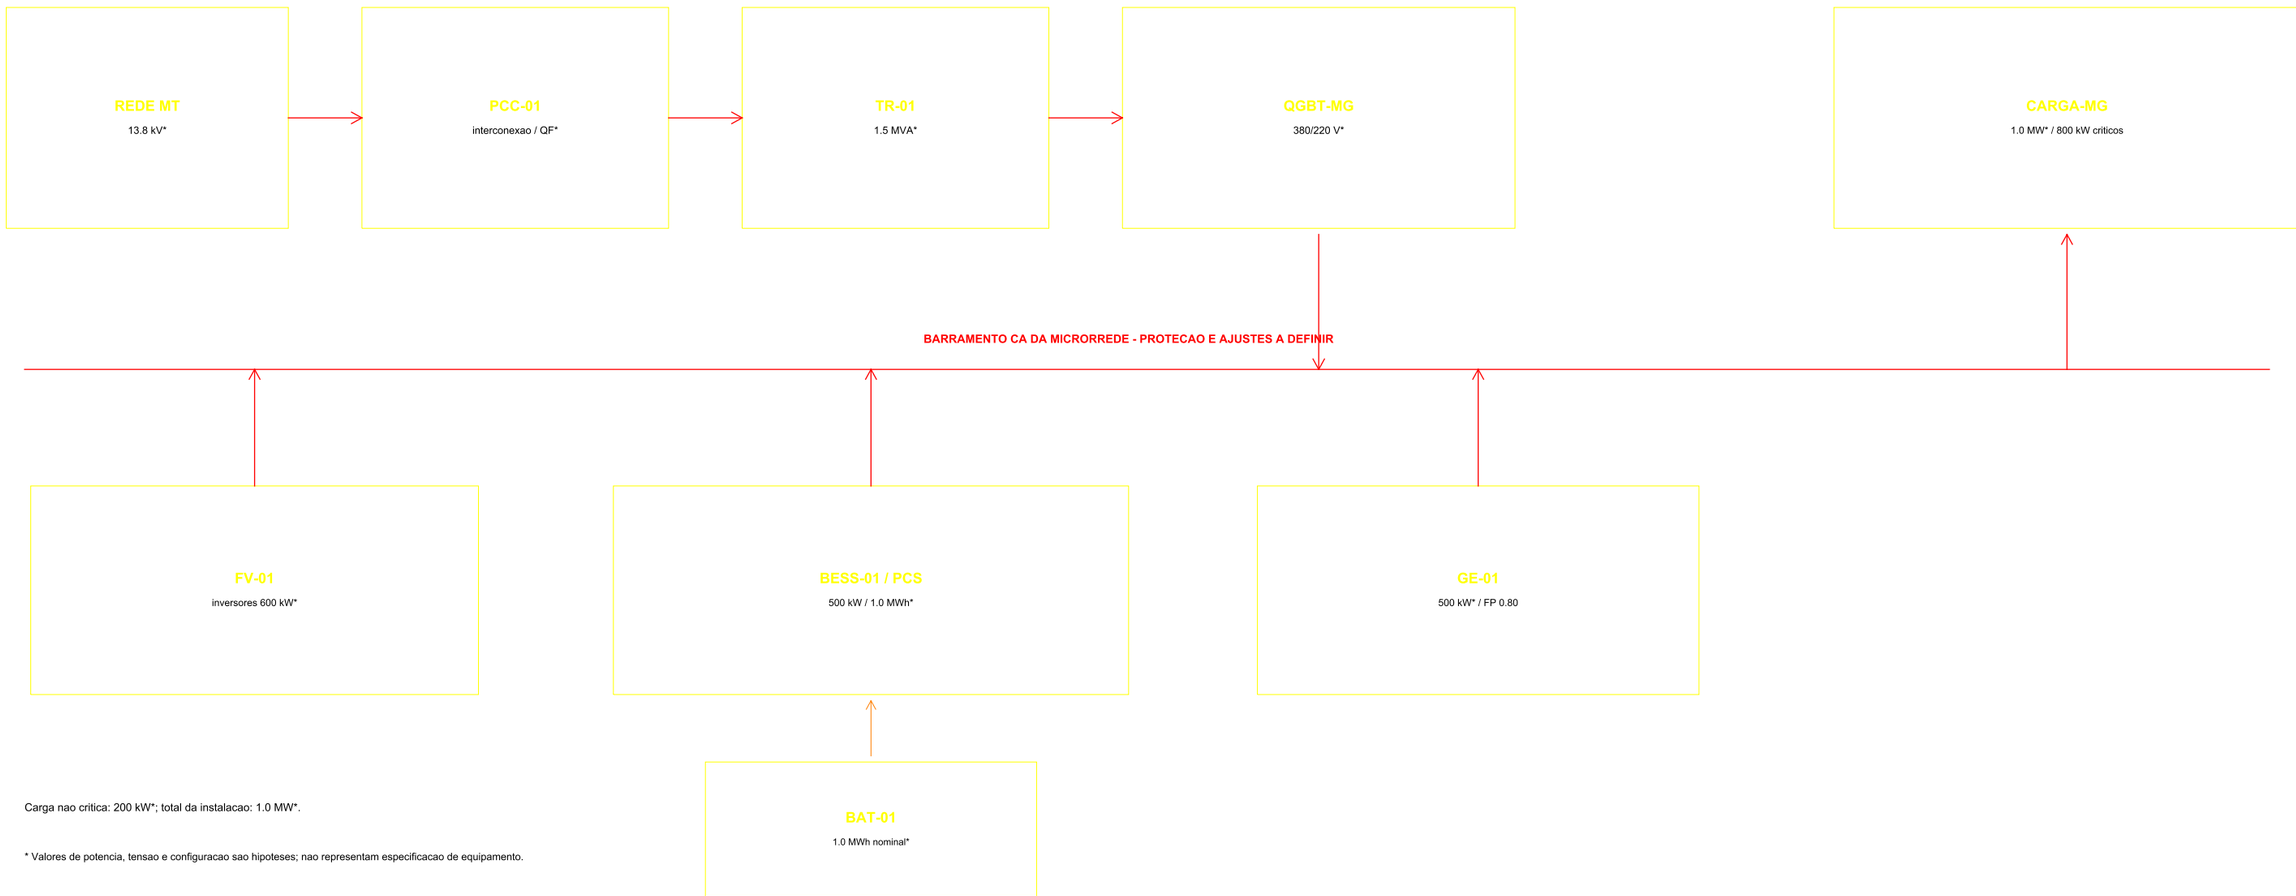

Carga nao critica: 200 kW*; total da instalacao: 1.0 MW*.

* Valores de potencia, tensao e configuracao sao hipoteses; nao representam especificacao de equipamento.

LEGENDA

PCC: ponto de acoplamento comum | FV: fotovoltaico | BESS: armazenamento | GE: grupo gerador | MG: microrrede | kW/kWh nominais assumidos

NOTAS DA PRANCHA

13,8 kV, 380/220 V, cargas e capacidades sao hipoteses de representacao.
Protecao de interconexao, curto-circuito e ajustes dependem de estudos e concessionaria.

AVISO OBRIGATORIO

Projeto acadêmico e conceitual. Não deve ser utilizado para fabricação, instalação ou execução de serviços sem revisão, dimensionamento e responsabilidade de profissional legalmente habilitado.

REV.	DATA	DESCRICAO	RESP.
00	2026-11-06	EMISSAO INICIAL	R.E.M.M.

PORTFOLIO DE
ENGENHARIA ELETRICA
BASE ACADEMICA REPRODUZIVEL

A3
PAISAGEM

TITULO

DIAGRAMA UNIFILAR DA MICRORREDE

AUTOR	DATA	REV.	PRANCHA
Rogério Eduardo Moreira Menegueli	2026-11-06	00	01/03

ARQUIVO	UNIDADES	ESCALA	FOLHA	STATUS
01_unifilar_microrrede.dxf	mm	S/ESC.	A3	CONCEIT.