
A | B | C | D | E | F | G | H

ARQUITETURA DE AUTOMAÇÃO

Potência, controle, segurança e interfaces de processo


5

CAMADA DE POTÊNCIA

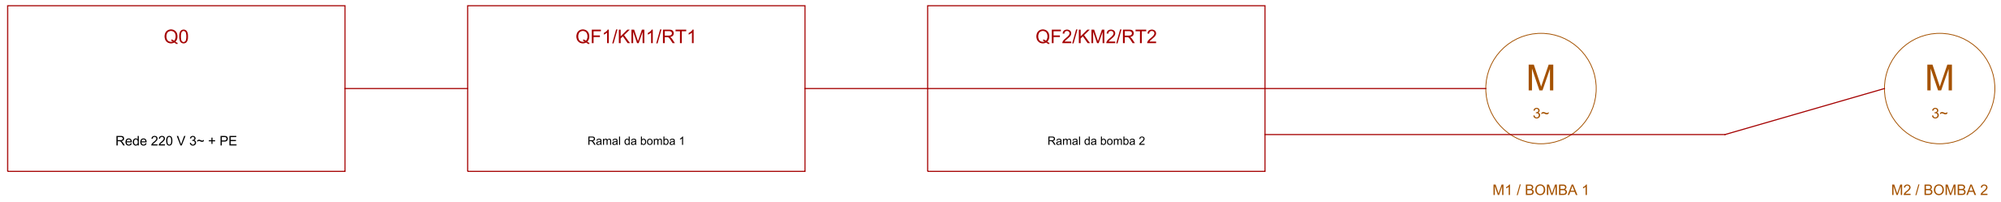

4

CAMADA DE CONTROLE E SEGURANÇA

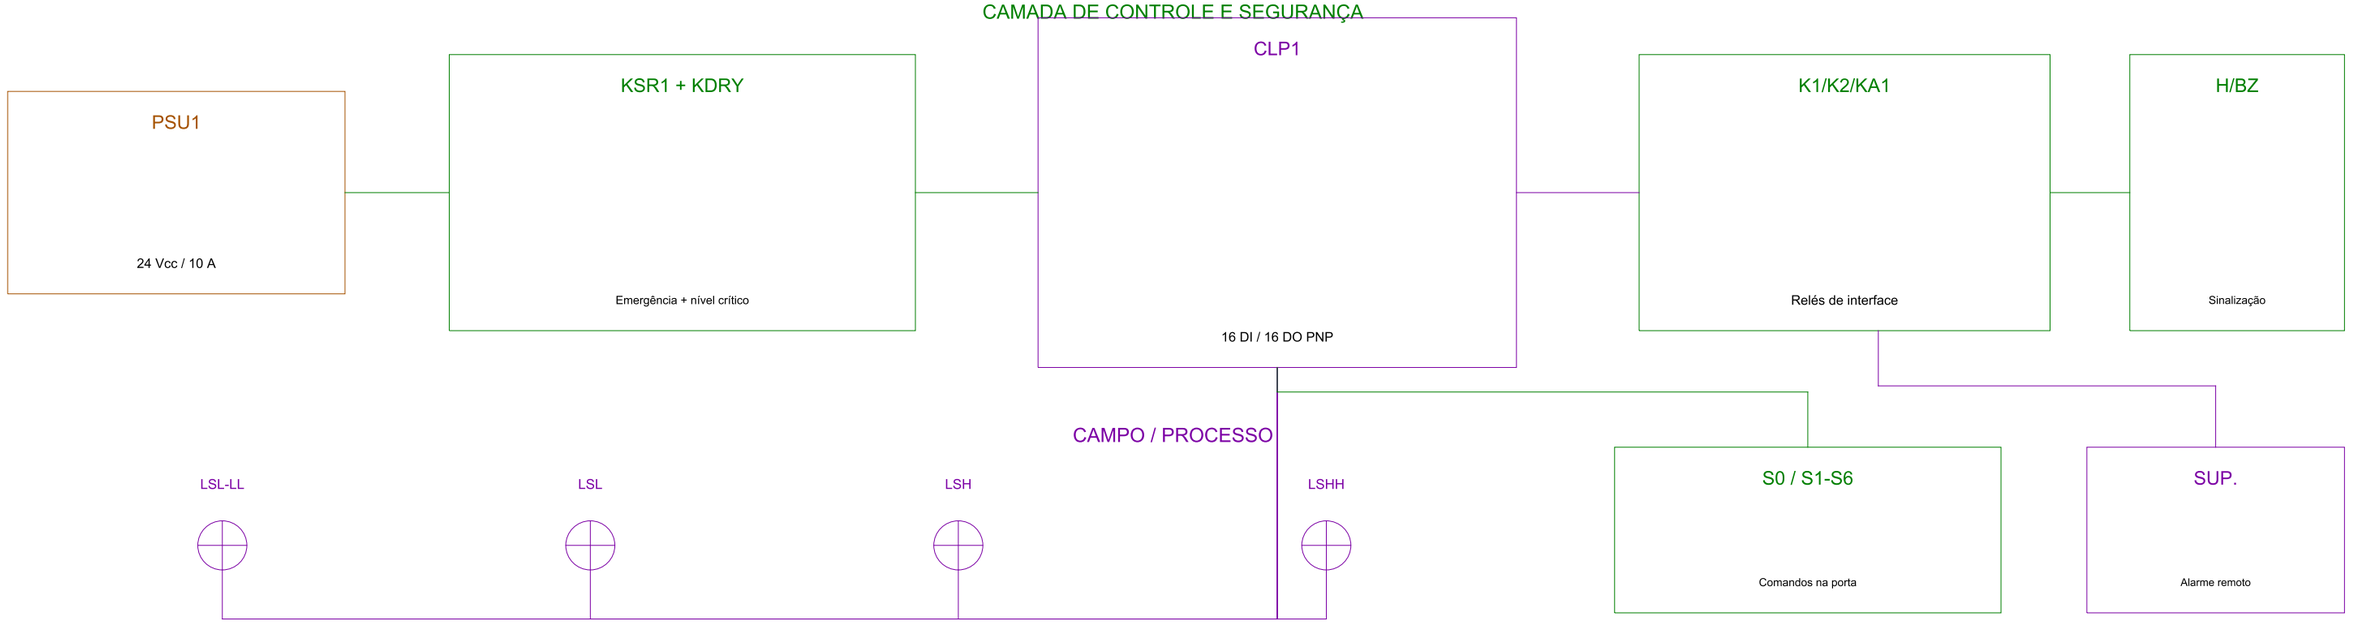

3

2

LEGENDA

QF: proteção | KM: contator | RT: sobrecarga | KSR: segurança | LS: nível

NOTAS DA PRANCHA

Rede assumida 220 V 3~ 60 Hz TN-S. CLP genérico 24 Vcc, 16 DI / 16 DO.
A arquitetura é conceitual e exige análise de risco e dimensionamento final.

1

AVISO OBRIGATÓRIO

Projeto acadêmico e conceitual. Não deve ser utilizado para fabricação, instalação ou execução de serviços sem revisão, dimensionamento e responsabilidade de profissional legalmente habilitado.

REV.	DATA	DESCRIÇÃO	RESP.
05	2026-11-06	ALTERNATIVAS DO PROCESSO	R.E.M.M.

PORTFOLIO DE
ENGENHARIA ELETRICA
BASE ACADEMICA REPRODUZIVEL

A3
PAISAGEM

TITULO

ARQUITETURA DE AUTOMAÇÃO

AUTOR	DATA	REV.	PRANCHA
Rogério Eduardo Moreira Menegueli	2026-11-06	05	01/11

ARQUIVO	UNIDADES	ESCALA	FOLHA	STATUS
01_arquitetura_automacao.dxf	mm	S/ESC.	A3	CONCEIT.