
# INTERLIGAÇÕES DE CAMPO

Painel, reservatório, bombas, emergência e supervisão remota

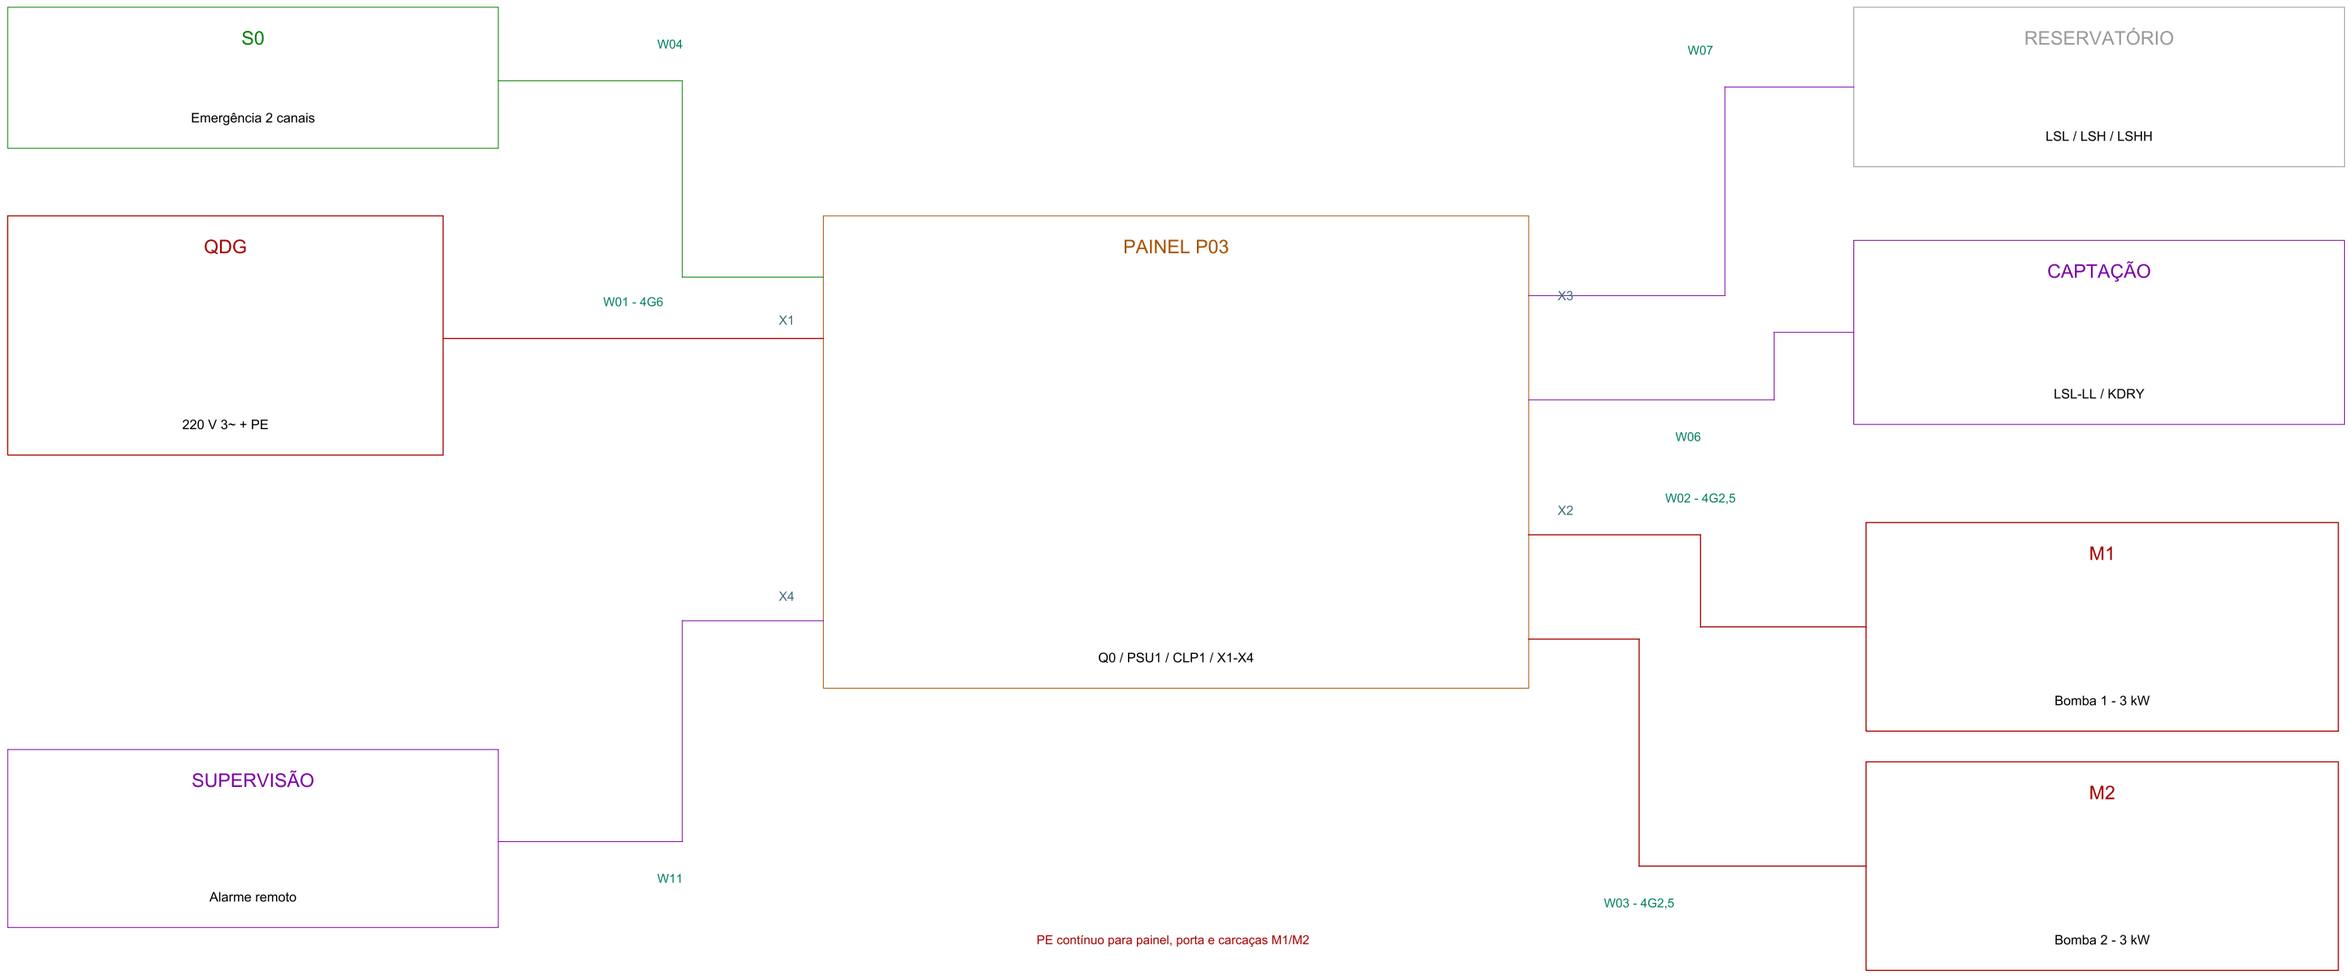


## LEGENDA

Linha cheia: potência | tracejado funcional: controle | LS: nível | PE: proteção

## NOTAS DA PRANCHA

Comprimentos de W01-W12 são premissas. Confirmar rotas, segregação, EMC, queda de tensão, tipo de sensor e equipotencialização após levantamento de campo.

## AVISO OBRIGATÓRIO

Projeto acadêmico e conceitual. Não deve ser utilizado para fabricação, instalação ou execução de serviços sem revisão, dimensionamento e responsabilidade de profissional legalmente habilitado.

| REV. | DATA | DESCRIÇÃO | RESP. |
|---|---|---|---|
| 05 | 2026-11-06 | ALTERNATIVAS DO PROCESSO | R.E.M.M. |

**PORTFOLIO DE**
**ENGENHARIA ELETRICA**
BASE ACADEMICA REPRODUZIVEL

**A3**
PAISAGEM

TITULO

INTERLIGAÇÕES DE CAMPO

| AUTOR | DATA | REV. | PRANCHA |
|---|---|---|---|
| Rogério Eduardo Moreira Menegueli | 2026-11-06 | 05 | 08/11 |

| ARQUIVO | UNIDADES | ESCALA | FOLHA | STATUS |
|---|---|---|---|---|
| 08_interligacoes_campo.dxf | mm | S/ESC. | A3 | CONCEIT. |