
A B C D E F G H

# DIAGRAMA DE BLOCOS

Fonte acadêmica: 0,8-30 Vcc regulados / 0-5 A / 150 W

5

CADEIA PRINCIPAL DE ENERGIA

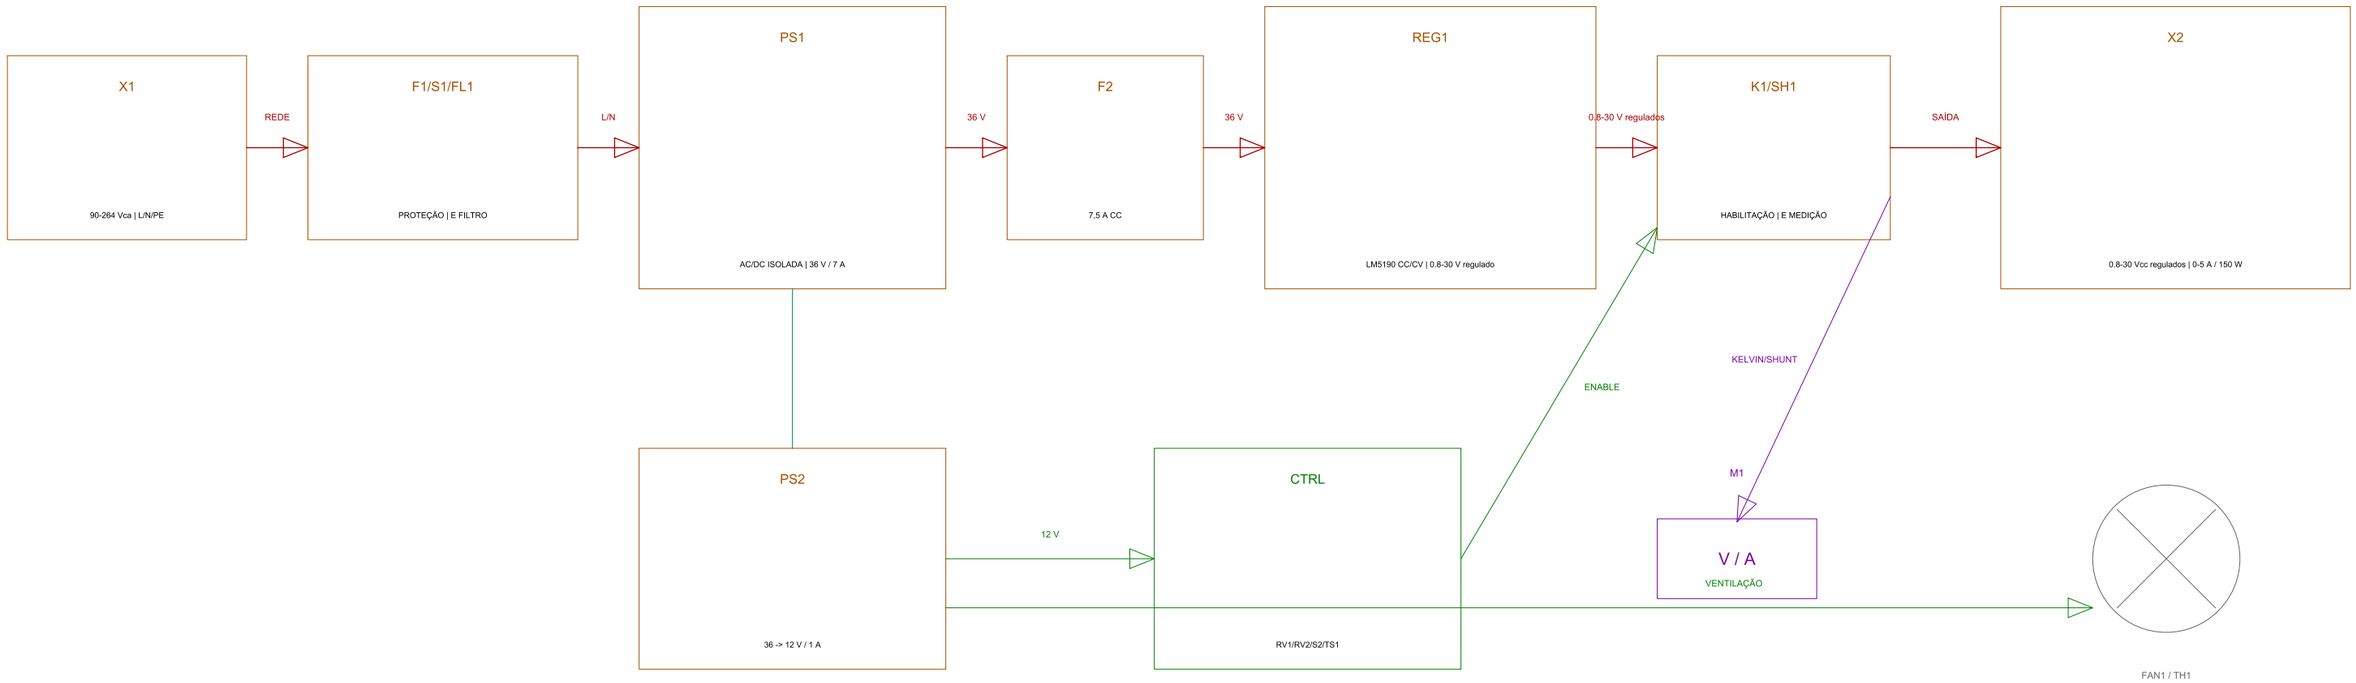


4

3

LIMITES DA ARQUITETURA

PE PERMANENTE NO CHASSI | SAÍDA CC FLUTUANTE | NEGATIVO SEM VÍNCULO INTERNO AO PE

Sem PCB, seleção comercial, ensaios dielétricos, EMC, corrente de toque, falha única, calibração, térmica ou certificação.

2

## LEGENDA

Vermelho: potência | Verde: comando/PE | Magenta: medição | Azul: bornes

## NOTAS DA PRANCHA

Blocos PS1, REG1, PS2 e M1 são especificações funcionais fictícias.
A arquitetura não comprova isolação, segurança, EMC, precisão ou desempenho.

1

## AVISO OBRIGATORIO

Projeto acadêmico e conceitual. Não deve ser utilizado para fabricação, instalação ou execução de serviços sem revisão, dimensionamento e responsabilidade de profissional legalmente habilitado.

| REV. | DATA | DESCRICAO | RESP. |
|---|---|---|---|
| 03 | 2026-11-05 | TOPOLOGIA E PRE-DIMENSIONAMENTO | R.E.M.M. |

**PORTFOLIO DE**
**ENGENHARIA ELETRICA**
BASE ACADEMICA REPRODUZIVEL

**A3**
PAISAGEM

TITULO

DIAGRAMA DE BLOCOS

| AUTOR | DATA | REV. | PRANCHA |
|---|---|---|---|
| Rogério Eduardo Moreira Menegueli | 2026-11-05 | 03 | 01/09 |

| ARQUIVO | UNIDADES | ESCALA | FOLHA | STATUS |
|---|---|---|---|---|
| 01_diagrama_blocos.dxf | mm | S/ESC. | A3 | CONCEIT. |