
DIAGRAMA ELÉTRICO

Entrada, proteção, conversão, regulação, medição e comando térmico

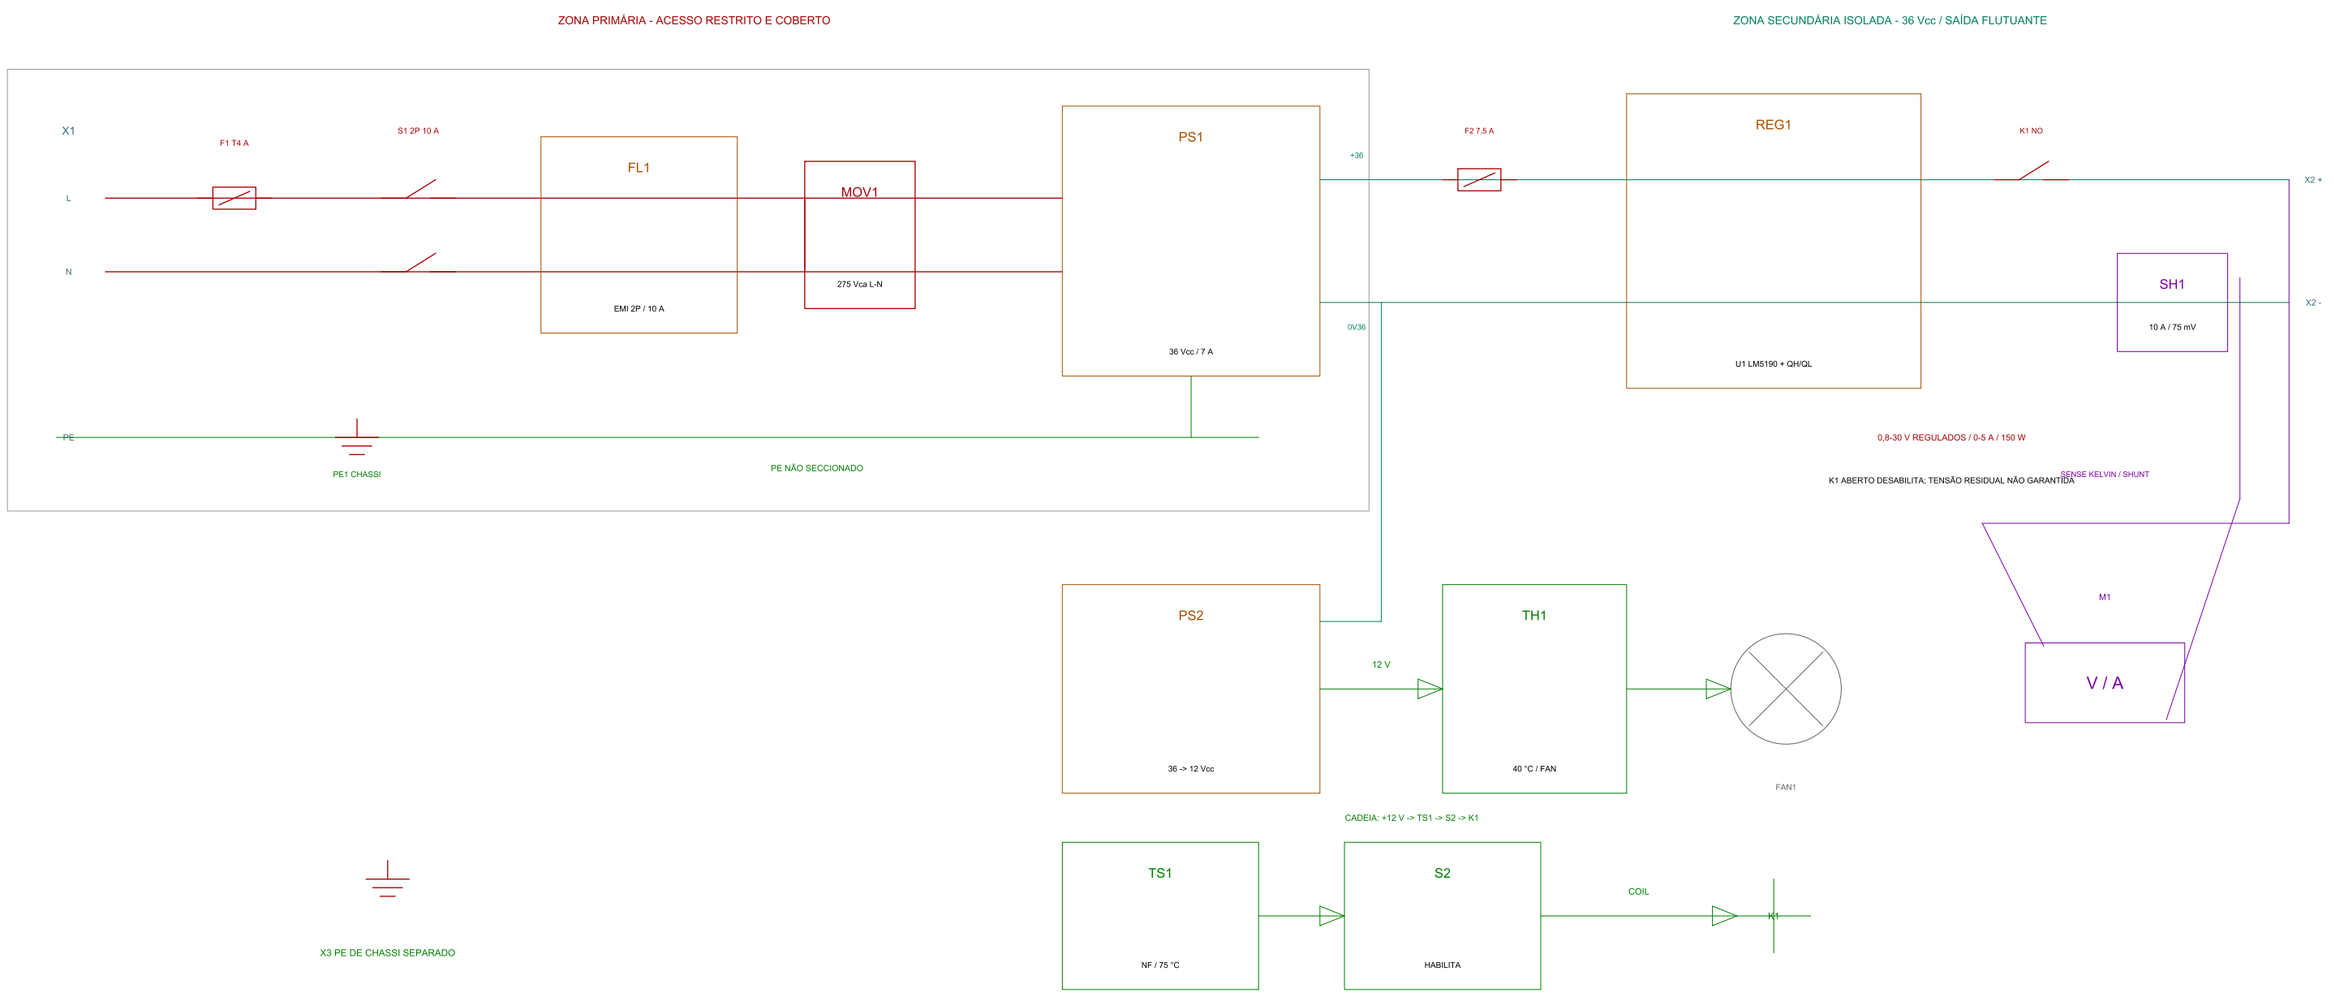

LEGENDA

F: fusível | S: chave/comando | PS: fonte | REG: regulador | K: relé | X: borne

NOTAS DA PRANCHA

PE é permanente e não passa por chave ou fusível. Saída CC sem ligação interna ao PE.
K1 isolado não prova tensão zero; o estudo paramétrico de descarga está na prancha 09.

AVISO OBRIGATORIO

Projeto acadêmico e conceitual. Não deve ser utilizado para fabricação, instalação ou execução de serviços sem revisão, dimensionamento e responsabilidade de profissional legalmente habilitado.

REV.	DATA	DESCRICAO	RESP.
03	2026-11-05	TOPOLOGIA E PRE-DIMENSIONAMENTO	R.E.M.M.

PORTFOLIO DE
ENGENHARIA ELETRICA
BASE ACADEMICA REPRODUZIVEL

A3
PAISAGEM

TITULO

DIAGRAMA ELÉTRICO

AUTOR	DATA	REV.	PRANCHA
Rogério Eduardo Moreira Menegueli	2026-11-05	03	02/09

ARQUIVO	UNIDADES	ESCALA	FOLHA	STATUS
02_diagrama_eletrico.dxf	mm	S/ESC.	A3	CONCEIT.