
DIAGRAMA UNIFILAR DO CCM

Integração de partida direta, reversão e inversor de frequência

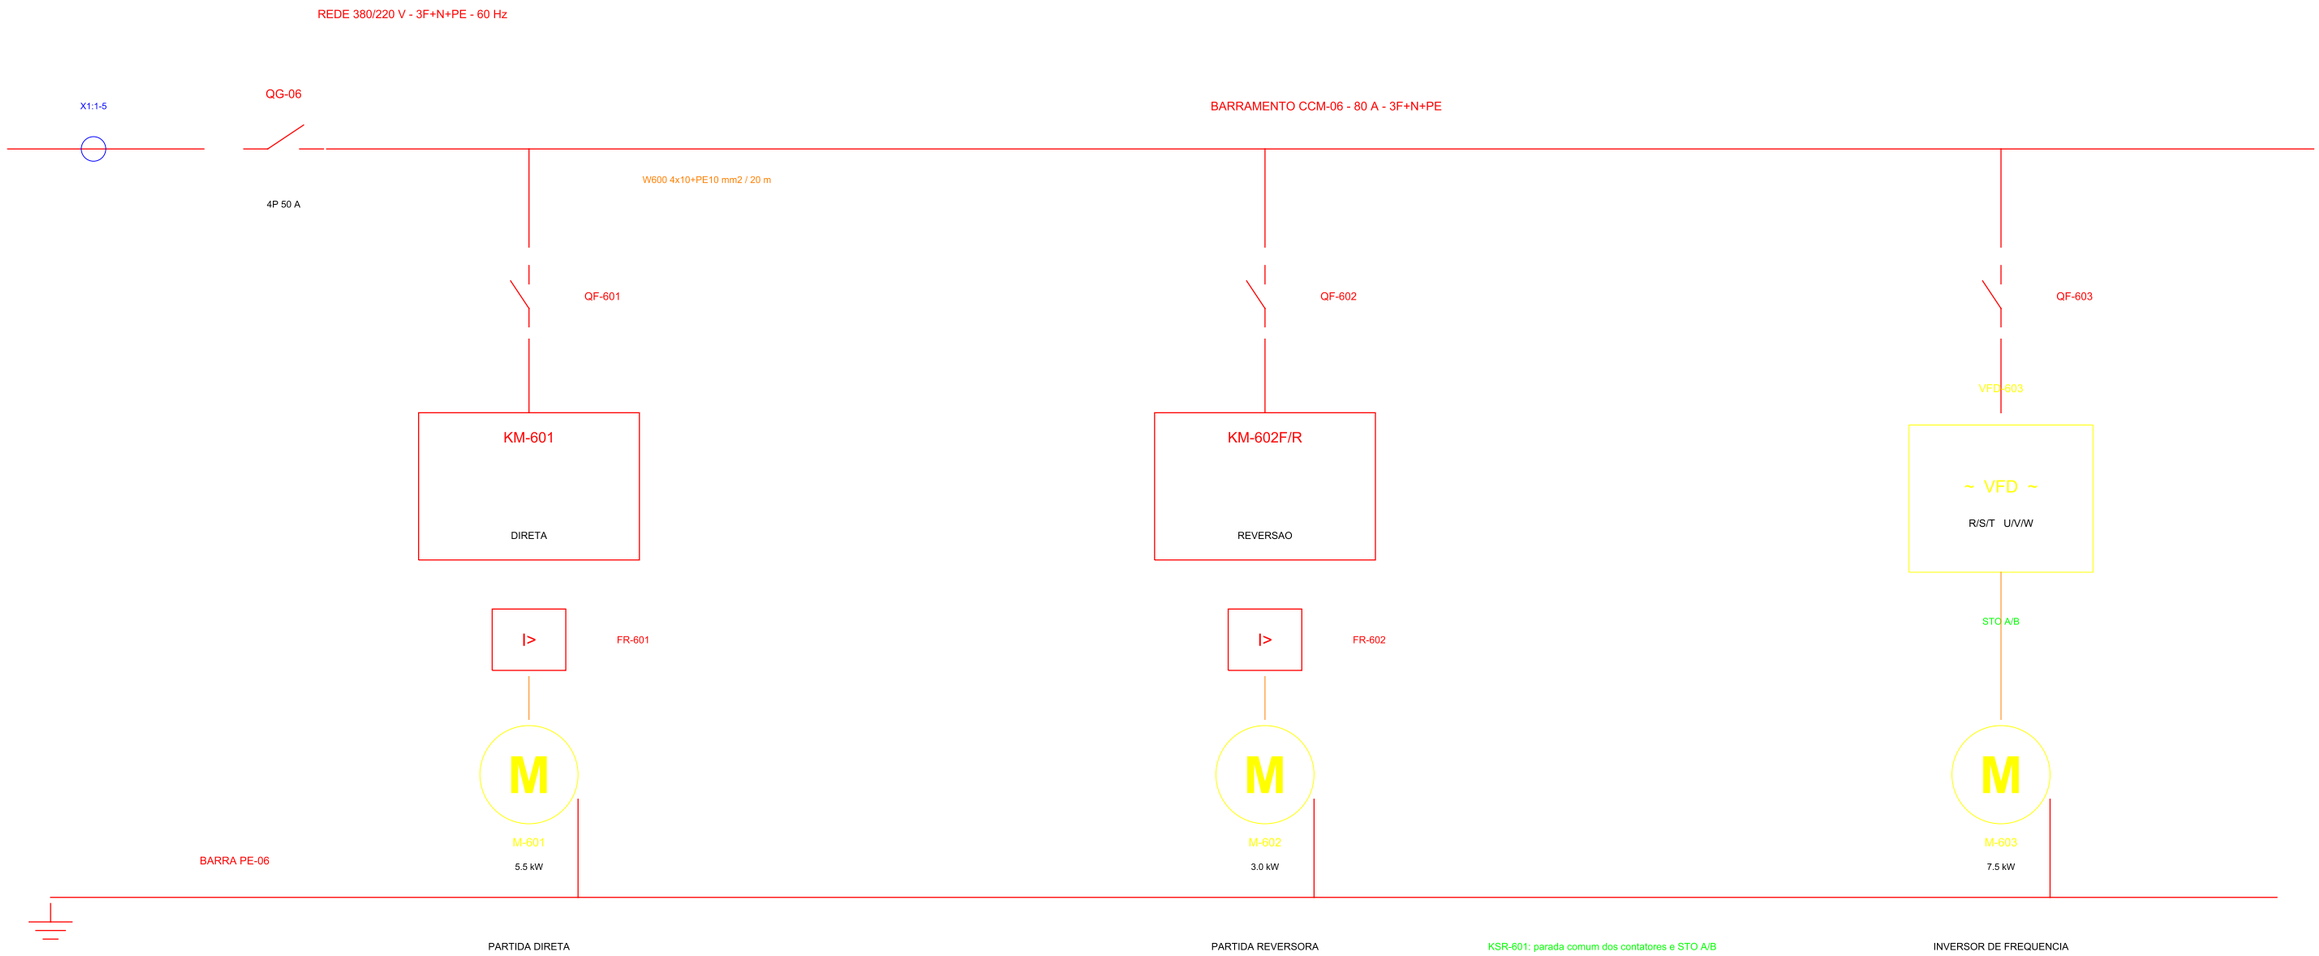

LEGENDA

Q: proteção | KM: contator | FR: sobrecarga | VFD: inversor | M: motor | PE: proteção

NOTAS DA PRANCHA

Rede assumida: 380/220 V, 3F+N+PE, 60 Hz, TN-S. Icc presumida: 6 kA.
Seleção final de proteção, curto-circuito e coordenação depende de estudo executivo.

AVISO OBRIGATORIO

Projeto acadêmico e conceitual. Não deve ser utilizado para fabricação, instalação ou execução de serviços sem revisão, dimensionamento e responsabilidade de profissional legalmente habilitado.

REV.	DATA	DESCRICAO	RESP.
00	2026-09-09	EMISSAO INICIAL DO PROJETO 06	R.E.M.M.

PORTFOLIO DE
ENGENHARIA ELETRICA
BASE ACADEMICA REPRODUZIVEL

A3
PAISAGEM

TITULO

DIAGRAMA UNIFILAR DO CCM

AUTOR	DATA	REV.	PRANCHA
Rogério Eduardo Moreira Menegueli	2026-09-09	00	01/07

ARQUIVO	UNIDADES	ESCALA	FOLHA	STATUS
01_diagrama_unifilar_ccm.dxf	mm	S/ESC.	A3	CONCEIT.