
ARQUITETURA DA REDE

Supervisão, controle, remotas, instrumentos e distribuição 24 Vcc

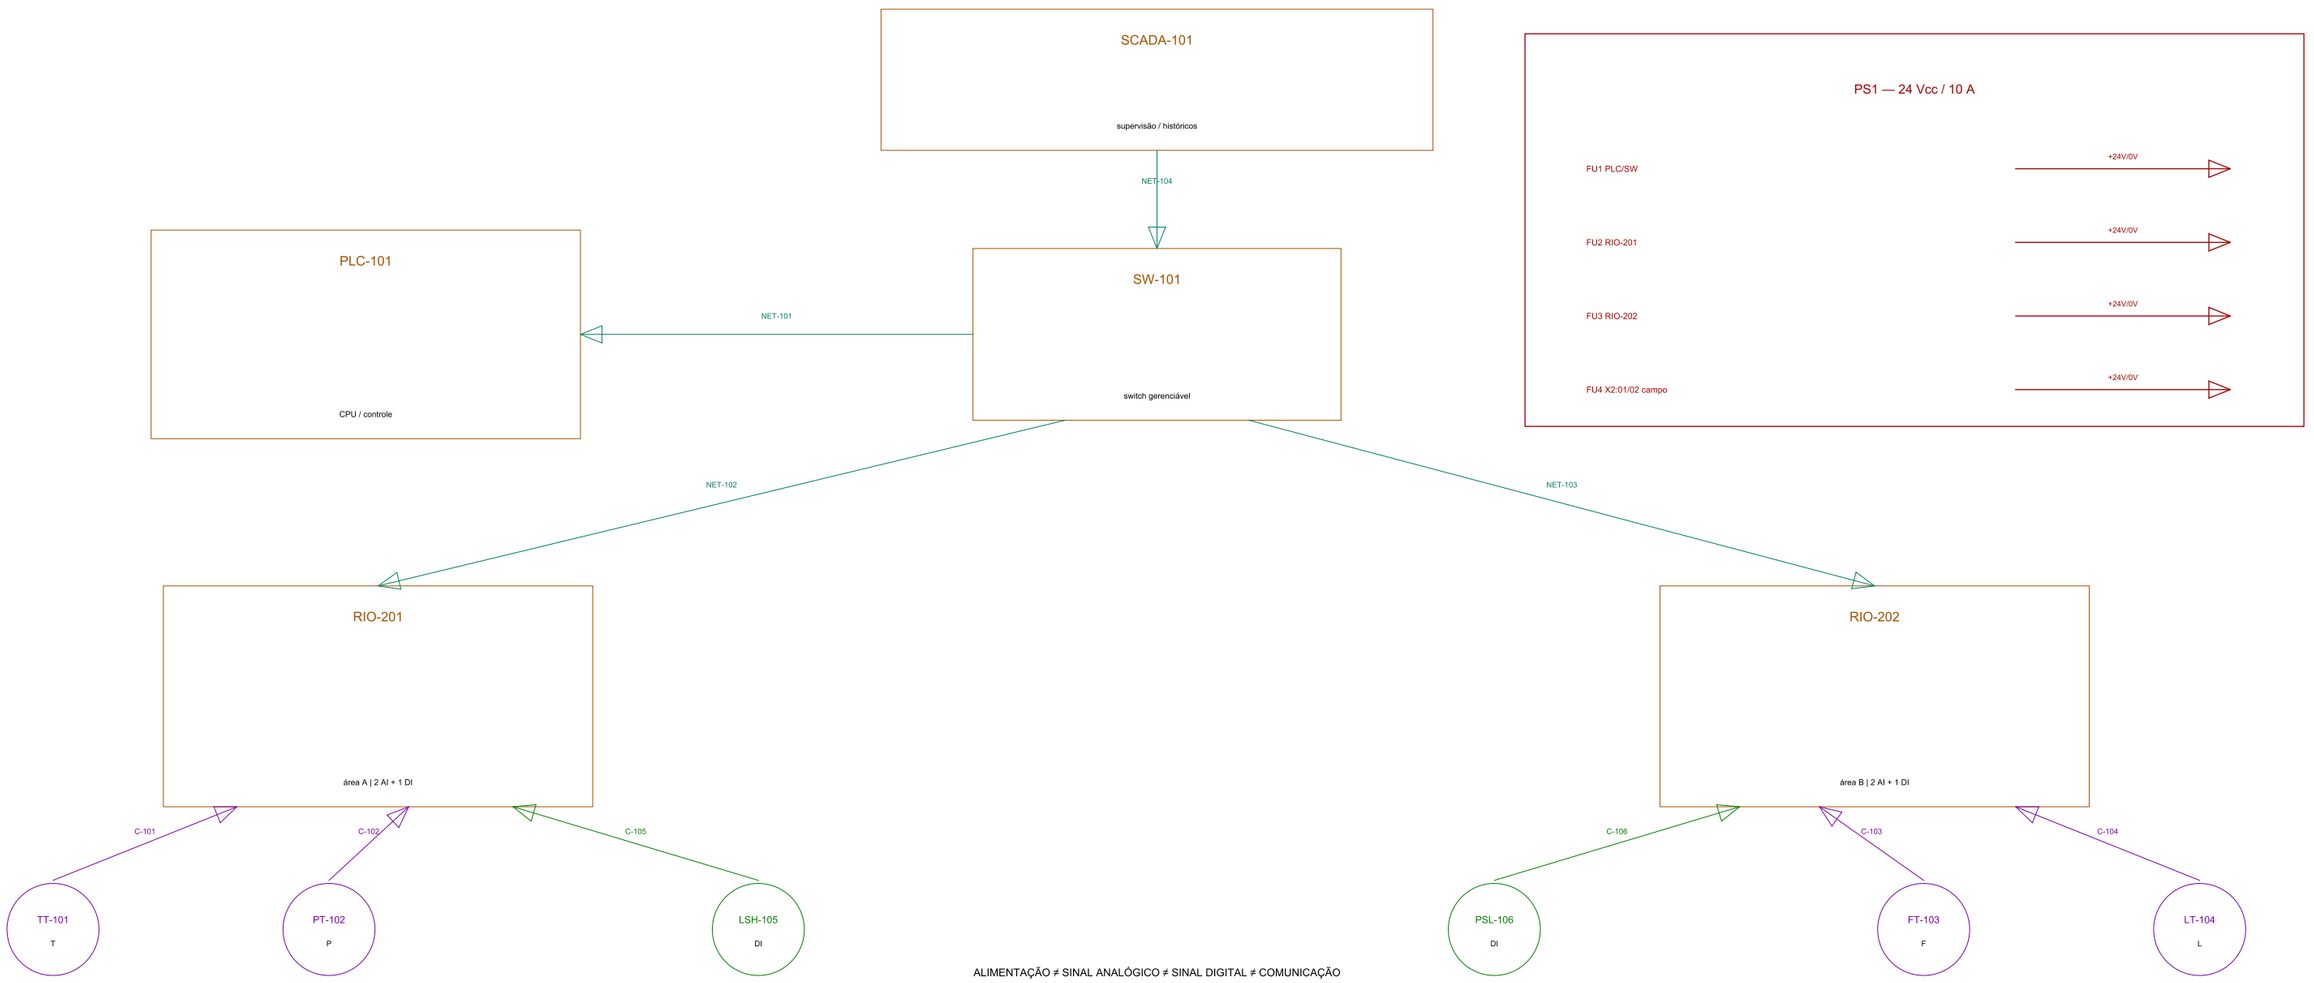

ALIMENTAÇÃO ≠ SINAL ANALÓGICO ≠ SINAL DIGITAL ≠ COMUNICAÇÃO

LEGENDA

Vermelho: 24 Vcc | Magenta: 4-20 mA | Verde: digital | Laranja: comunicação

NOTAS DA PRANCHA

Topologia acadêmica genérica; protocolo, fabricante e disponibilidade não foram selecionados.
Separar alimentação, sinais de campo e comunicação em rotas compatíveis com o estudo de EMC.
FU4 representa a distribuição comum das malhas/sensores em X2:01/02; seleção e coordenação pendentes.

AVISO OBRIGATÓRIO

Projeto acadêmico e conceitual. Não deve ser utilizado para fabricação, instalação ou execução de serviços sem revisão, dimensionamento e responsabilidade de profissional legalmente habilitado.

REV.	DATA	DESCRIÇÃO	RESP.
05	2026-11-06	INTERLIGACAO RIO	R.E.M.M.

PORTFOLIO DE
ENGENHARIA ELETRICA
BASE ACADEMICA REPRODUZIVEL

A3
PAISAGEM

TITULO

ARQUITETURA DA REDE

AUTOR	DATA	REV.	PRANCHA
Rogério Eduardo Moreira Menegueli	2026-11-06	05	01/10

ARQUIVO	UNIDADES	ESCALA	FOLHA	STATUS
01_arquitetura_rede.dxf	mm	S/ESC.	A3	CONCEIT.