
TOPOLOGIA DE COMUNICAÇÃO

Ethernet industrial acadêmica em estrela com switch gerenciável

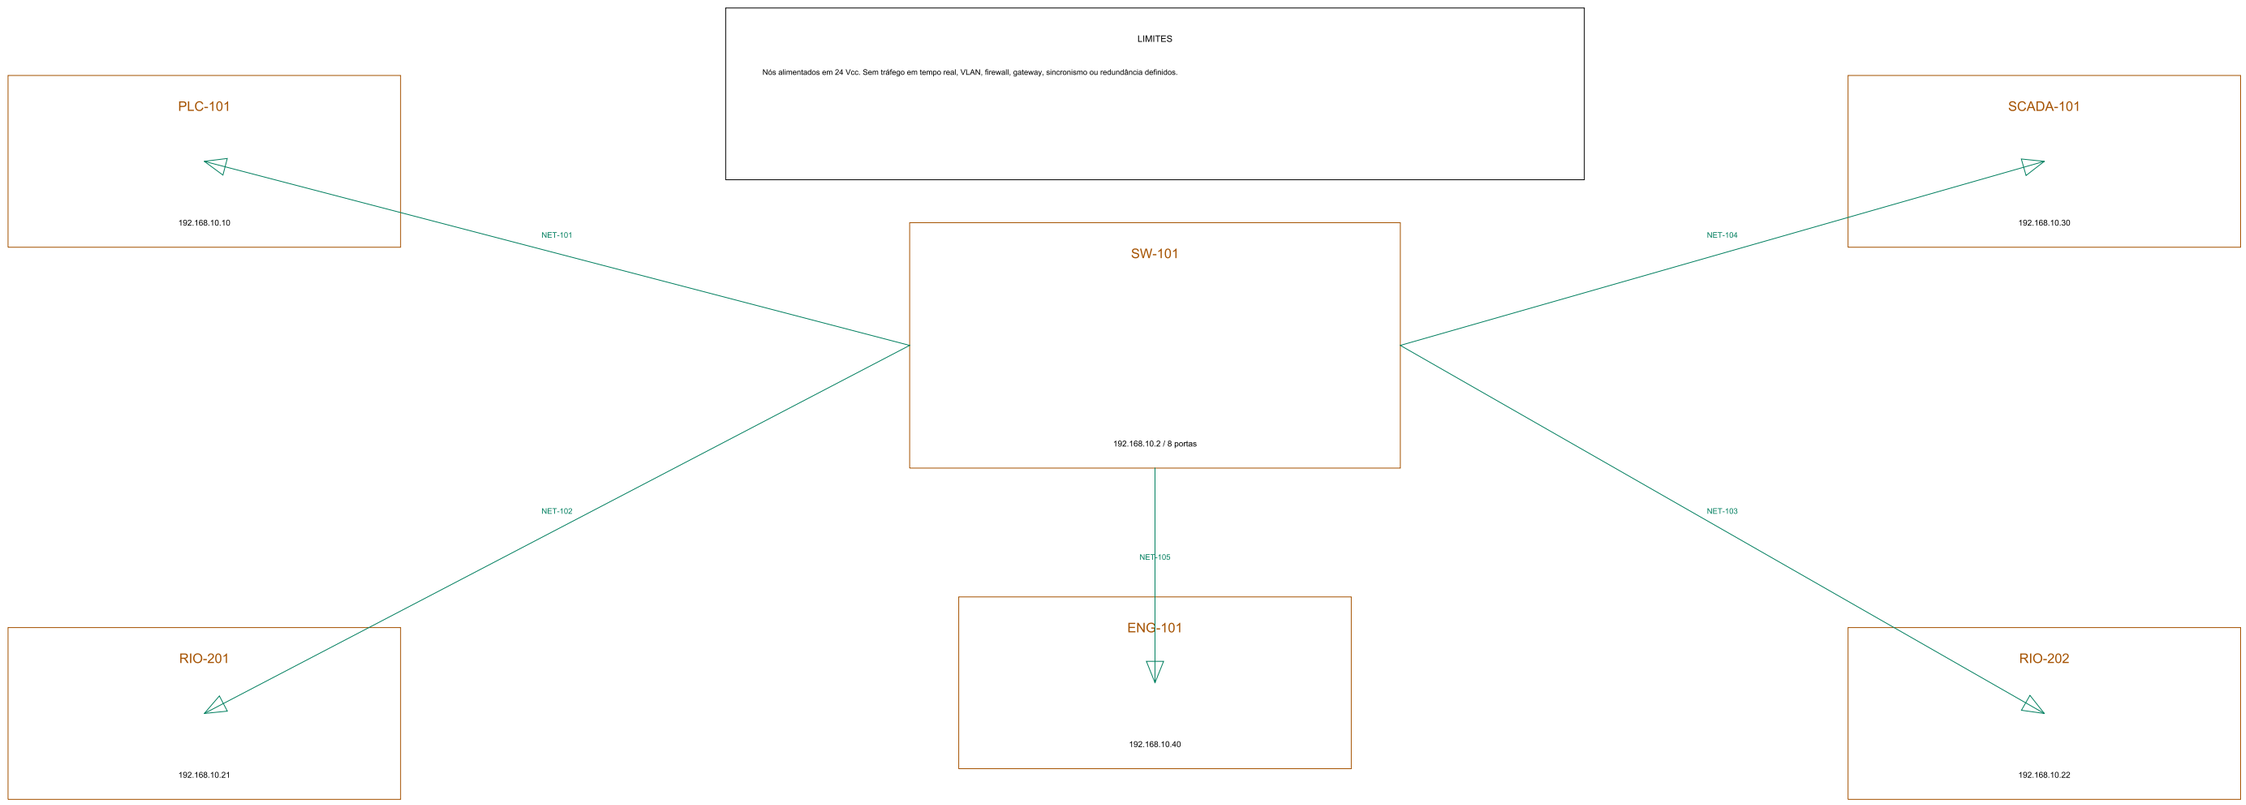

NÓ	ENDEREÇO	MÁSCARA	PORTA	PAPEL
PLC-101	192.168.10.10	/24	SW-101/P1	controlador
RIO-201	192.168.10.21	/24	SW-101/P2	remota área A
RIO-202	192.168.10.22	/24	SW-101/P3	remota área B
SCADA-101	192.168.10.30	/24	SW-101/P4	supervisão
ENG-101	192.168.10.40	/24	SW-101/P5	engenharia temporária

LEGENDA

Linha laranja: Ethernet industrial | NET-xxx: identificação do enlace | /24: máscara 255.255.255.0

NOTAS DA PRANCHA

A comunicação transporta quadros e diagnósticos, não a energia nem o valor 4-20 mA.
Endereços são premissas de documentação; VLAN, protocolo e redundância exigem projeto posterior.

AVISO OBRIGATÓRIO

Projeto acadêmico e conceitual. Não deve ser utilizado para fabricação, instalação ou execução de serviços sem revisão, dimensionamento e responsabilidade de profissional legalmente habilitado.

REV.	DATA	DESCRIÇÃO	RESP.
05	2026-11-06	INTERLIGACAO RIO	R.E.M.M.

PORTFOLIO DE
ENGENHARIA ELETRICA
BASE ACADEMICA REPRODUZIVEL

A3
PAISAGEM

TITULO

TOPOLOGIA DE COMUNICAÇÃO

AUTOR	DATA	REV.	PRANCHA
Rogério Eduardo Moreira Menegueli	2026-11-06	05	04/10

ARQUIVO	UNIDADES	ESCALA	FOLHA	STATUS
04_topologia_comunicacao.dxf	mm	S/ESC.	A3	CONCEIT.