
LAYOUT DOS EQUIPAMENTOS

Telhado, parede técnica, rotas segregadas e ponto de conexão

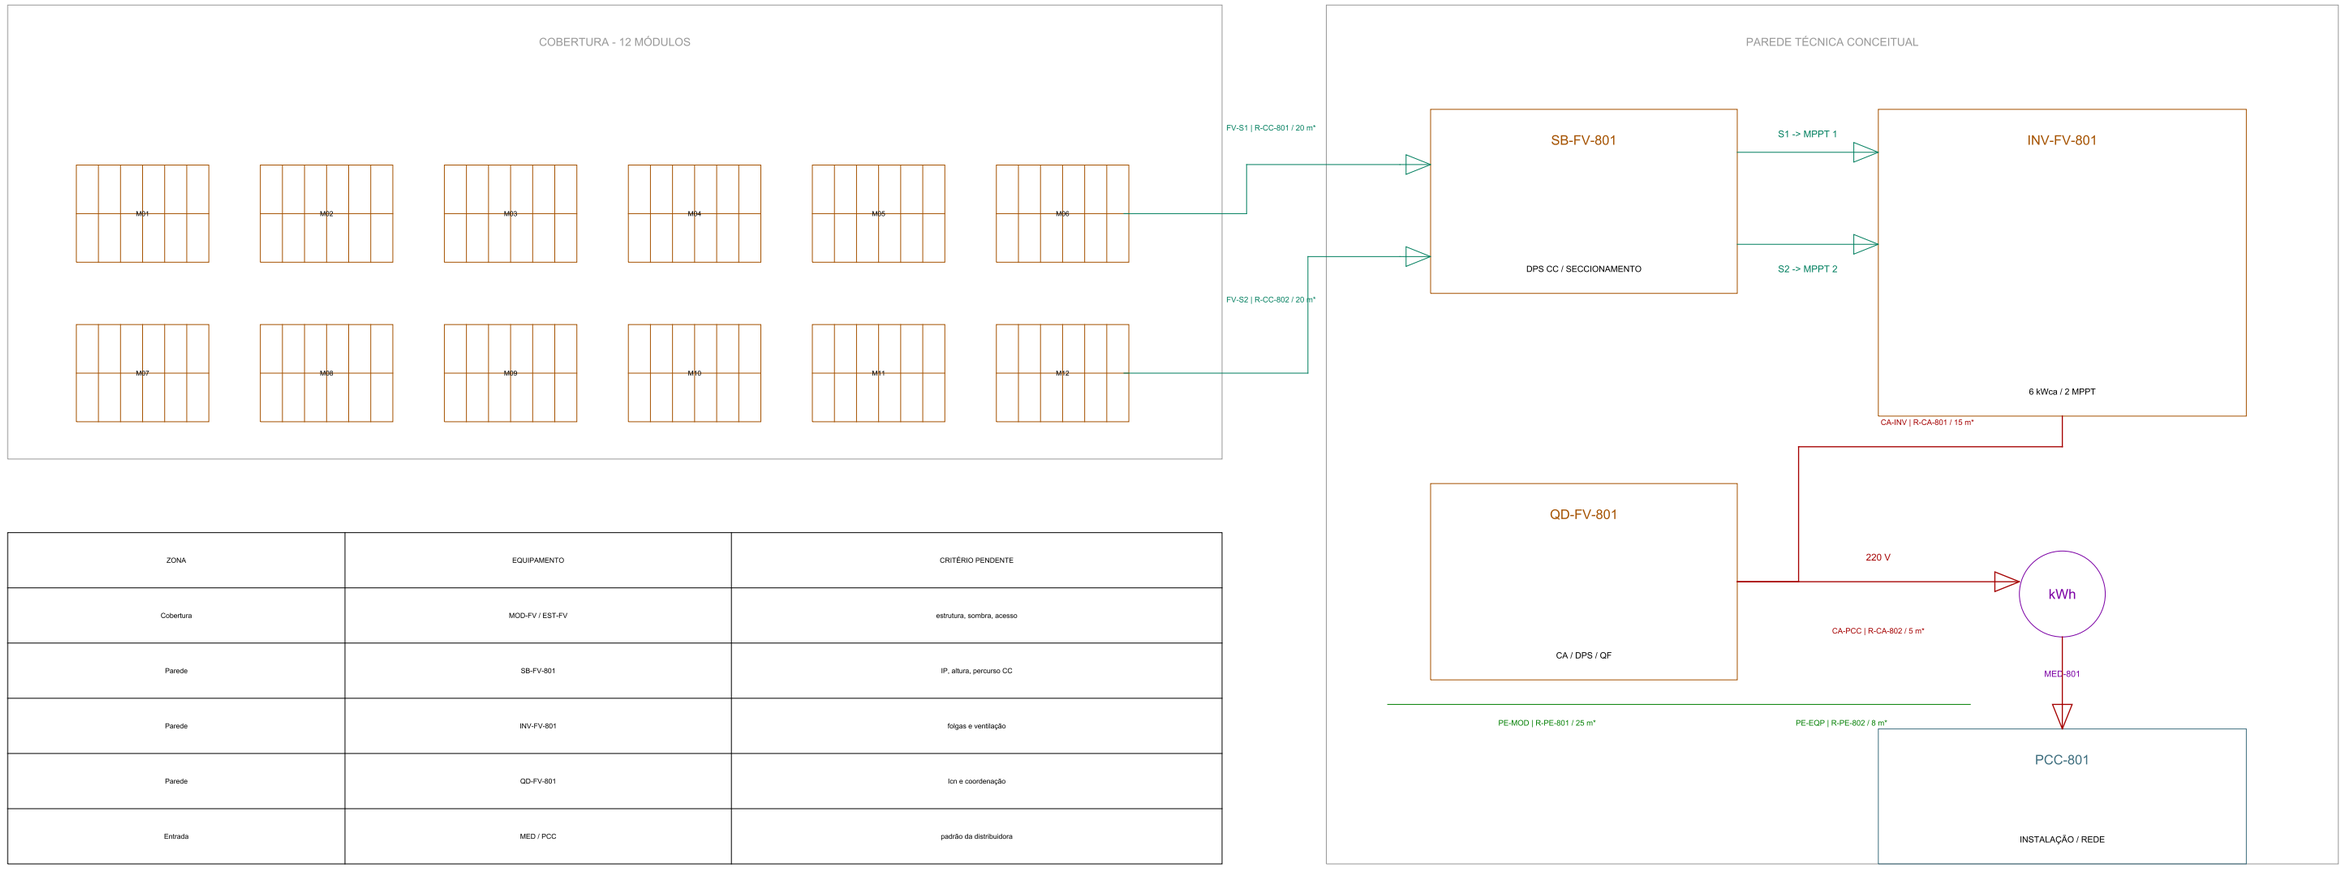

ZONA	EQUIPAMENTO	CRITÉRIO PENDENTE
Cobertura	MOD-FV / EST-FV	estrutura, sombra, acesso
Parede	SB-FV-801	IP, altura, percurso CC
Parede	INV-FV-801	folgas e ventilação
Parede	QD-FV-801	Icn e coordenação
Entrada	MED / PCC	padrão da distribuidora

LEGENDA

Turquesa: CC | Vermelho: CA | Verde: PE | Cinza: arquitetura | * comprimento assumido

NOTAS DA PRANCHA

Posições e folgas são propostas, não instruções de montagem.
Comprimentos indicados são assumidos, não medidos; trajetos não representam imóvel levantado.
Validar acesso, ventilação, IP, raios de curvatura, estrutura e padrão da distribuidora.

AVISO OBRIGATORIO

Projeto acadêmico e conceitual. Não deve ser utilizado para fabricação, instalação ou execução de serviços sem revisão, dimensionamento e responsabilidade de profissional legalmente habilitado.

REV.	DATA	DESCRICAO	RESP.
04	2026-11-06	ROTAS CC/CA RASTREÁVEIS	R.E.M.M.

PORTFOLIO DE
ENGENHARIA ELETRICA
BASE ACADEMICA REPRODUZIVEL

A3
PAISAGEM

TITULO

LAYOUT DOS EQUIPAMENTOS

AUTOR	DATA	REV.	PRANCHA
Rogério Eduardo Moreira Menegueli	2026-11-06	04	06/08

ARQUIVO	UNIDADES	ESCALA	FOLHA	STATUS
06_layout_equipamentos.dxf	mm	S/ESC.	A3	CONCEIT.