
A | B | C | D | E | F | G | H

# ARQUITETURA DE AUTOMAÇÃO

Potência, controle, segurança e interfaces de processo


5

## CAMADA DE POTÊNCIA

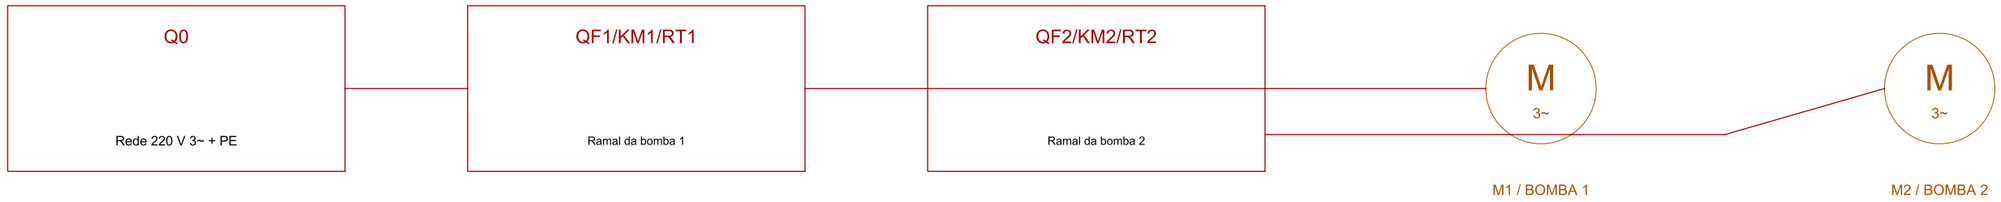


4

## CAMADA DE CONTROLE E SEGURANÇA

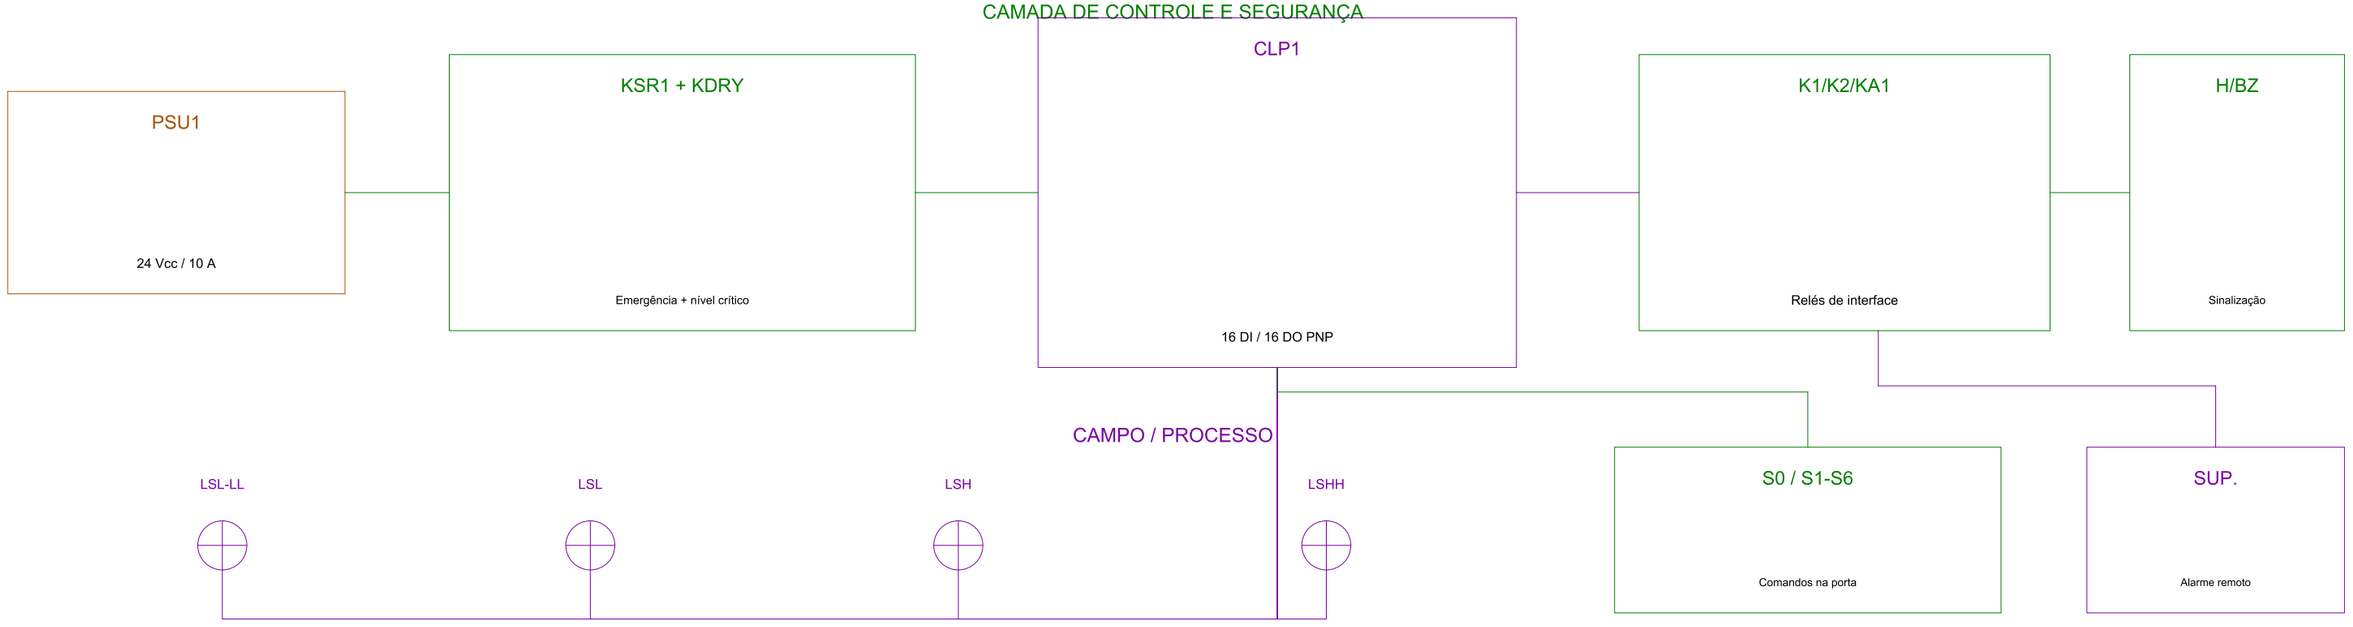


3

2

### LEGENDA

QF: proteção | KM: contator | RT: sobrecarga | KSR: segurança | LS: nível

### NOTAS DA PRANCHA

Rede assumida 220 V 3~ 60 Hz TN-S. CLP genérico 24 Vcc, 16 DI / 16 DO.
A arquitetura é conceitual e exige análise de risco e dimensionamento final.

1

### AVISO OBRIGATÓRIO

Projeto acadêmico e conceitual. Não deve ser utilizado para fabricação, instalação ou execução de serviços sem revisão, dimensionamento e responsabilidade de profissional legalmente habilitado.

| REV. | DATA | DESCRIÇÃO | RESP. |
|---|---|---|---|
| 04 | 2026-11-06 | PLANO DE VERIFICAÇÃO | R.E.M.M. |

**PORTFOLIO DE**
**ENGENHARIA ELETRICA**
BASE ACADEMICA REPRODUZIVEL

**A3**
PAISAGEM

TITULO

ARQUITETURA DE AUTOMAÇÃO

| AUTOR | DATA | REV. | PRANCHA |
|---|---|---|---|
| Rogério Eduardo Moreira Menegueli | 2026-11-06 | 04 | 01/10 |

| ARQUIVO | UNIDADES | ESCALA | FOLHA | STATUS |
|---|---|---|---|---|
| 01_arquitetura_automacao.dxf | mm | S/ESC. | A3 | CONCEIT. |