
# FLUXOGRAMA DO PROCESSO

Enchimento de TK-101 por P-101 com demanda variável

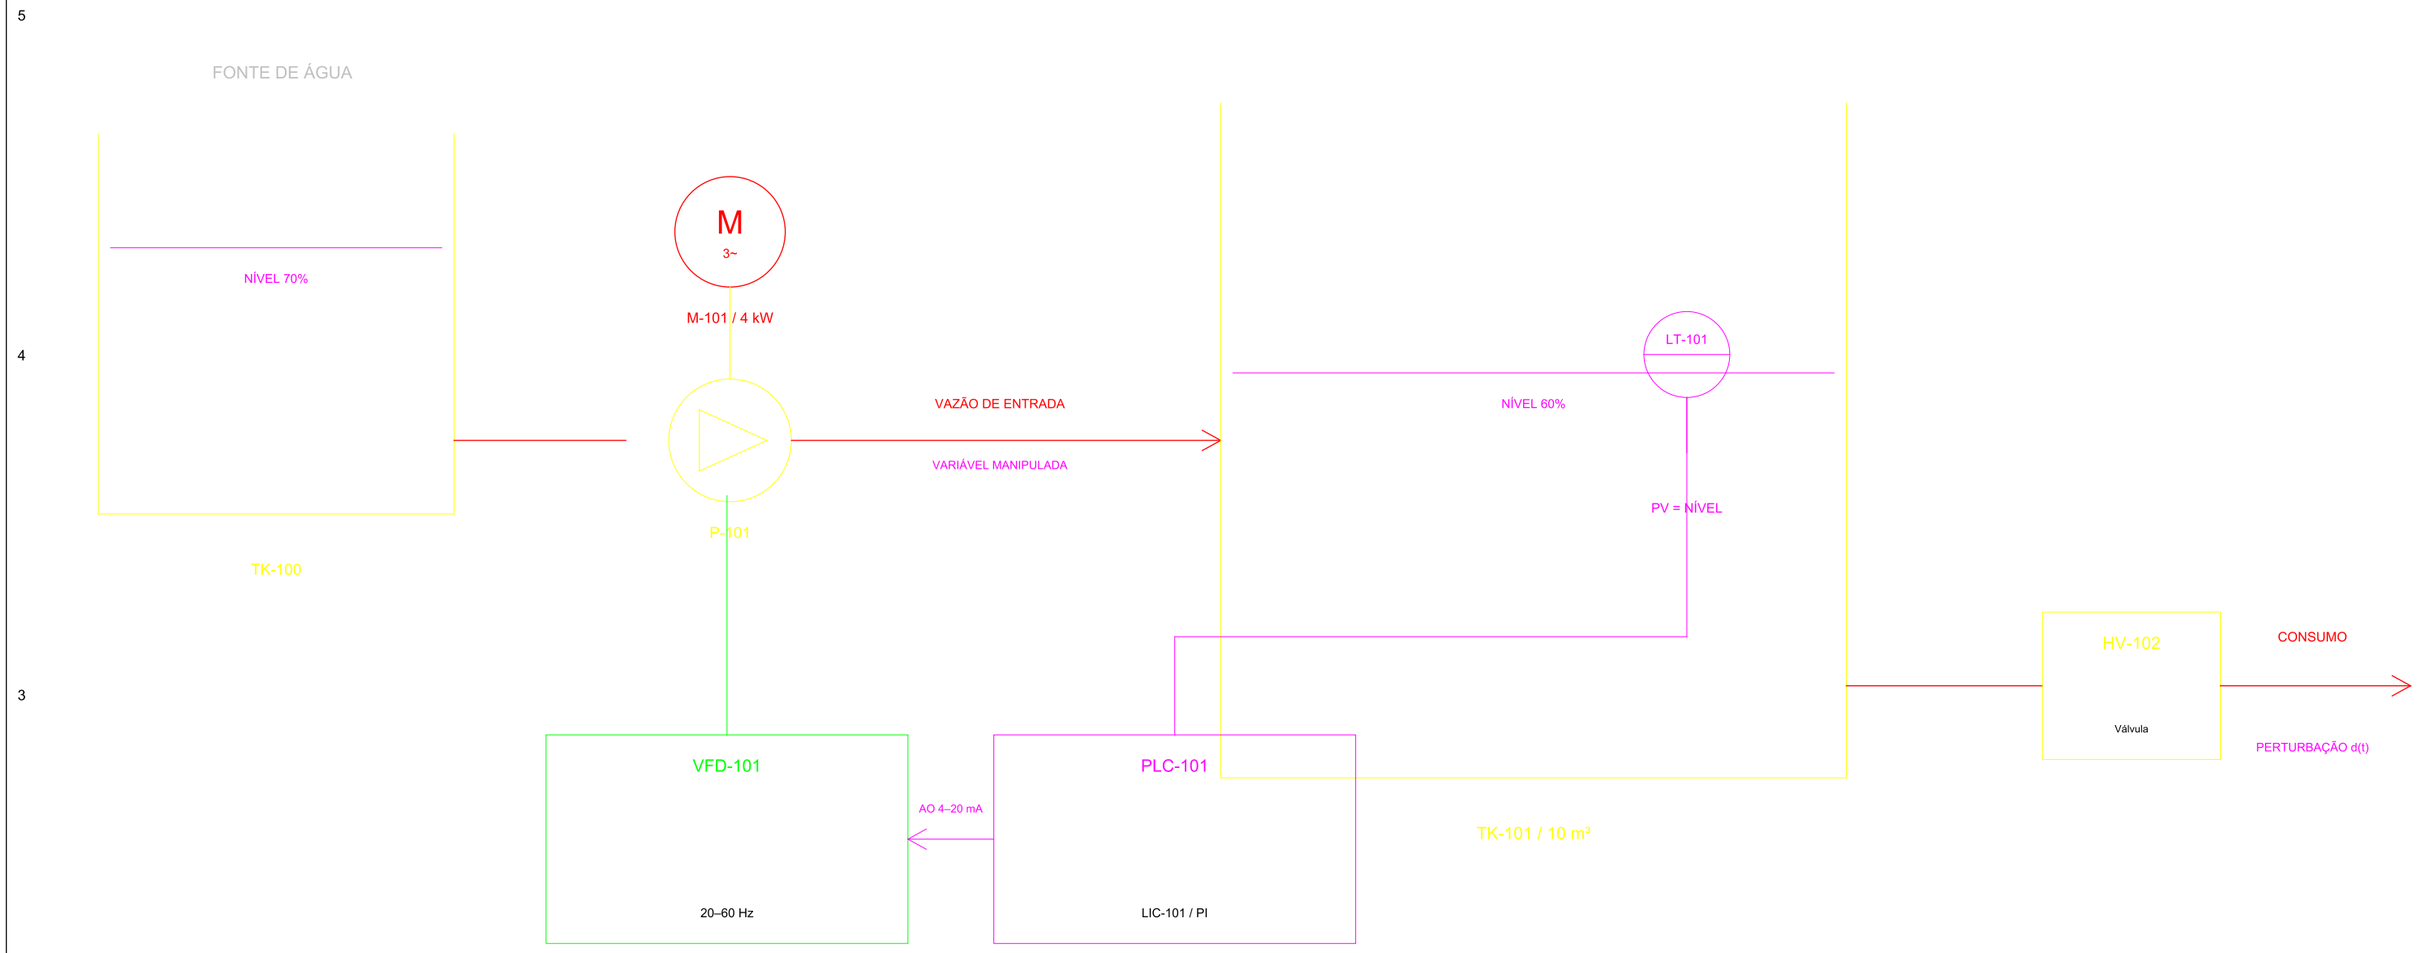


## LEGENDA

Linha grossa: tubulação | Tracejado funcional: sinal | FCV: válvula manual | NRV: retenção

## NOTAS DA PRANCHA

TK-101: 10 m³ (premissa). Operação normal: 30–80%; SP inicial: 60%.
A vazão de consumo é a perturbação principal da malha de nível.

## AVISO OBRIGATÓRIO

Projeto acadêmico e conceitual. Não deve ser utilizado para fabricação, instalação ou execução de serviços sem revisão, dimensionamento e responsabilidade de profissional legalmente habilitado.

| REV. | DATA | DESCRIÇÃO | RESP. |
|---|---|---|---|
| 00 | 2026-09-08 | EMISSÃO INICIAL DO PROJETO 04 | R.E.M.M. |

**PORTFOLIO DE**
**ENGENHARIA ELETRICA**
BASE ACADEMICA REPRODUZIVEL

**A3**
PAISAGEM

TITULO

FLUXOGRAMA DO PROCESSO

| AUTOR | DATA | REV. | PRANCHA |
|---|---|---|---|
| Rogério Eduardo Moreira Menegueli | 2026-09-08 | 00 | 01/06 |

| ARQUIVO | UNIDADES | ESCALA | FOLHA | STATUS |
|---|---|---|---|---|
| 01_fluxograma_processo.dxf | mm | S/ESC. | A3 | CONCEIT. |