
DIAGRAMA UNIFILAR DA ALIMENTACAO EV

Fronteiras, seis alimentadores e interface de gestao; protecoes ainda nao selecionadas

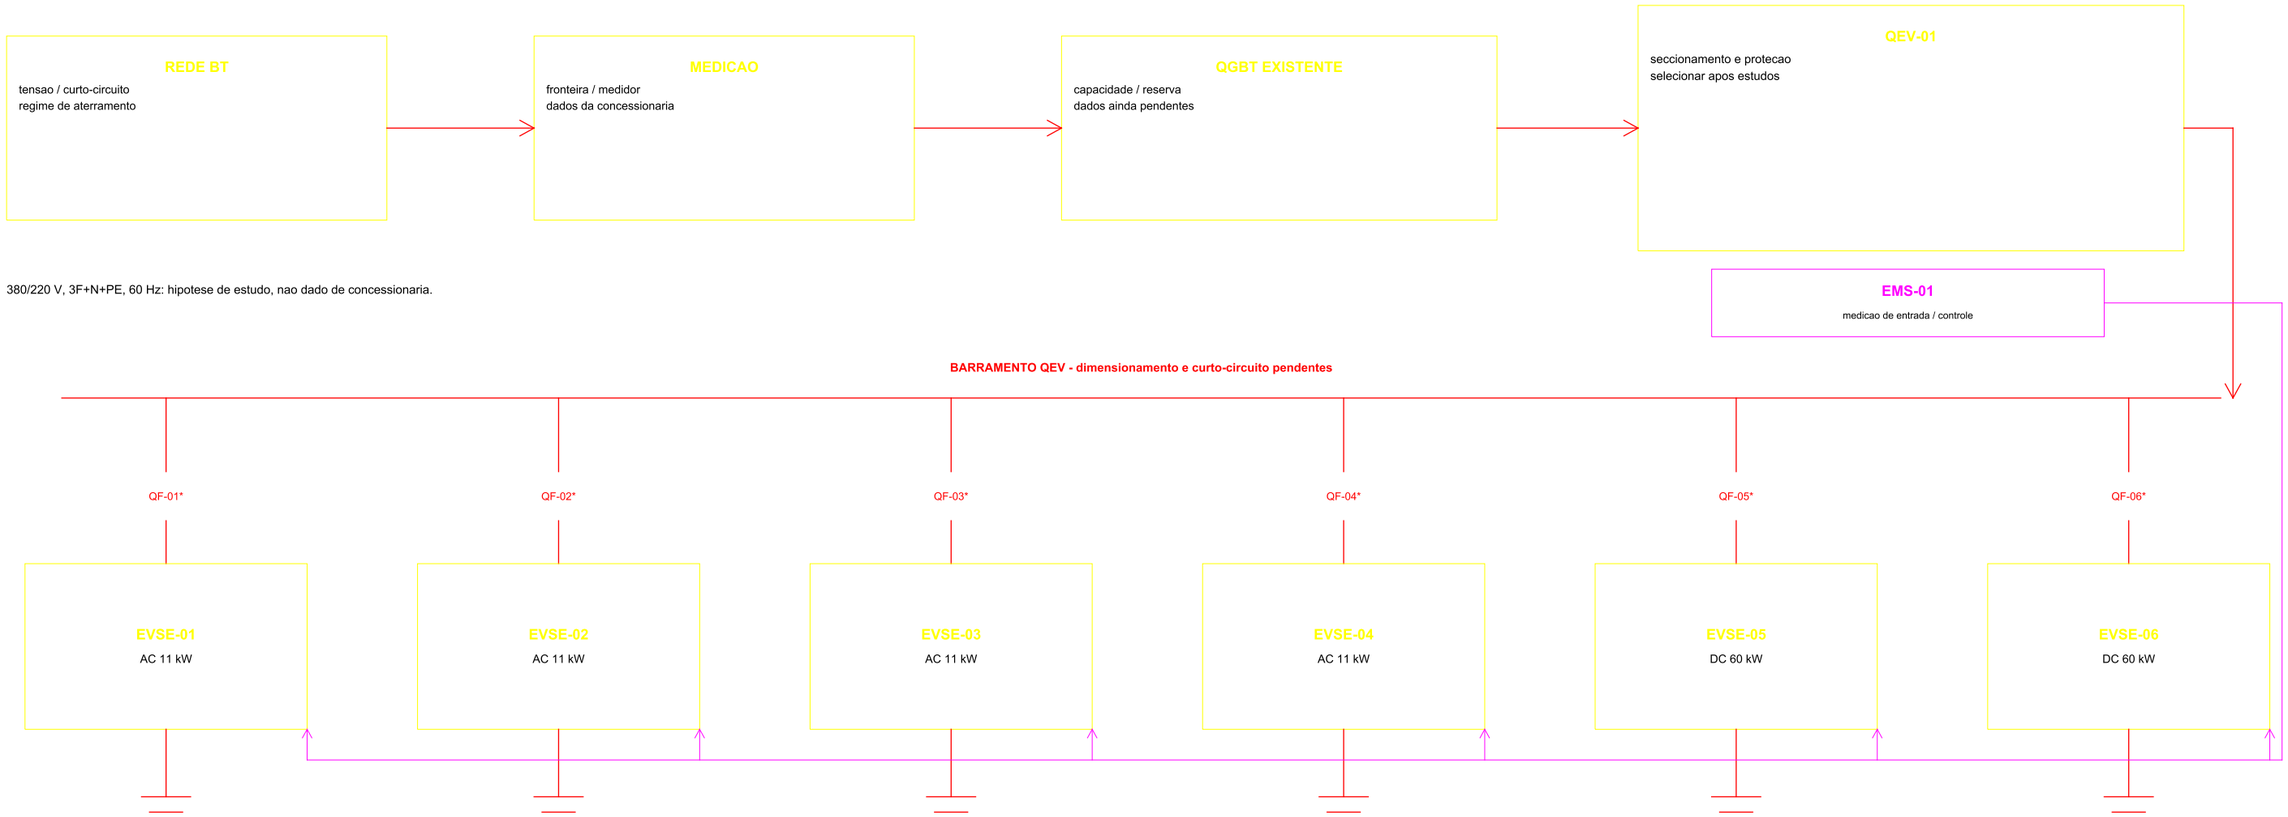

380/220 V, 3F+N+PE, 60 Hz: hipotese de estudo, nao dado de concessionaria.

LEGENDA

QEV: quadro dedicado | QGBT: quadro geral | QF-01 a QF-06: protecoes nao selecionadas | Pnom. saida assumida: 4 x 11 + 2 x 60 = 164 kW; nao e demanda da rede.

NOTAS DA PRANCHA

Tensao, aterramento, curto-circuito, seletividade e demanda nao foram confirmados.
QF: tipo, polos, corrente, curva e ajustes pendentes; interface EMS depende de dados OEM.

AVISO OBRIGATORIO

Projeto acadêmico e conceitual. Não deve ser utilizado para fabricação, instalação ou execução de serviços sem revisão, dimensionamento e responsabilidade de profissional legalmente habilitado.

REV.	DATA	DESCRICAO	RESP.
00	2026-11-06	EMISSAO INICIAL	R.E.M.M.

PORTFOLIO DE
ENGENHARIA ELETRICA
BASE ACADEMICA REPRODUZIVEL

A3
PAISAGEM

TITULO

DIAGRAMA UNIFILAR DA ALIMENTACAO EV

AUTOR	DATA	REV.	PRANCHA
Rogério Eduardo Moreira Menegueli	2026-11-06	00	02/03

ARQUIVO	UNIDADES	ESCALA	FOLHA	STATUS
02_diagrama_unifilar_estacao.dxf	mm	S/ESC.	A3	CONCEIT.