
DIAGRAMA UNIFILAR

Entrada 127/220 V, QG1, DPS1, DR1 e circuitos finais

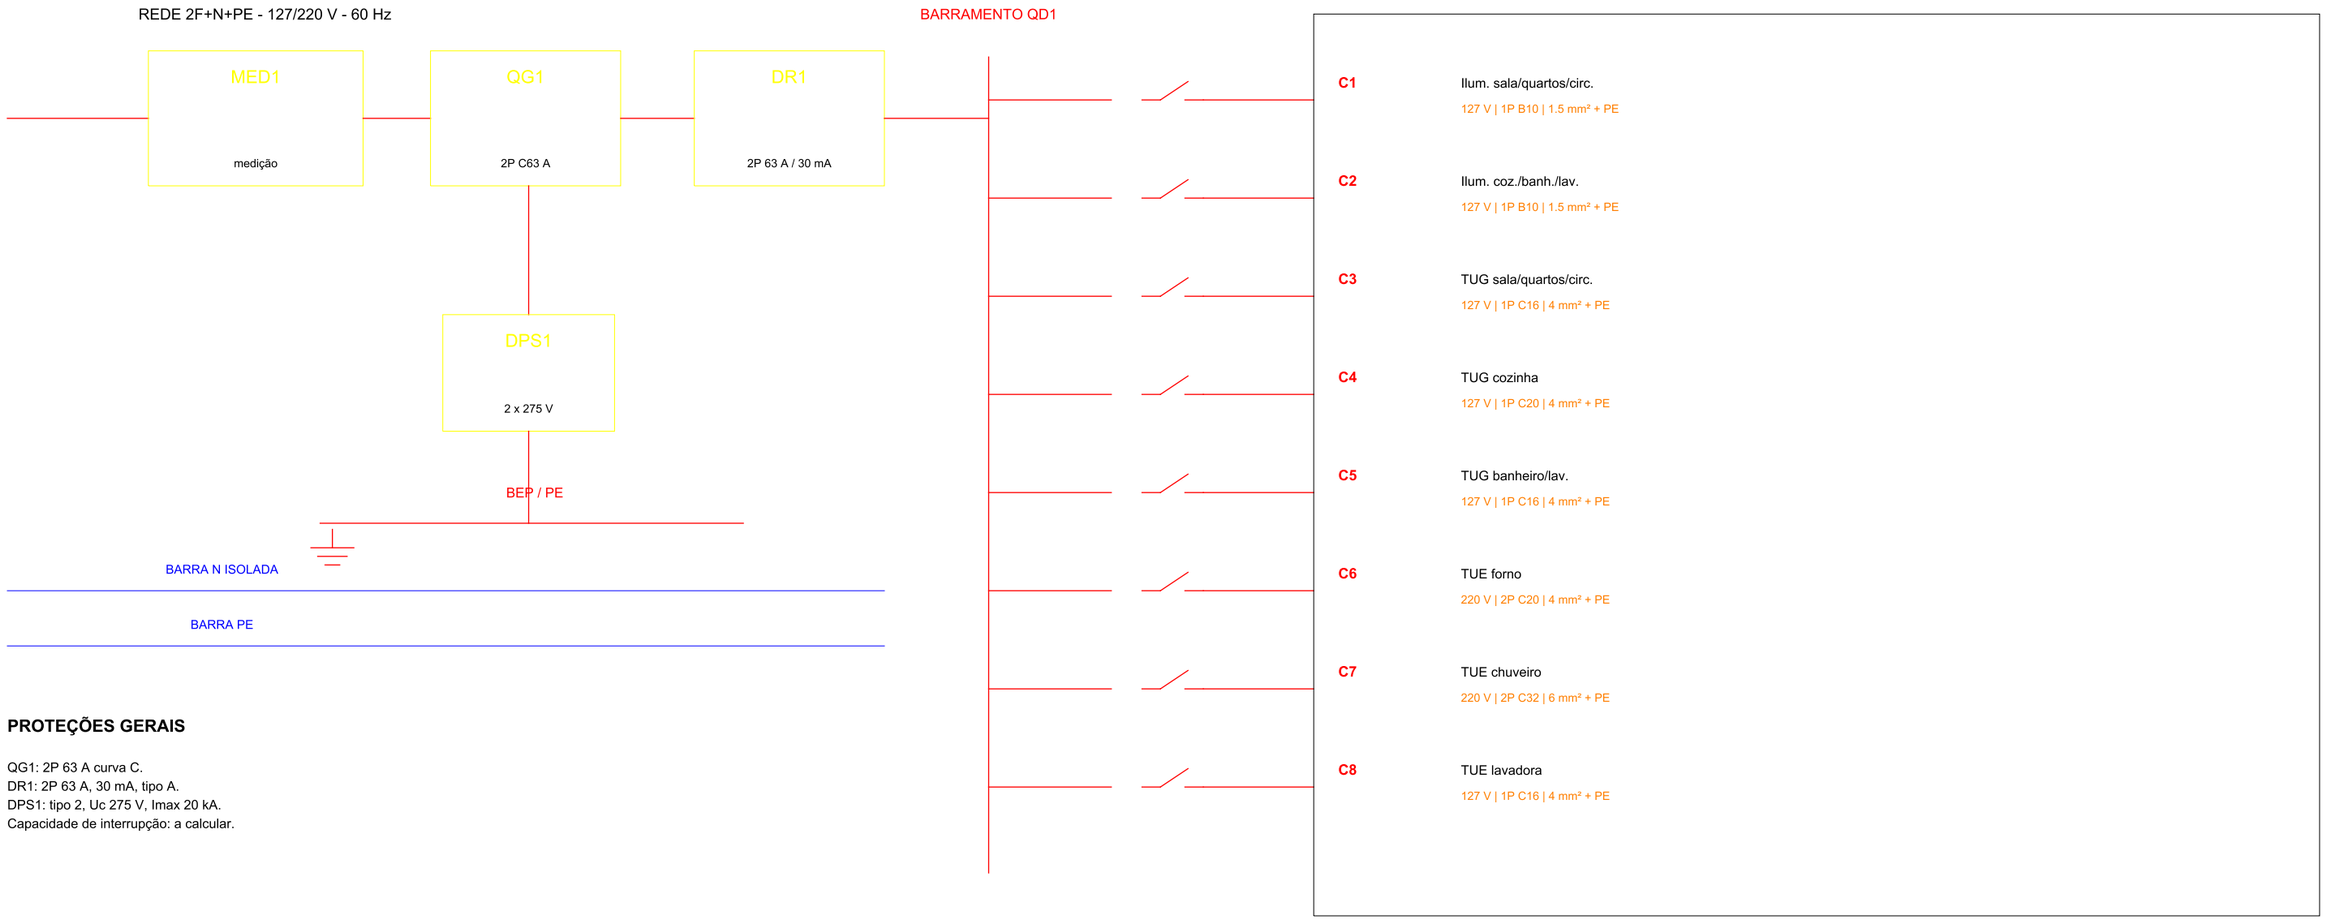

PROTEÇÕES GERAIS

QG1: 2P 63 A curva C.
DR1: 2P 63 A, 30 mA, tipo A.
DPS1: tipo 2, Uc 275 V, Imax 20 kA.
Capacidade de interrupção: a calcular.

LEGENDA

QG/DJ: disjuntor | DPS: surto | DR: diferencial | N/PE: barramentos

NOTAS DA PRANCHA

Capacidade de interrupção, curto-circuito e coordenação de DPS não calculados.
Neutro e PE permanecem separados a jusante no esquema TN-S conceitual.

AVISO OBRIGATÓRIO

Projeto acadêmico e conceitual. Não deve ser utilizado para fabricação, instalação ou execução de serviços sem revisão, dimensionamento e responsabilidade de profissional legalmente habilitado.

REV.	DATA	DESCRIÇÃO	RESP.
00	2026-09-05	EMISSÃO INICIAL DO PROJETO 02	R.E.M.M.

PORTFOLIO DE
ENGENHARIA ELETRICA
BASE ACADEMICA REPRODUZIVEL

A3
PAISAGEM

TITULO

DIAGRAMA UNIFILAR

AUTOR	DATA	REV.	PRANCHA
Rogério Eduardo Moreira Menegueli	2026-09-05	00	05/08

ARQUIVO	UNIDADES	ESCALA	FOLHA	STATUS
05_diagrama_unifilar.dxf	mm	S/ESC.	A3	CONCEIT.