
# INTERLIGAÇÕES DE CAMPO

Interfaces do painel com rede, motor, emergência e automação

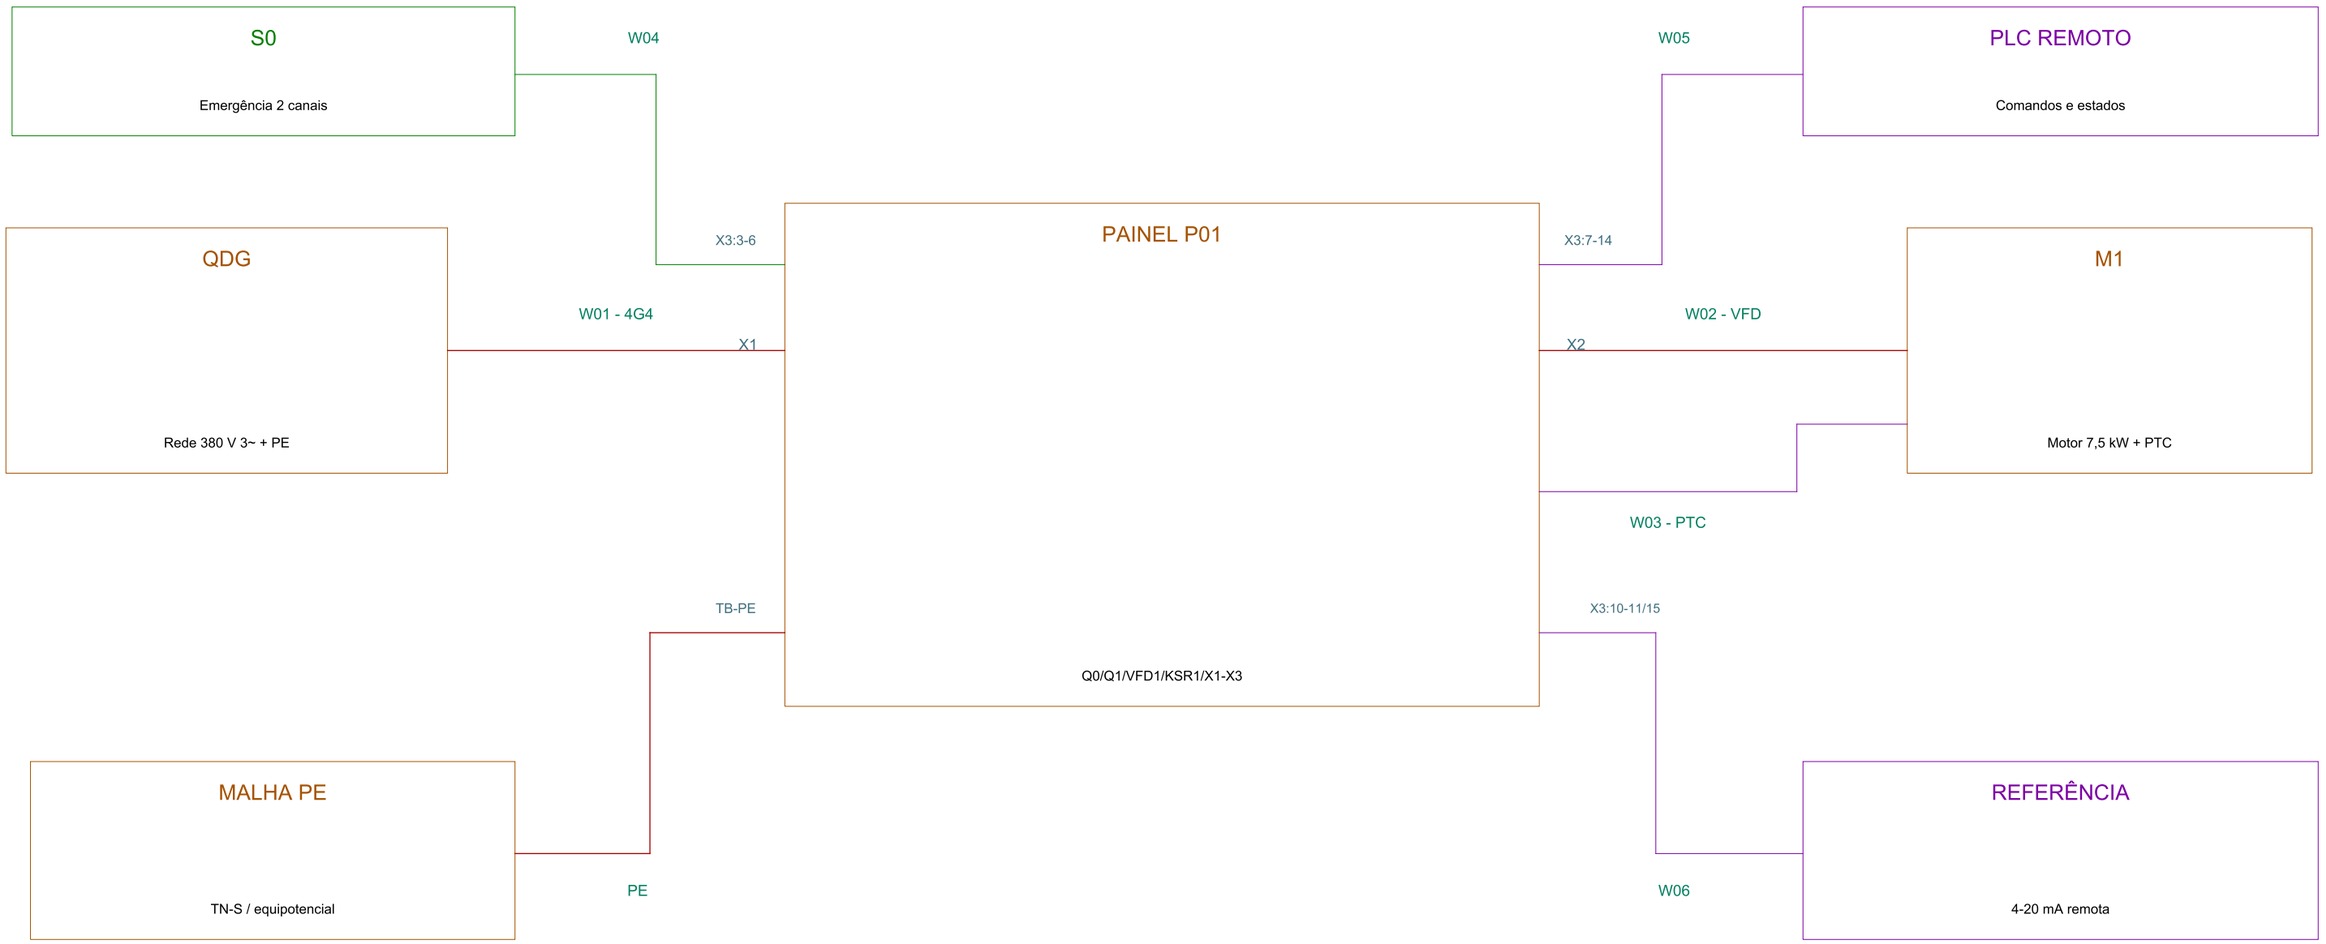


## LEGENDA

W01/W02: potência | W03/W04/W05/W06: comando e instrumentação

## NOTAS DA PRANCHA

Comprimentos são premissas para documentação e orçamento conceitual.
Rotas, segregação, queda de tensão e EMC dependem de levantamento em campo.

## AVISO OBRIGATÓRIO

Projeto acadêmico e conceitual. Não deve ser utilizado para fabricação, instalação ou execução de serviços sem revisão, dimensionamento e responsabilidade de profissional legalmente habilitado.

| REV. | DATA | DESCRIÇÃO | RESP. |
|---|---|---|---|
| 04 | 2026-11-06 | REVISAO VISUAL 04 | R.E.M.M. |

**PORTFOLIO DE**
**ENGENHARIA ELETRICA**
BASE ACADEMICA REPRODUZIVEL

**A3**
PAISAGEM

TITULO

INTERLIGAÇÕES DE CAMPO

| AUTOR | DATA | REV. | PRANCHA |
|---|---|---|---|
| Rogério Eduardo Moreira Menegueli | 2026-11-06 | 04 | 06/09 |

| ARQUIVO | UNIDADES | ESCALA | FOLHA | STATUS |
|---|---|---|---|---|
| 06_interligacoes_campo.dxf | mm | S/ESC. | A3 | CONCEIT. |