
DIAGRAMA UNIFILAR

Entrada 380/220 V, QGBT-05, QDF-05, QDL-05 e QADM-05

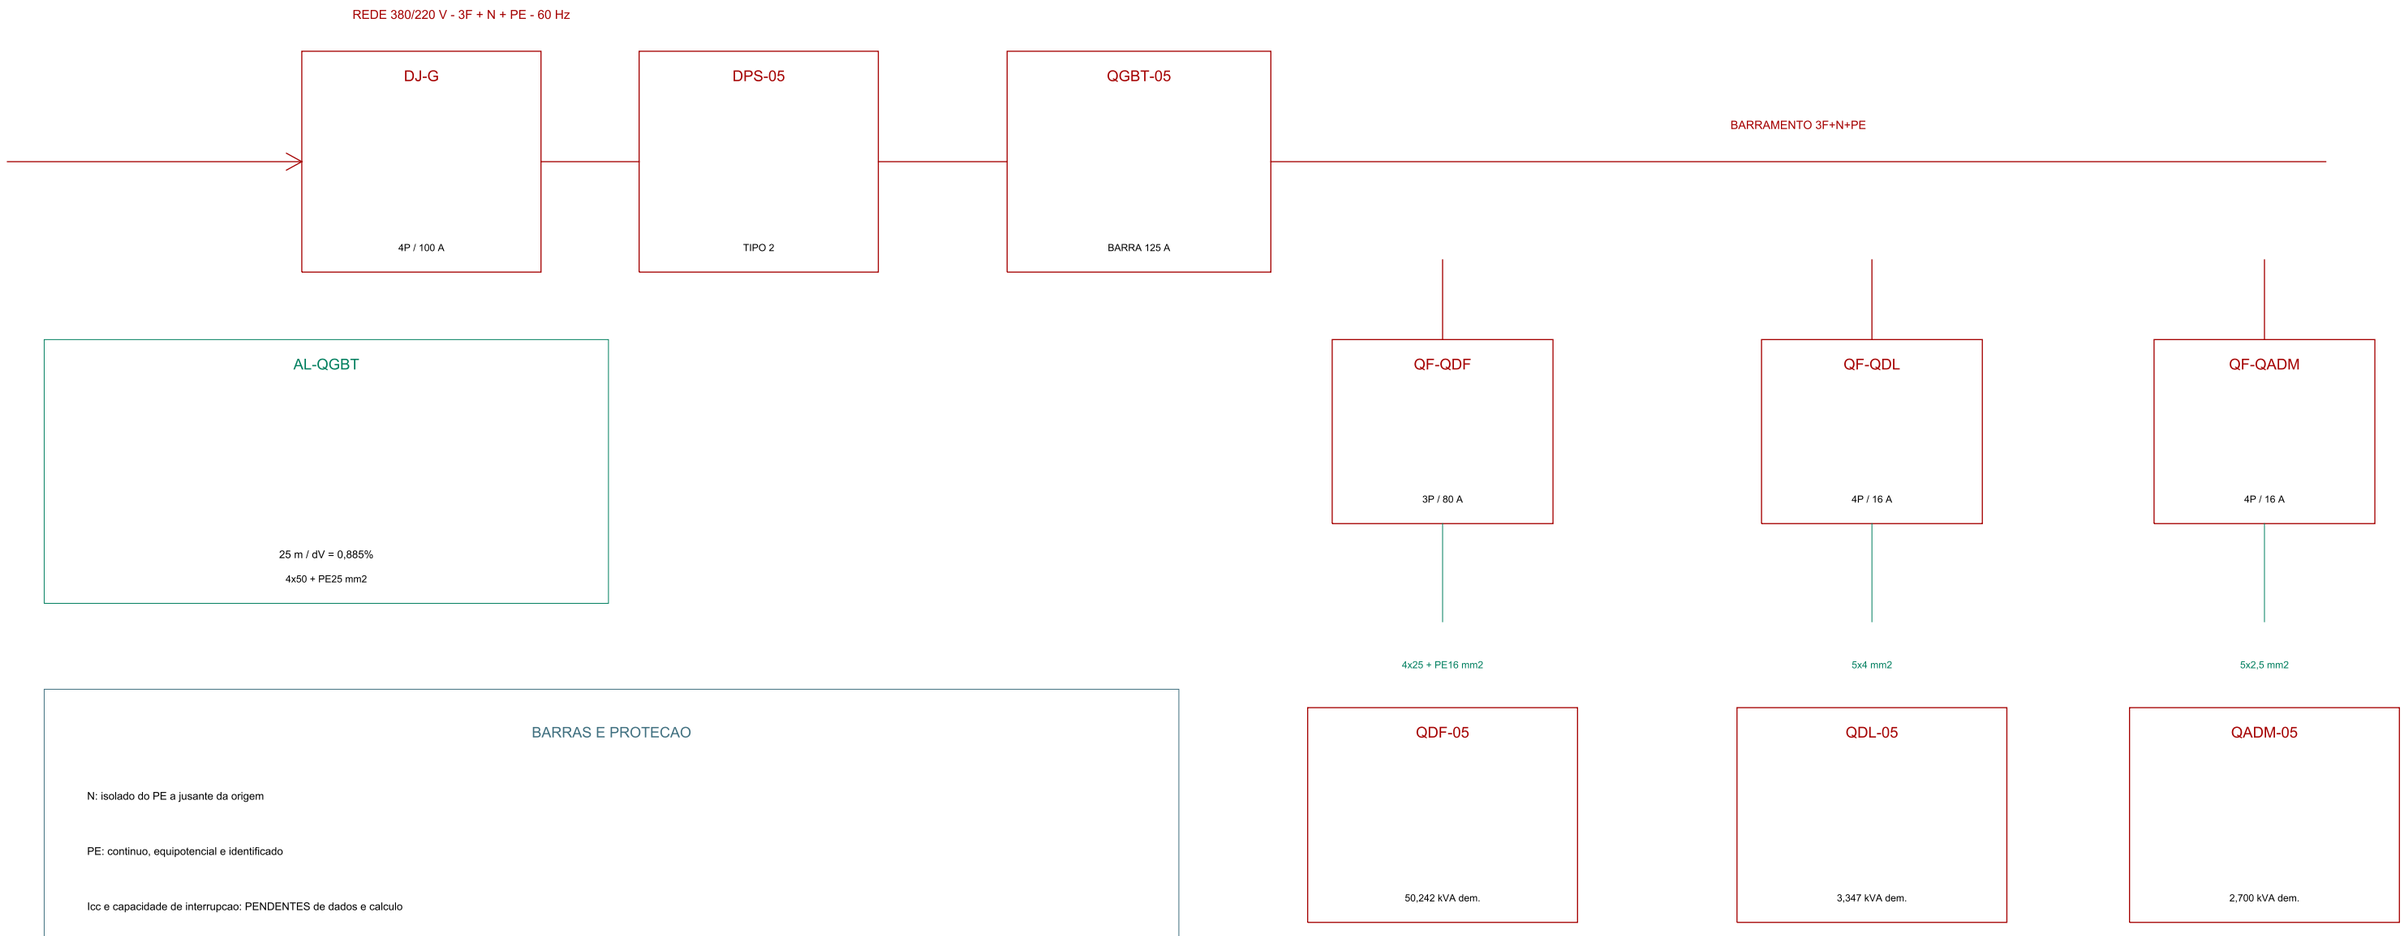

LEGENDA

DJ: disjuntor | DPS: surto | DR: diferencial | N/PE: barras separadas

NOTAS DA PRANCHA

Esquema TN-S conceitual a jusante do ponto de entrega. DR e DPS exigem coordenacao e selecao conforme rede, cargas, fabricante e estudo executivo.

AVISO OBRIGATORIO

Projeto acadêmico e conceitual. Não deve ser utilizado para fabricação, instalação ou execução de serviços sem revisão, dimensionamento e responsabilidade de profissional legalmente habilitado.

REV.	DATA	DESCRICAO	RESP.
04	2026-11-06	METODO DE CURTO-CIRCUITO E COORDENACAO	R.E.M.M.

PORTFOLIO DE
ENGENHARIA ELETRICA
BASE ACADEMICA REPRODUZIVEL

A3
PAISAGEM

TITULO

DIAGRAMA UNIFILAR

AUTOR	DATA	REV.	PRANCHA
Rogério Eduardo Moreira Menegueli	2026-11-06	04	05/09

ARQUIVO	UNIDADES	ESCALA	FOLHA	STATUS
05_diagrama_unifilar.dxf	mm	S/ESC.	A3	CONCEIT.