
PLANO DE DADOS PARA CURTO-CIRCUITO E COORDENACAO

Entradas e evidencias necessarias para revisar os seis pares da prancha 08

ROTEIRO DE VERIFICACAO — SEM RESULTADOS CALCULADOS

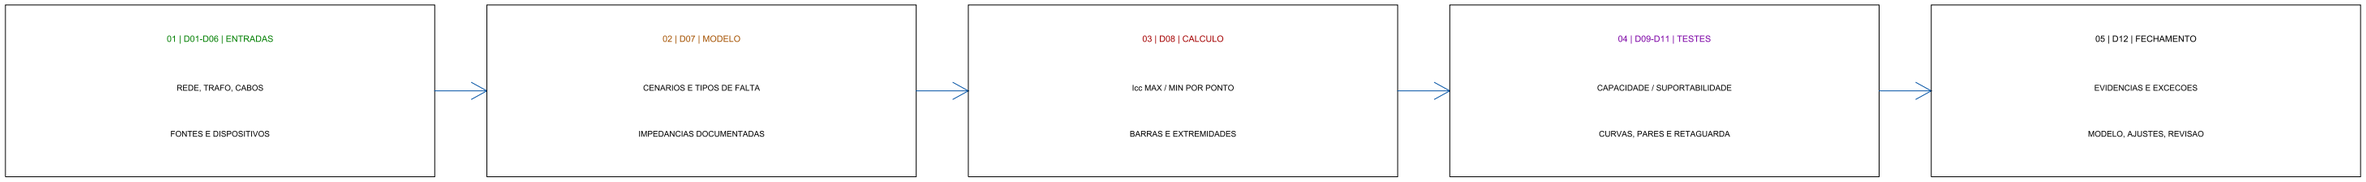

ID	GRUPO	DADO OU VERIFICACAO NECESSARIA	FONTE / REGISTRO	STATUS
D01	ENTRADA	Icc maximo e minimo, R/X e tensao no ponto de entrega	Concessionaria / protocolo vigente	PENDENTE
D02	ENTRADA	Transformadores em servico, kVA, Uk, ligacao, tap e aterramento	Placa, folha de dados e diagrama	PENDENTE
D03	ENTRADA	Comprimento, secao, material, instalacao e temperatura dos cabos	Levantamento e cadastro as-built	PENDENTE
D04	ENTRADA	Dados de motores, corrente de partida, regime e contribuicao de curto	Placas e manuais dos fabricantes	PENDENTE
D05	ENTRADA	Marca, modelo, polos, unidade de disparo e ajustes dos seis pares	Folhas de dados e ajustes selecionados	PENDENTE
D06	ENTRADA	Icu/Ics de disjuntores; Icw/Ipk de conjuntos, quando aplicaveis; tabela OEM de retaguarda	Catalogo, folha de dados e tabela OEM	PENDENTE
D07	CALCULO	Modelo da rede, criterio e classes de falta aplicaveis	Metodo de calculo e hipoteses documentadas	PENDENTE
D08	CALCULO	Icc maxima e minima em cada barra e extremidade de circuito	Memoria de calculo com pontos identificados	PENDENTE
D09	CALCULO	Sobrecarga, curto, I2t, suportabilidade do condutor e PE	Verificacao termica e de desligamento	PENDENTE
D10	CALCULO	Curvas TCC, tolerancias e limites de seletividade para cada par	Graficos e curvas dos fabricantes	PENDENTE
D11	CALCULO	Seletividade, retaguarda e limite de energia nos seis pares	Tabela comparativa pareada com criterio	PENDENTE
D12	REVISAO	Unifilar, ajustes, desvios, versao do modelo e revisao tecnica	Relatorio controlado, revisor identificado e lista de pendencias	PENDENTE

LEGENDA

D01-D06: entradas | D07-D08: modelo e Icc | D09-D11: verificacoes | D12: revisao | PENDENTE: sem evidencia

NOTAS DA PRANCHA

O estudo ainda nao foi calculado. Os doze grupos de dados permanecem pendentes.
Icc e capacidade de interrupcao nao foram definidos; a folha orienta verificacoes e evidencias.

AVISO OBRIGATORIO

Projeto acadêmico e conceitual. Não deve ser utilizado para fabricação, instalação ou execução de serviços sem revisão, dimensionamento e responsabilidade de profissional legalmente habilitado.

REV.	DATA	DESCRICAO	RESP.
05	2026-11-06	RASTREABILIDADE DO LAYOUT	R.E.M.M.

PORTFOLIO DE
ENGENHARIA ELETRICA
BASE ACADEMICA REPRODUZIVEL

A3
PAISAGEM

TITULO

PLANO DE DADOS PARA CURTO-CIRCUITO E COORDENACAO

AUTOR	DATA	REV.	PRANCHA
Rogério Eduardo Moreira Menegueli	2026-11-06	05	09/09

ARQUIVO	UNIDADES	ESCALA	FOLHA	STATUS
09_plano_dados_coordenacao.dxf	mm	S/ESC.	A3	CONCEIT.